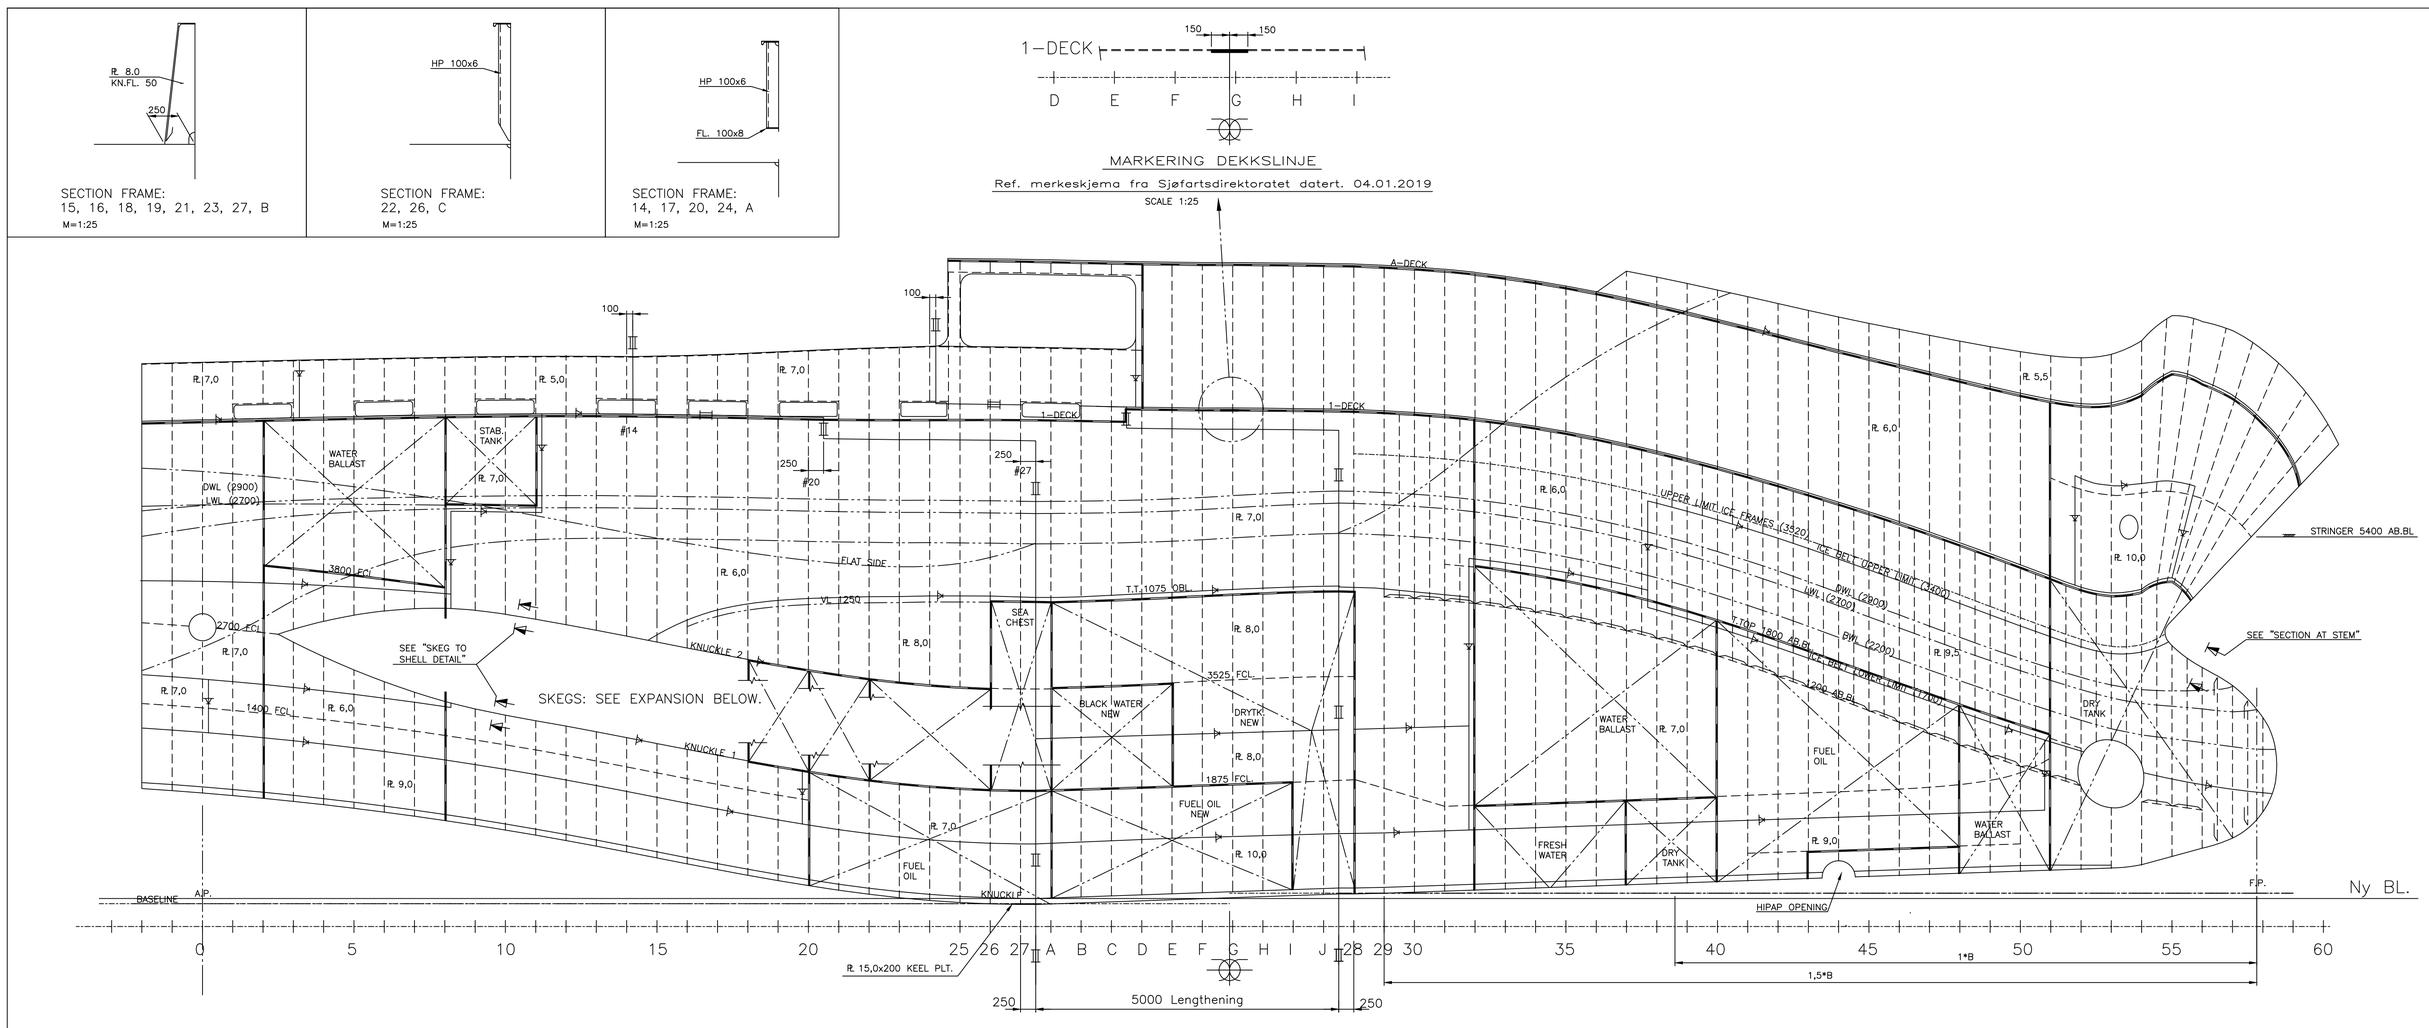

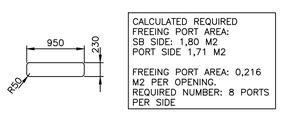

CALCULATED REQUIRED FREEING PORT AREA:
SB SIDE: 1,80 M2
PORT SIDE 1,71 M2

FREEING PORT AREA: 0,216 M2 PER OPENING.
REQUIRED NUMBER: 8 PORTS PER SIDE

FREEING PORT OPENINGS

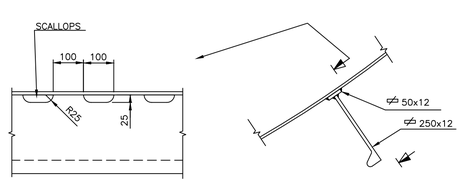

BILGE KEEL DETAILS

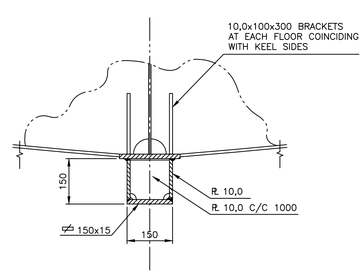

SECTION AT CL-KEEL
SCALE 1:10

MAIN DIMENSIONS:
SEE PK DRAWING NO. 166141 – MIDSHIP SECTION

BASED ON DWG. 166321A4	DATE: 31/08/2026	
PROJECT: FF GUNNERUS –LNVZ– SHELL EXPANSION S.B. SIDE	SCALE: 1:50	SHEETS: 1/2

Open use for research/teaching and other non-commercial activities
Commercial use is not permitted without approval (CC BY-NC 4.0)

NTNU

polarkonsult
PASSION FOR IMPROVING LIFE AT SEA
www.polarkonsult.com

This drawing is a derivative work based on the R/V Gunnerus open repository drawings, courtesy of Polarkonsult, published by NTNU

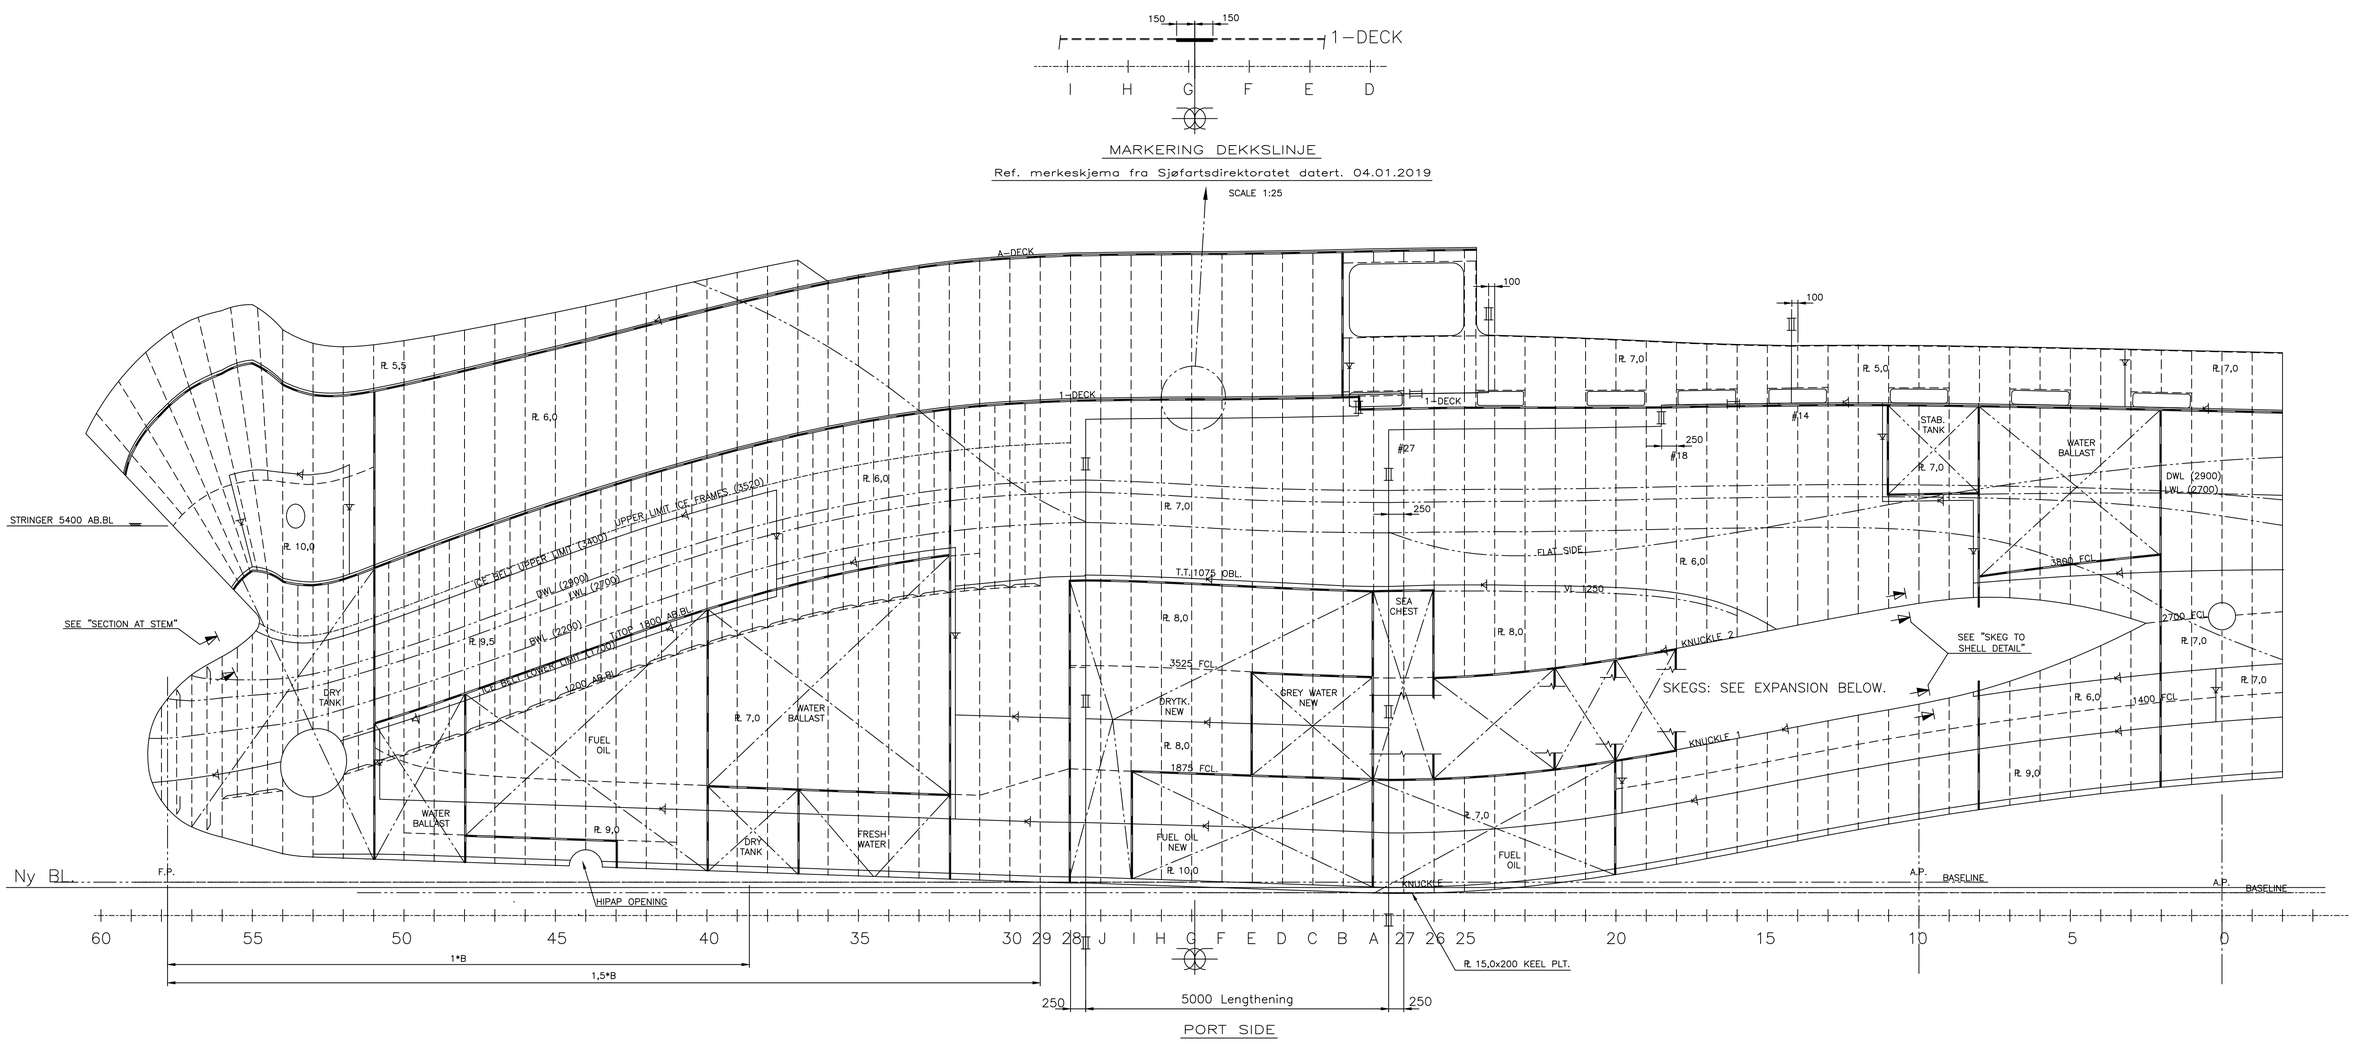

BASED ON DWG. 166321A4	DATE: 31/08/2026	
PROJECT: FF GUNNERUS –LNVZ– SHELL EXPANSION B.B. SIDE	SCALE: 1:50	SHEETS: 2/2

Open use for research/teaching and other non-commercial activities
Commercial use is not permitted without approval (CC BY-NC 4.0)

NTNU

polarkonsult
PASSION FOR IMPROVING LIFE AT SEA
www.polarkonsult.com

This drawing is a derivative work based on the R/V Gunnerus open repository drawings, courtesy of Polarkonsult, published by NTNU