

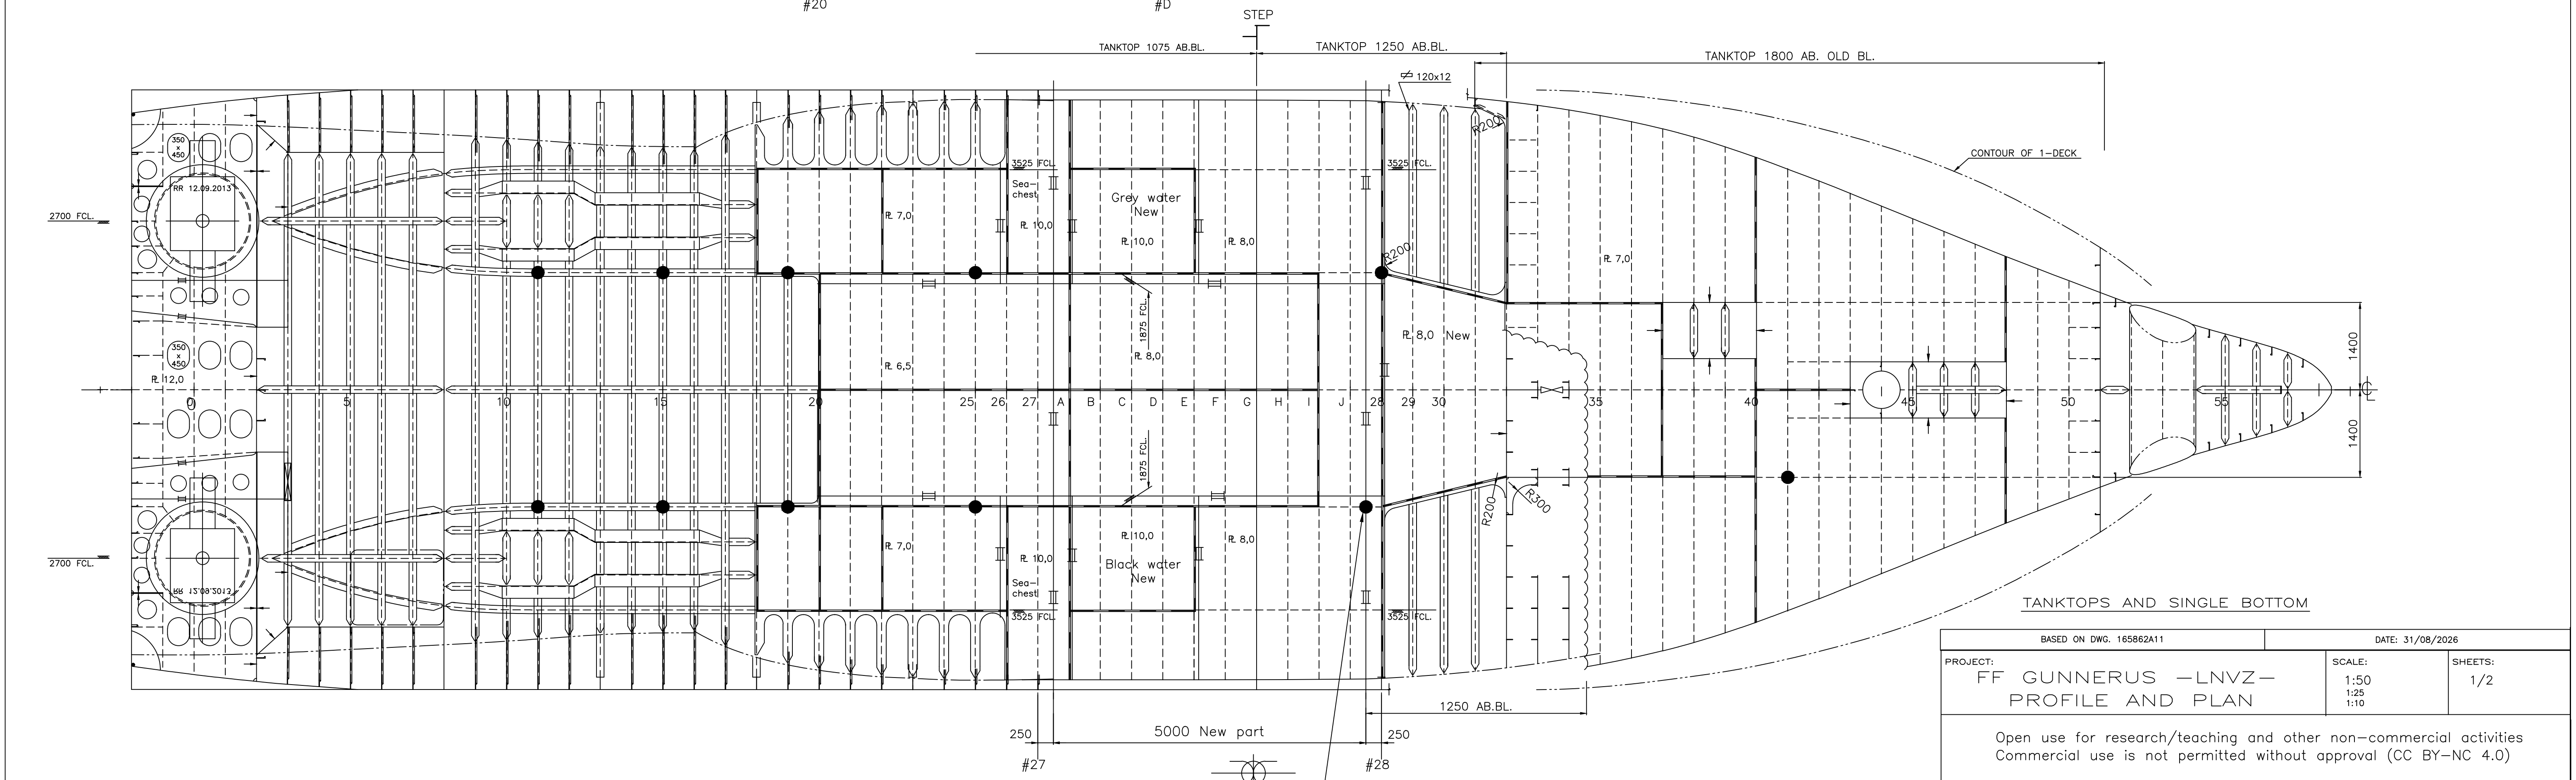
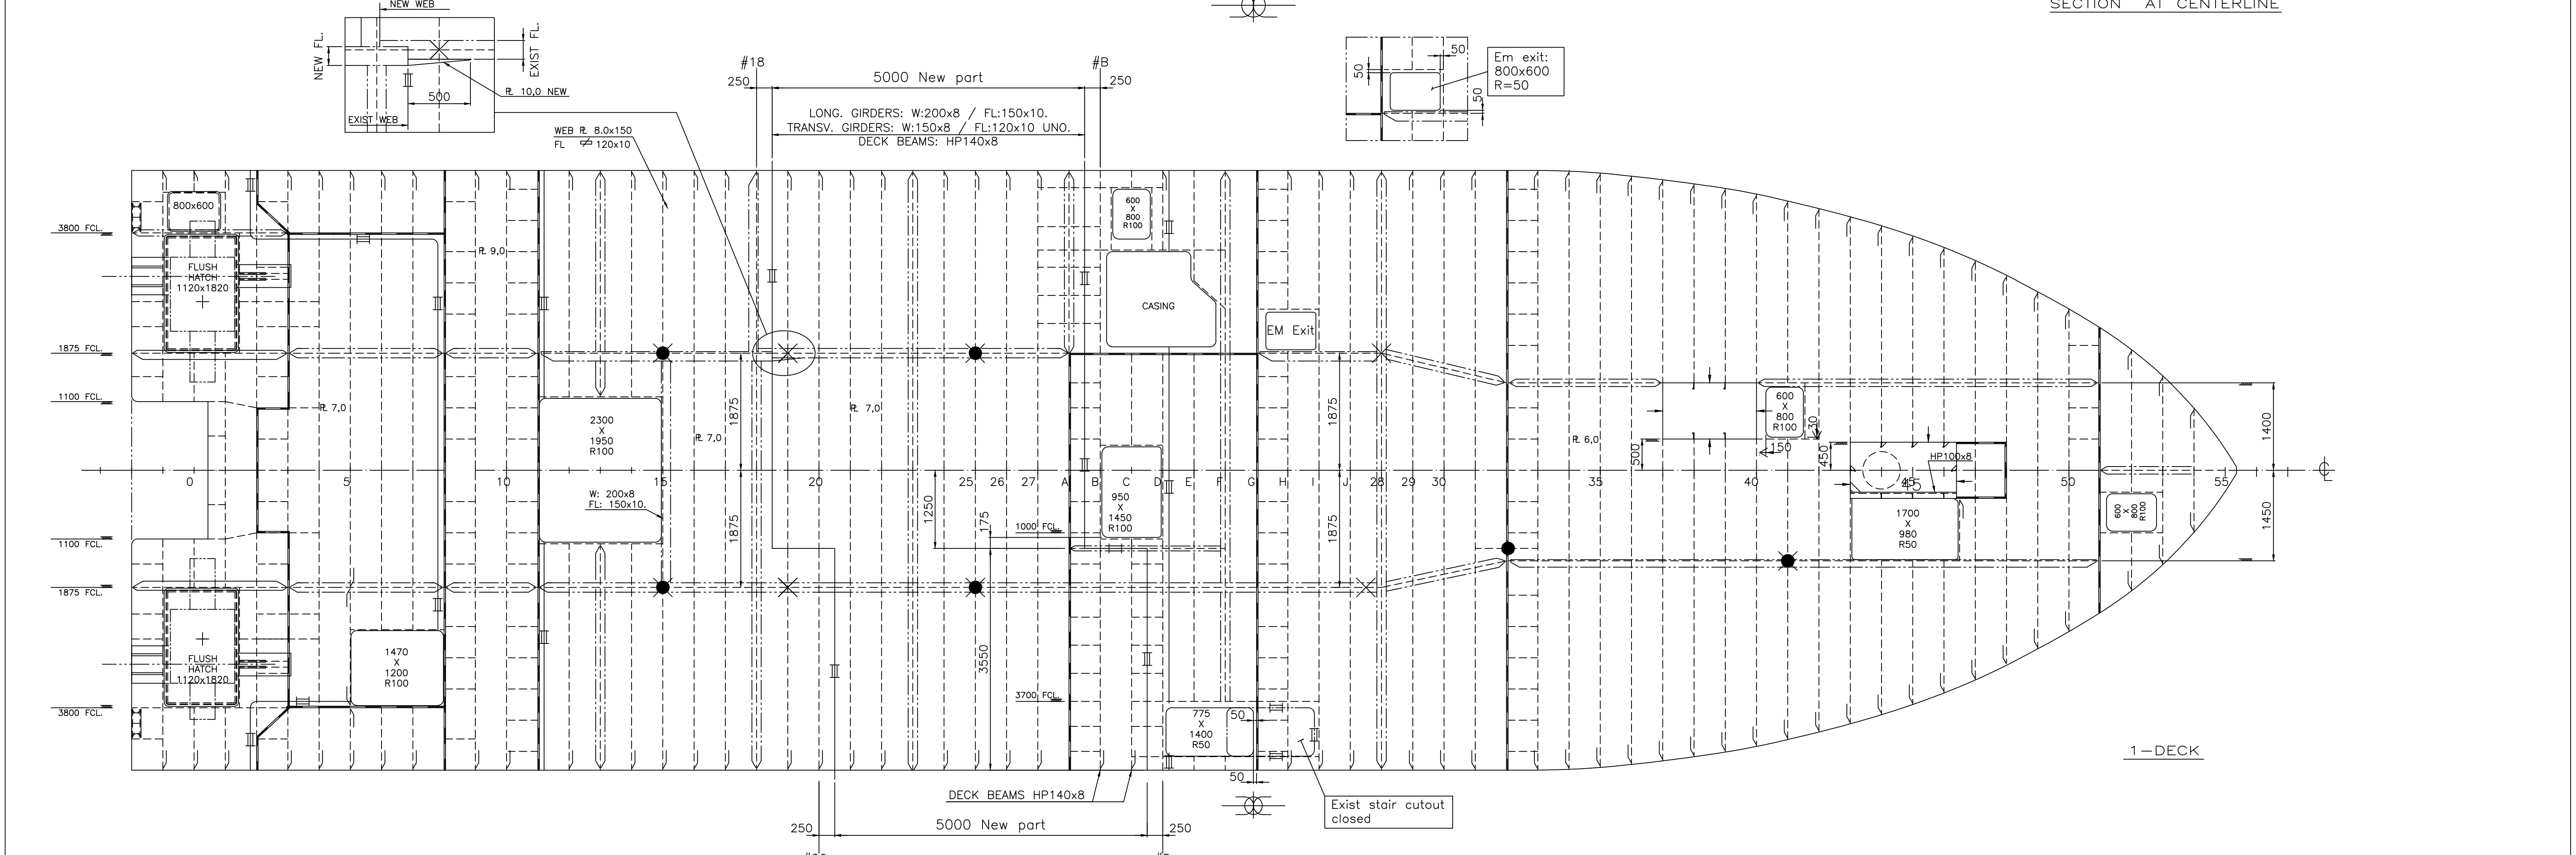


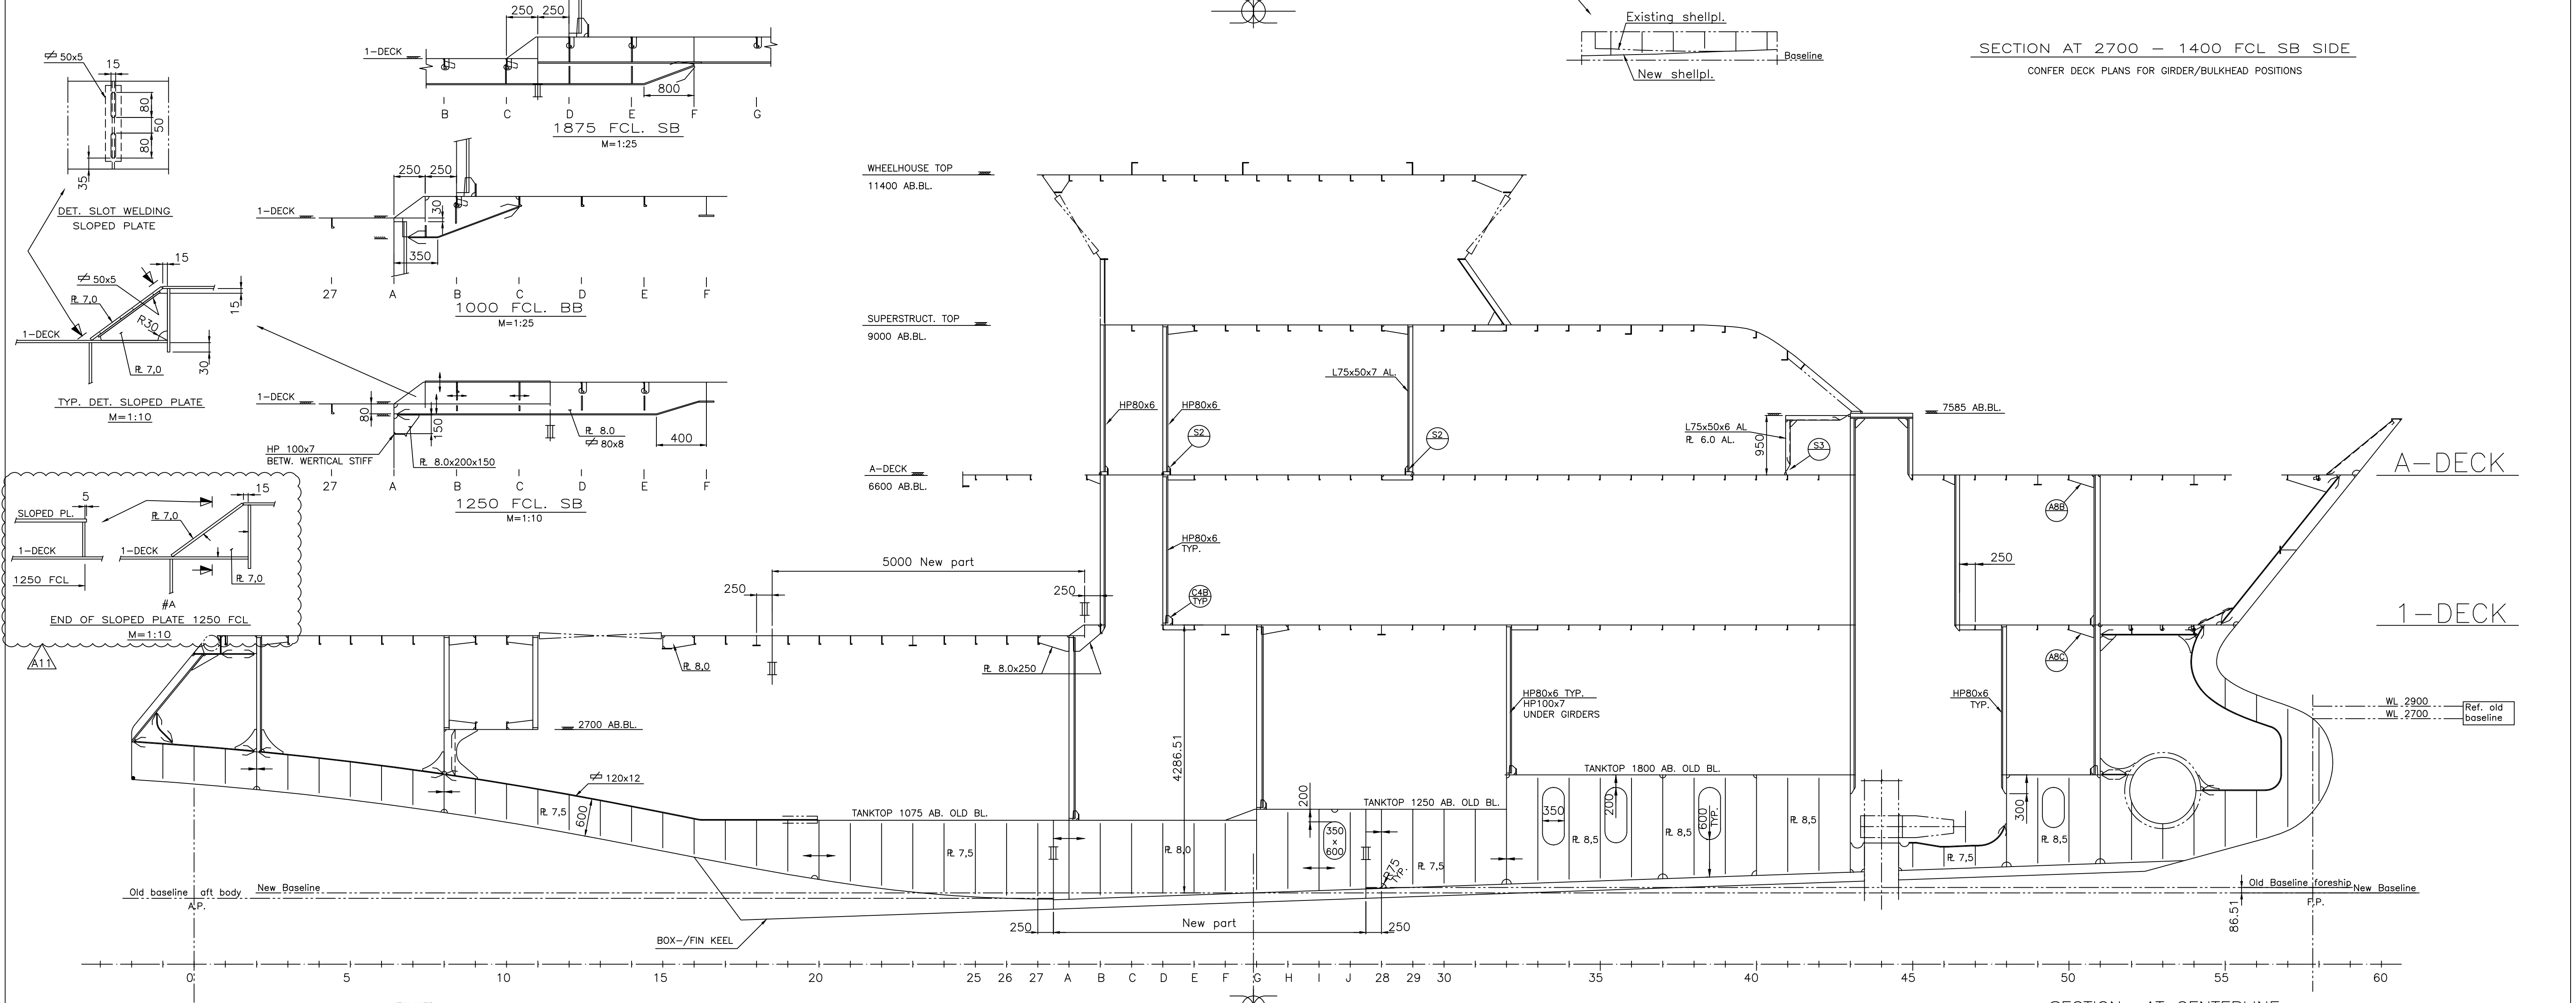

PROJECT: FF GUNNERUS - LNVZ - PROFILE AND PLAN		SCALE: 1:50 1:25 1:10	DATE: 31/08/2026 SHEETS: 1/2
Open use for research/teaching and other non-commercial activities Commercial use is not permitted without approval (CC BY-NC 4.0)			

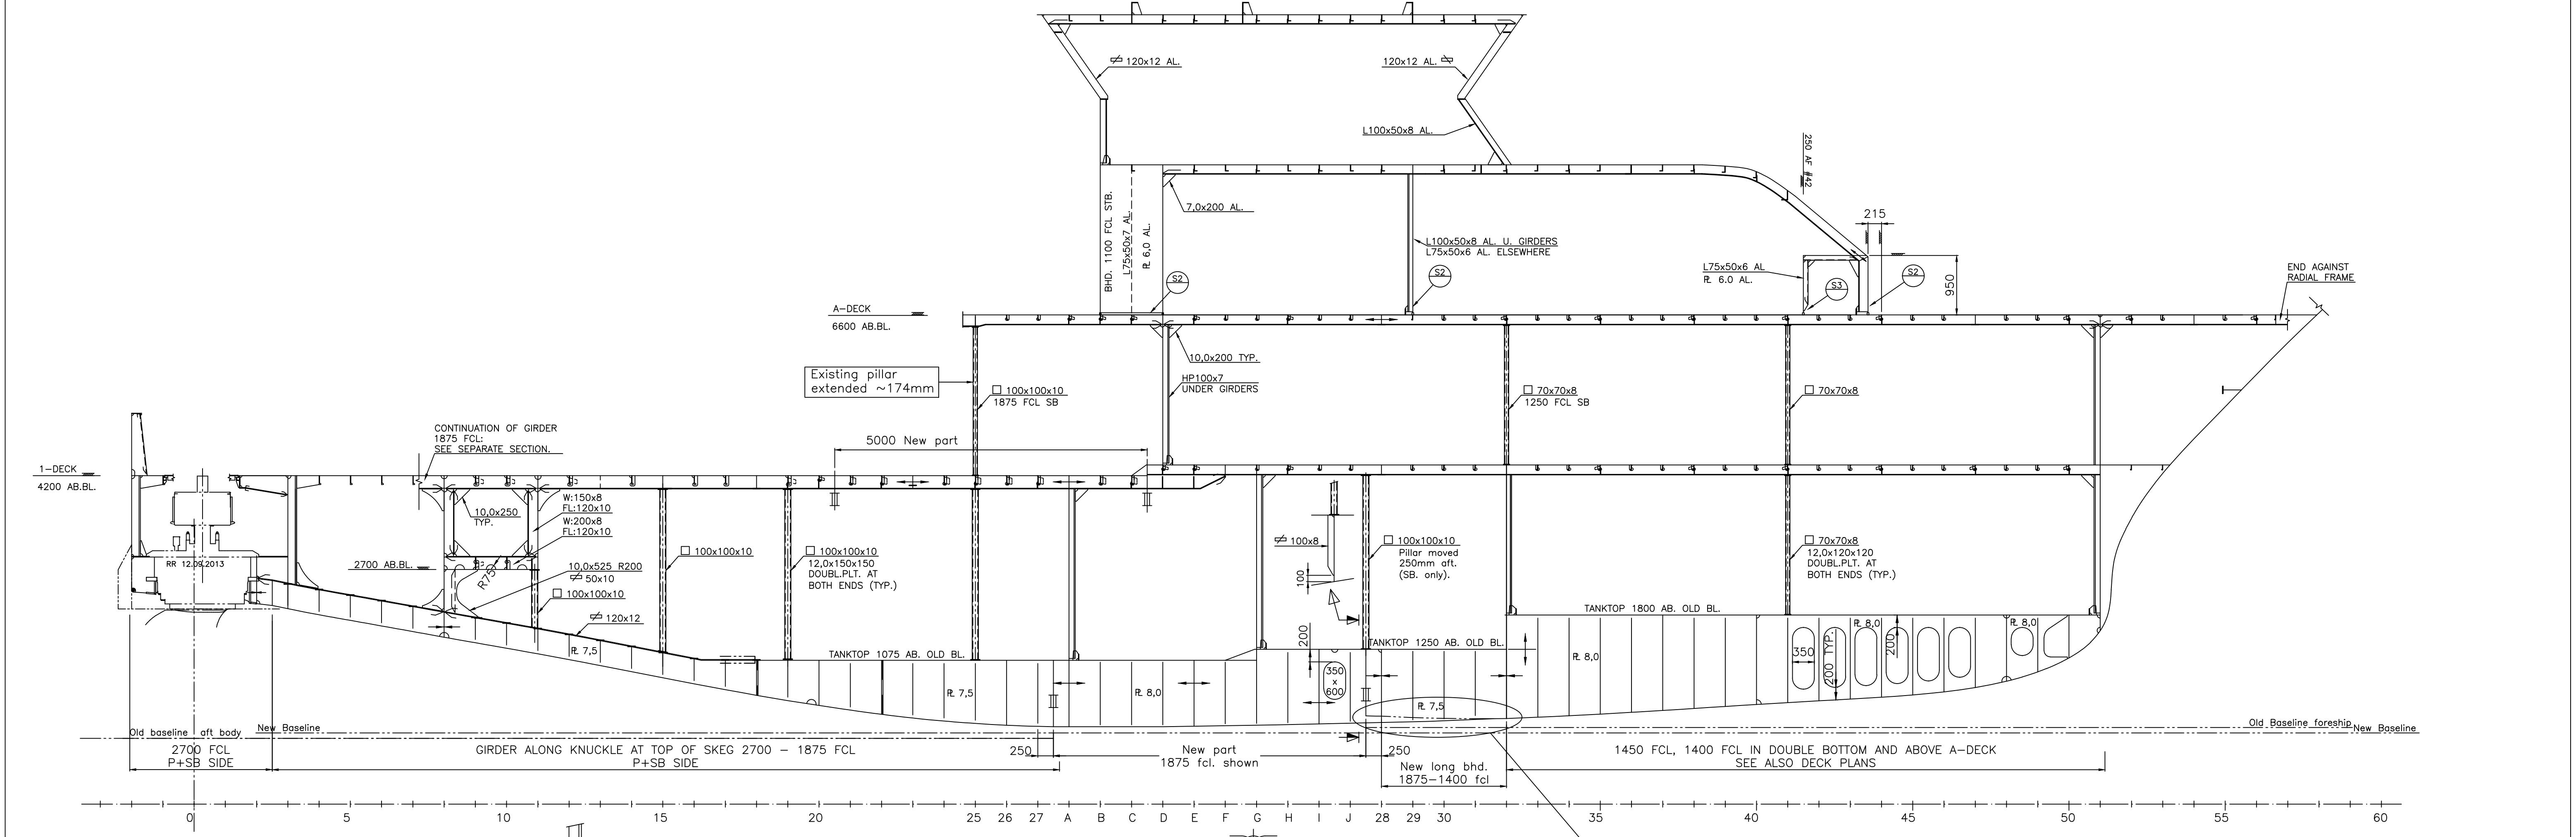