



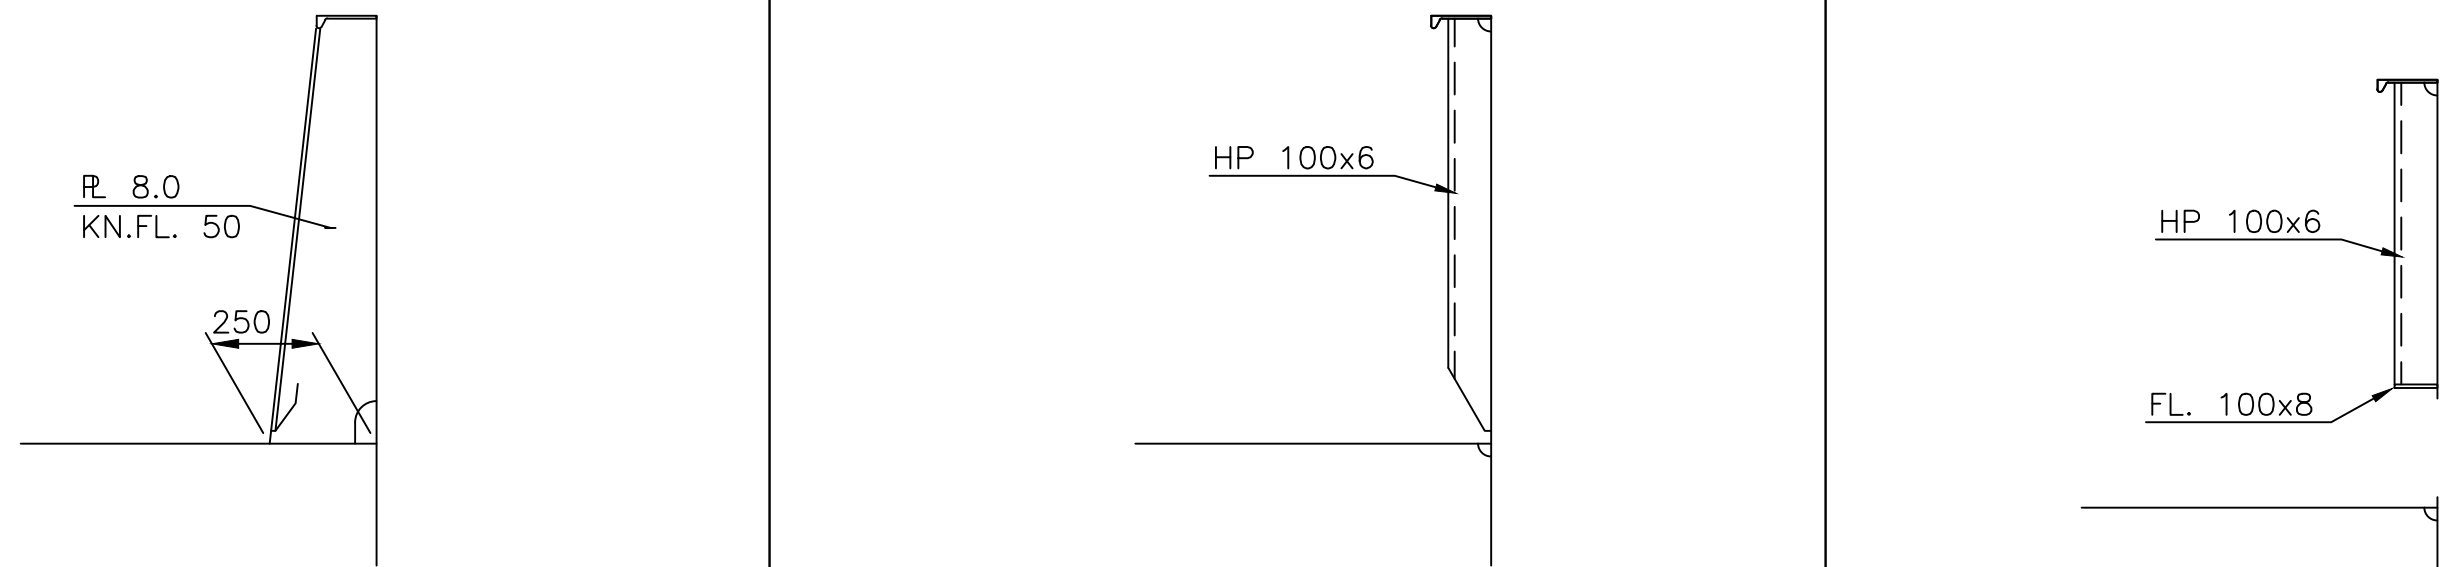

SECTION FRAME:
15, 16, 18, 19, 21, 23, 27, B
M=1:25

SECTION FRAME:
22, 26, C
M=1:25



SECTION FRAME:
14, 17, 20, 24, A
M=1:25

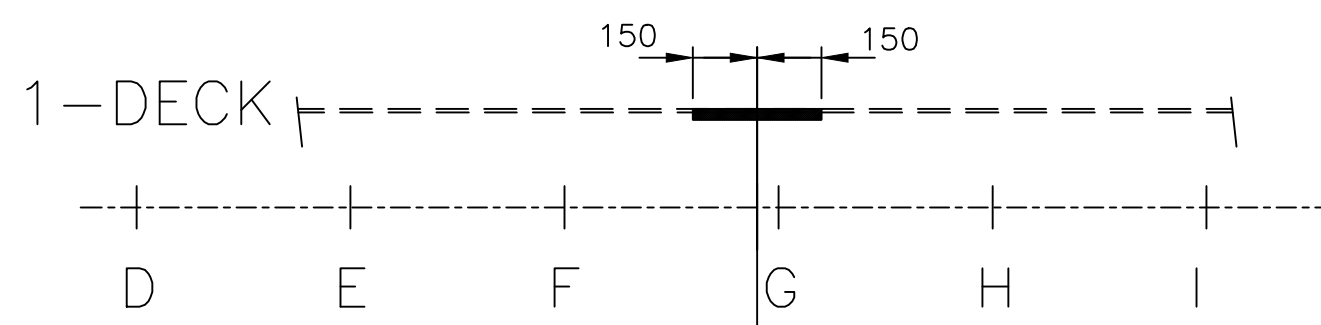

MARKERING DEKKS LINJE

Ref. merkeskjema fra Sjøfartsdirektoratet datert. 04.01.2019


SCALE 1:25

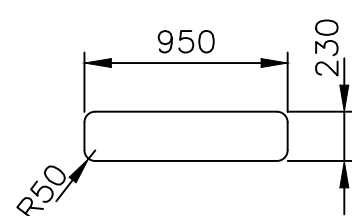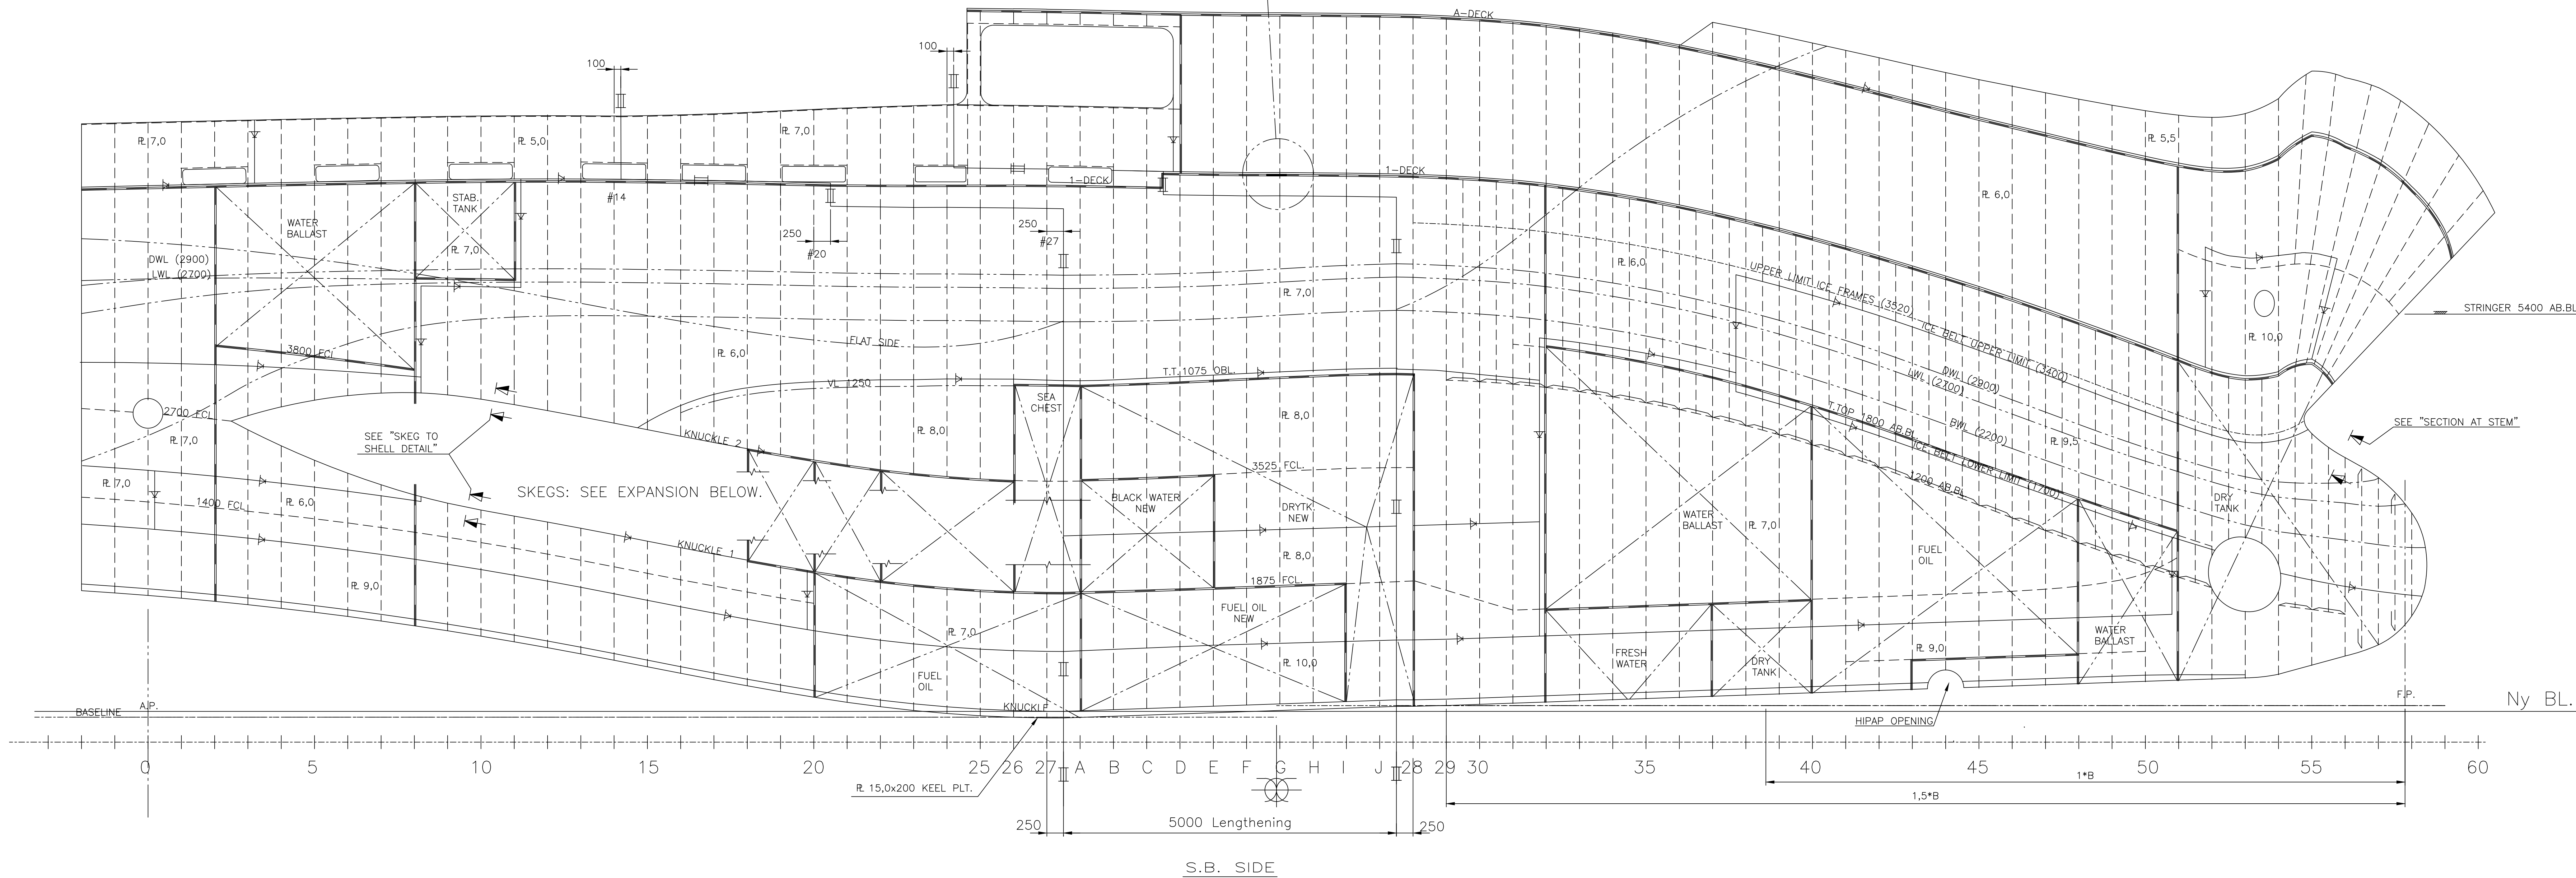


CALCULATED REQUIRED
FREEING PORT AREA:
SB SIDE: 1,80 M²
PORT SIDE 1,71 M²

FREEING PORT AREA: 0,216
M² PER OPENING.
REQUIRED NUMBER: 8 PORTS
PER SIDE

FREEING PORT OPENINGS

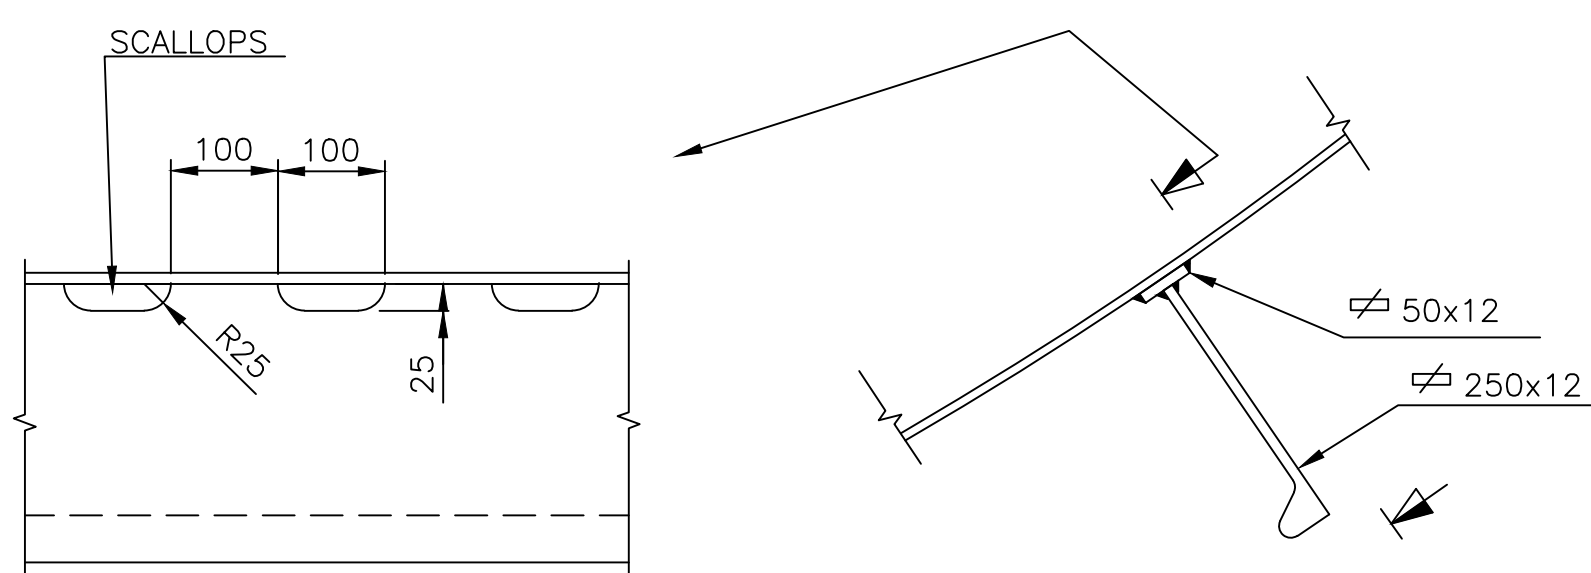

BILGE KEEL DETAILS

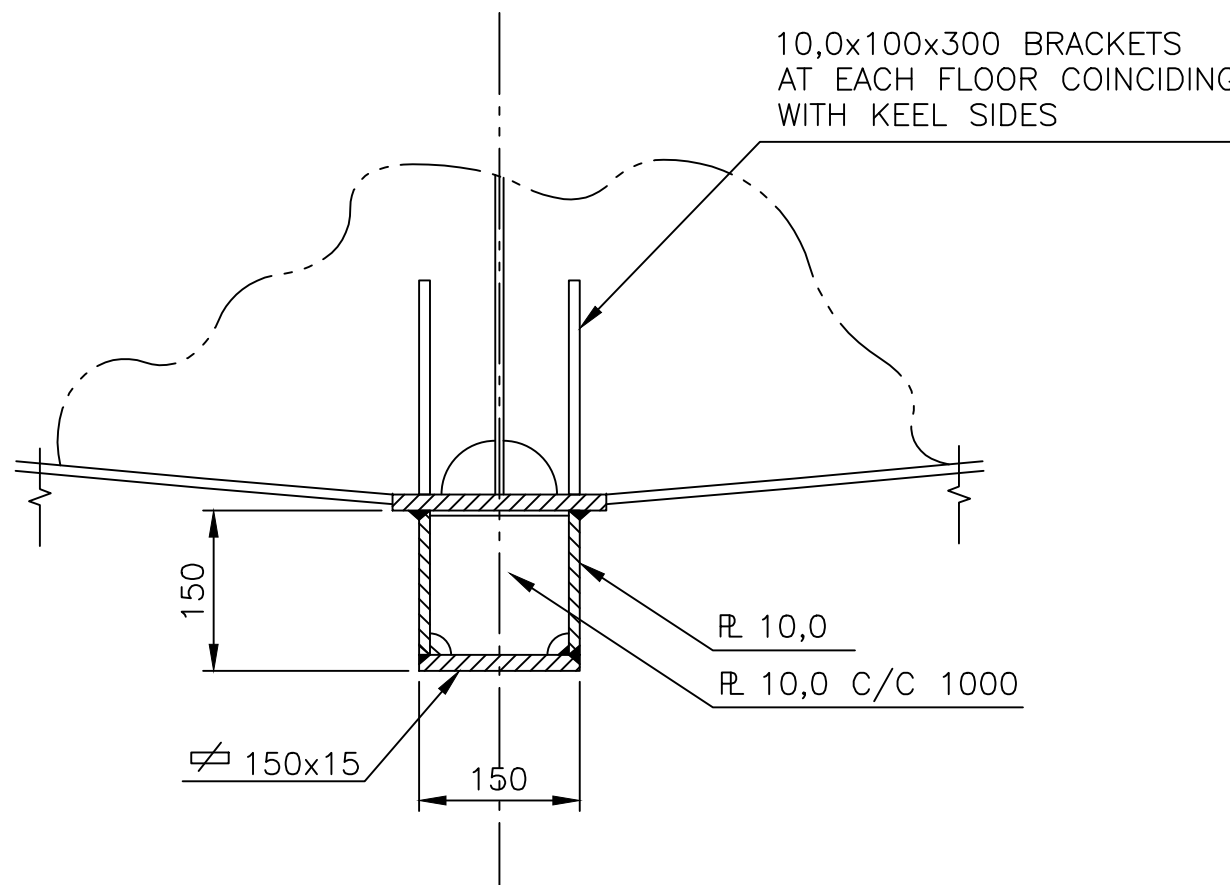

SECTION AT CL-KEEL

SCALE 1:10

MAIN DIMENSIONS:
SEE PK DRAWING NO. 166141 – MIDSHIP SECTION


BASED ON DWG. 166321A4		DATE: 31/08/2026	
PROJECT:	FF GUNNERUS – LNVZ – SHELL EXPANSION S.B. SIDE		SHEETS: 1/2



Open use for research/teaching and other non-commercial activities
Commercial use is not permitted without approval (CC BY-NC 4.0)

NTNU

polarkonsult
PASSION FOR IMPROVING LIFE AT SEA
www.polarkonsult.com

This drawing is a derivative
work based on the R/V
Gunnerus Platekledning
(166321A4), courtesy of
Polarkonsult, published by
NTNU

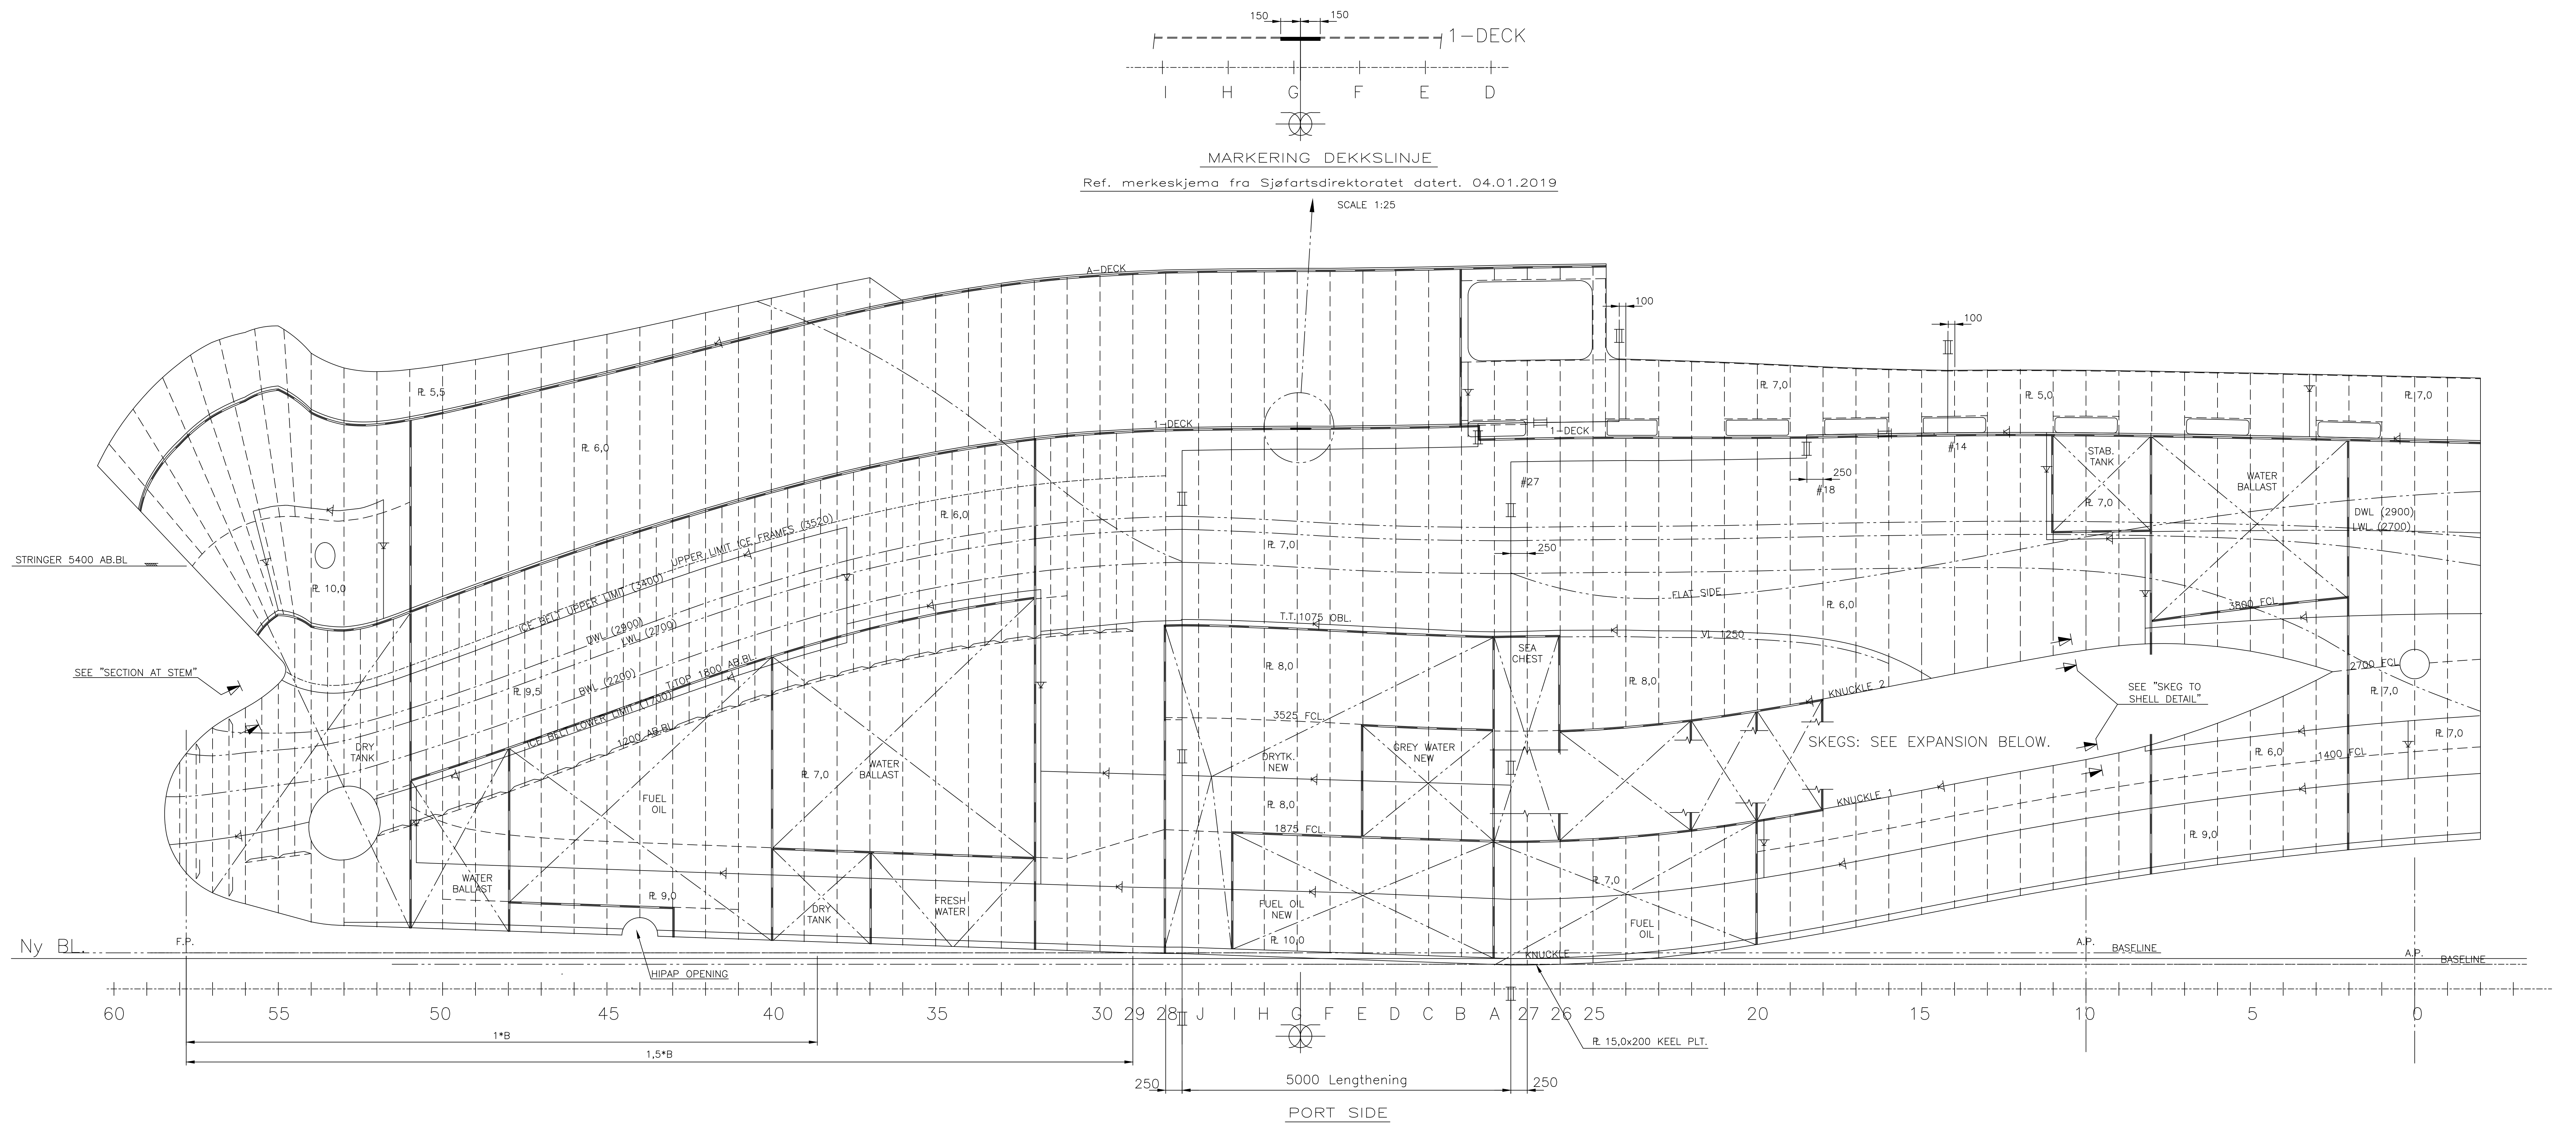

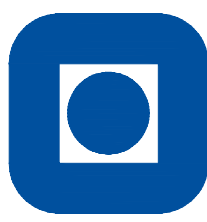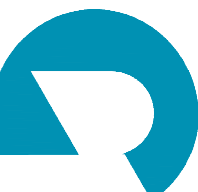BASED ON DWG. 166321A4		DATE: 31/08/2026	
PROJECT: FF GUNNERUS – LNVZ – SHELL EXPANSION B.B. SIDE		SCALE: 1:50	SHEETS: 2/2
Open use for research/teaching and other non-commercial activities Commercial use is not permitted without approval (CC BY-NC 4.0)			
 NTNU		 polarkonsult PASSION FOR IMPROVING LIFE AT SEA www.polarkonsult.com	
This drawing is a derivative work based on the R/V Gunnerus Platekledning (166321A4), courtesy of Polarkonsult, published by NTNU			