




1-DECK 4200 ABOVE BL

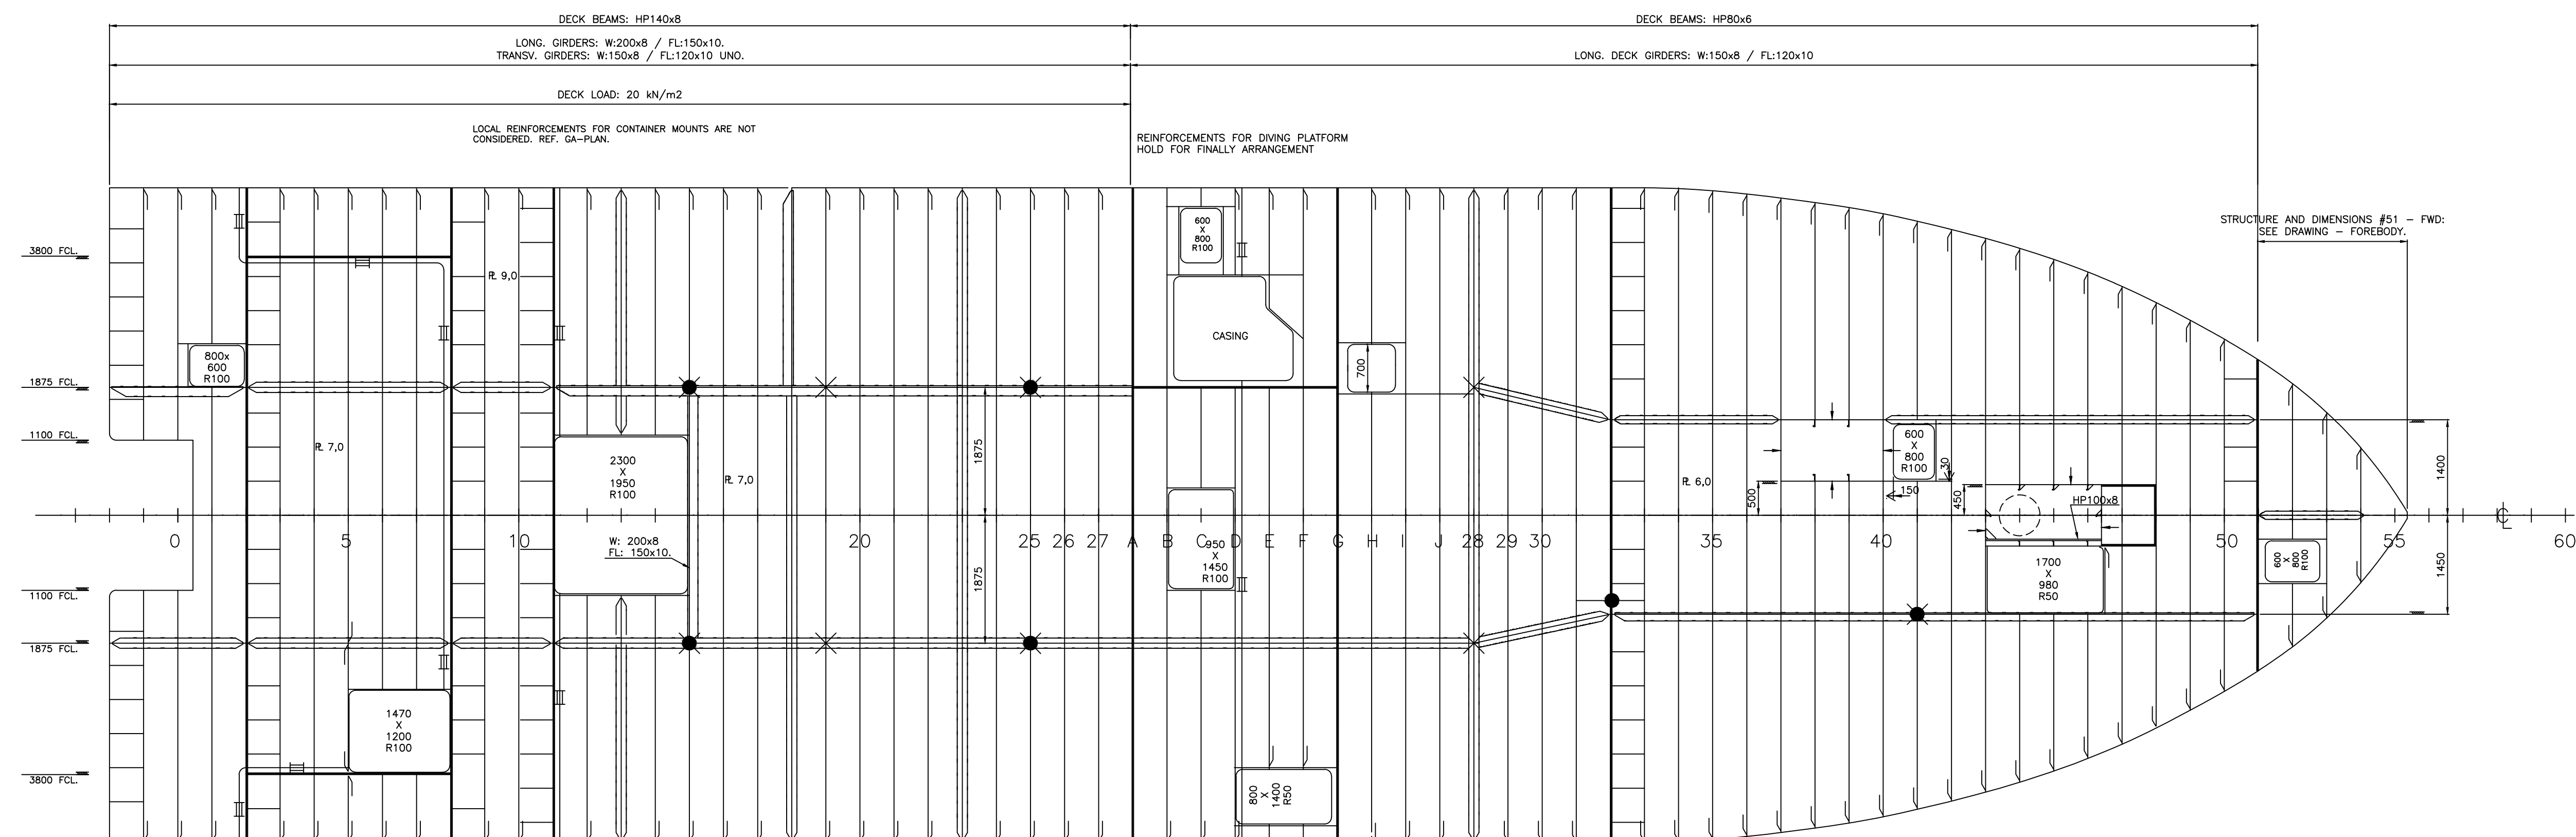


WHEELHOUSE TOP 11400 ABOVE BL

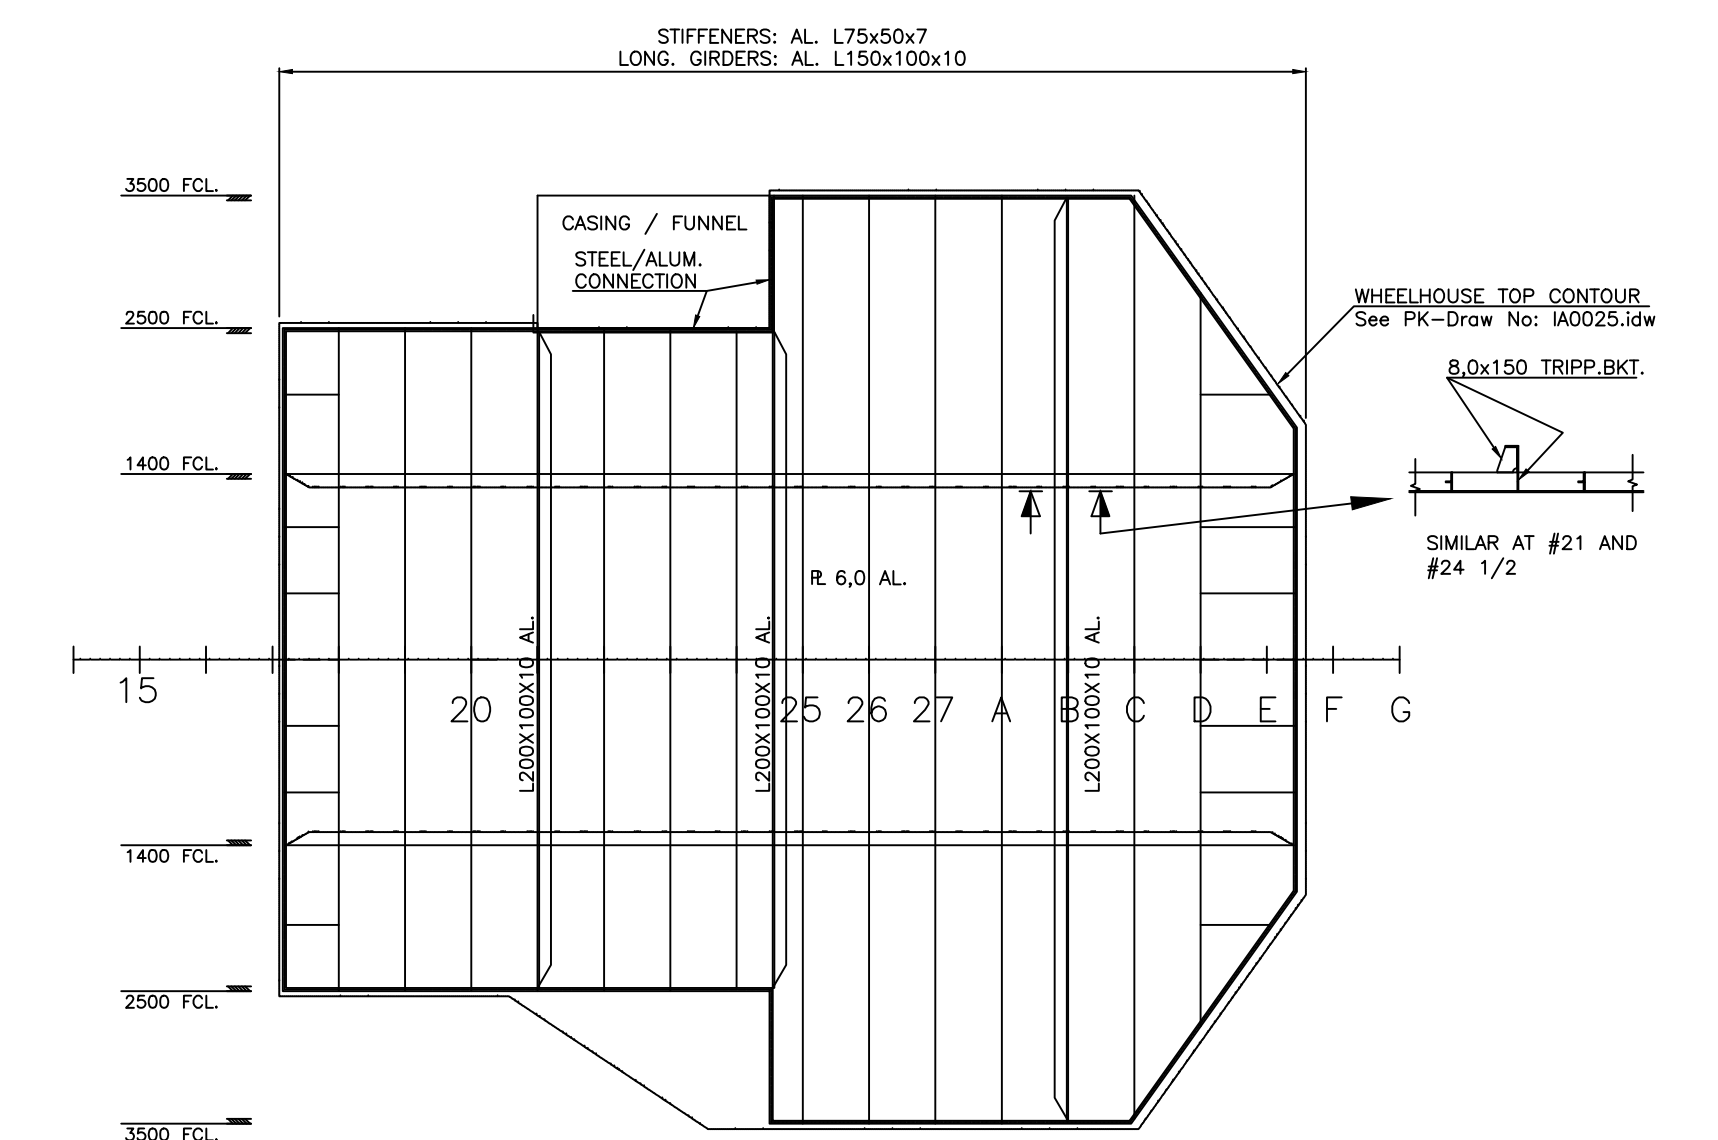


TANKTOP AND SINGLE BOTTOM

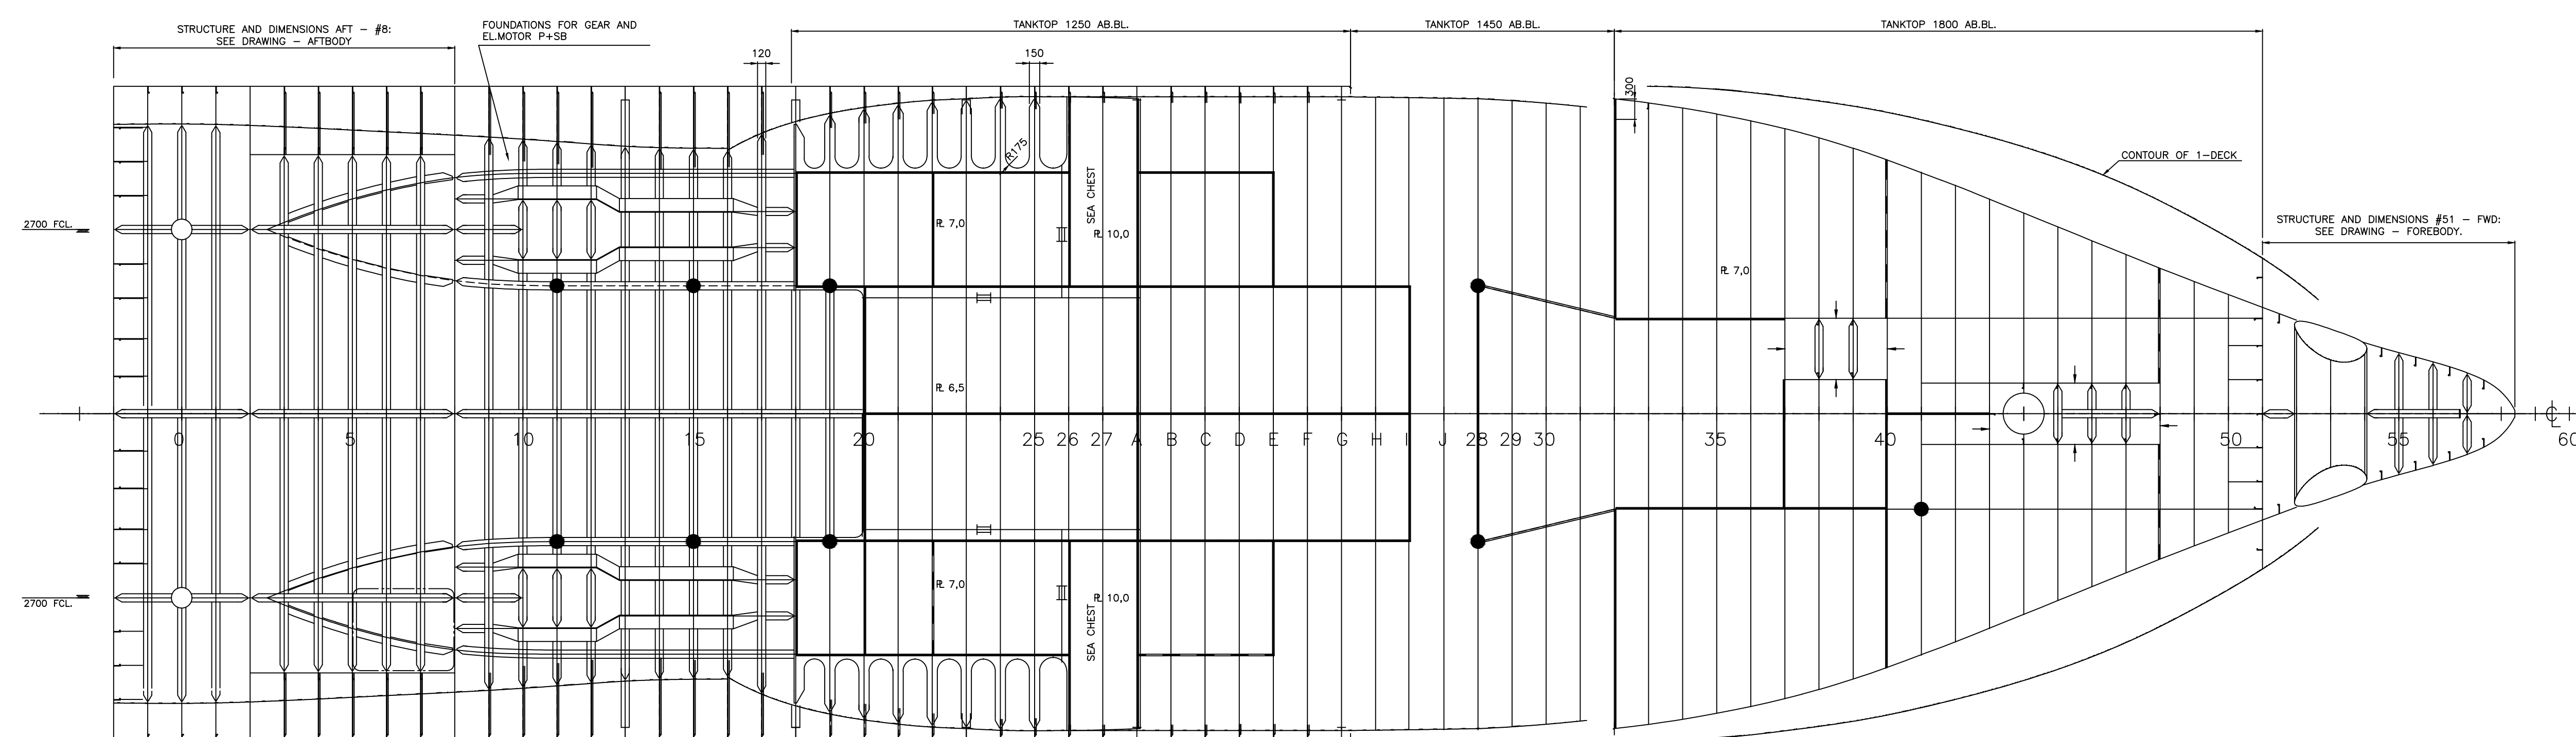

SUPERSTRUCTURE TOP 9000 ABOVE BL

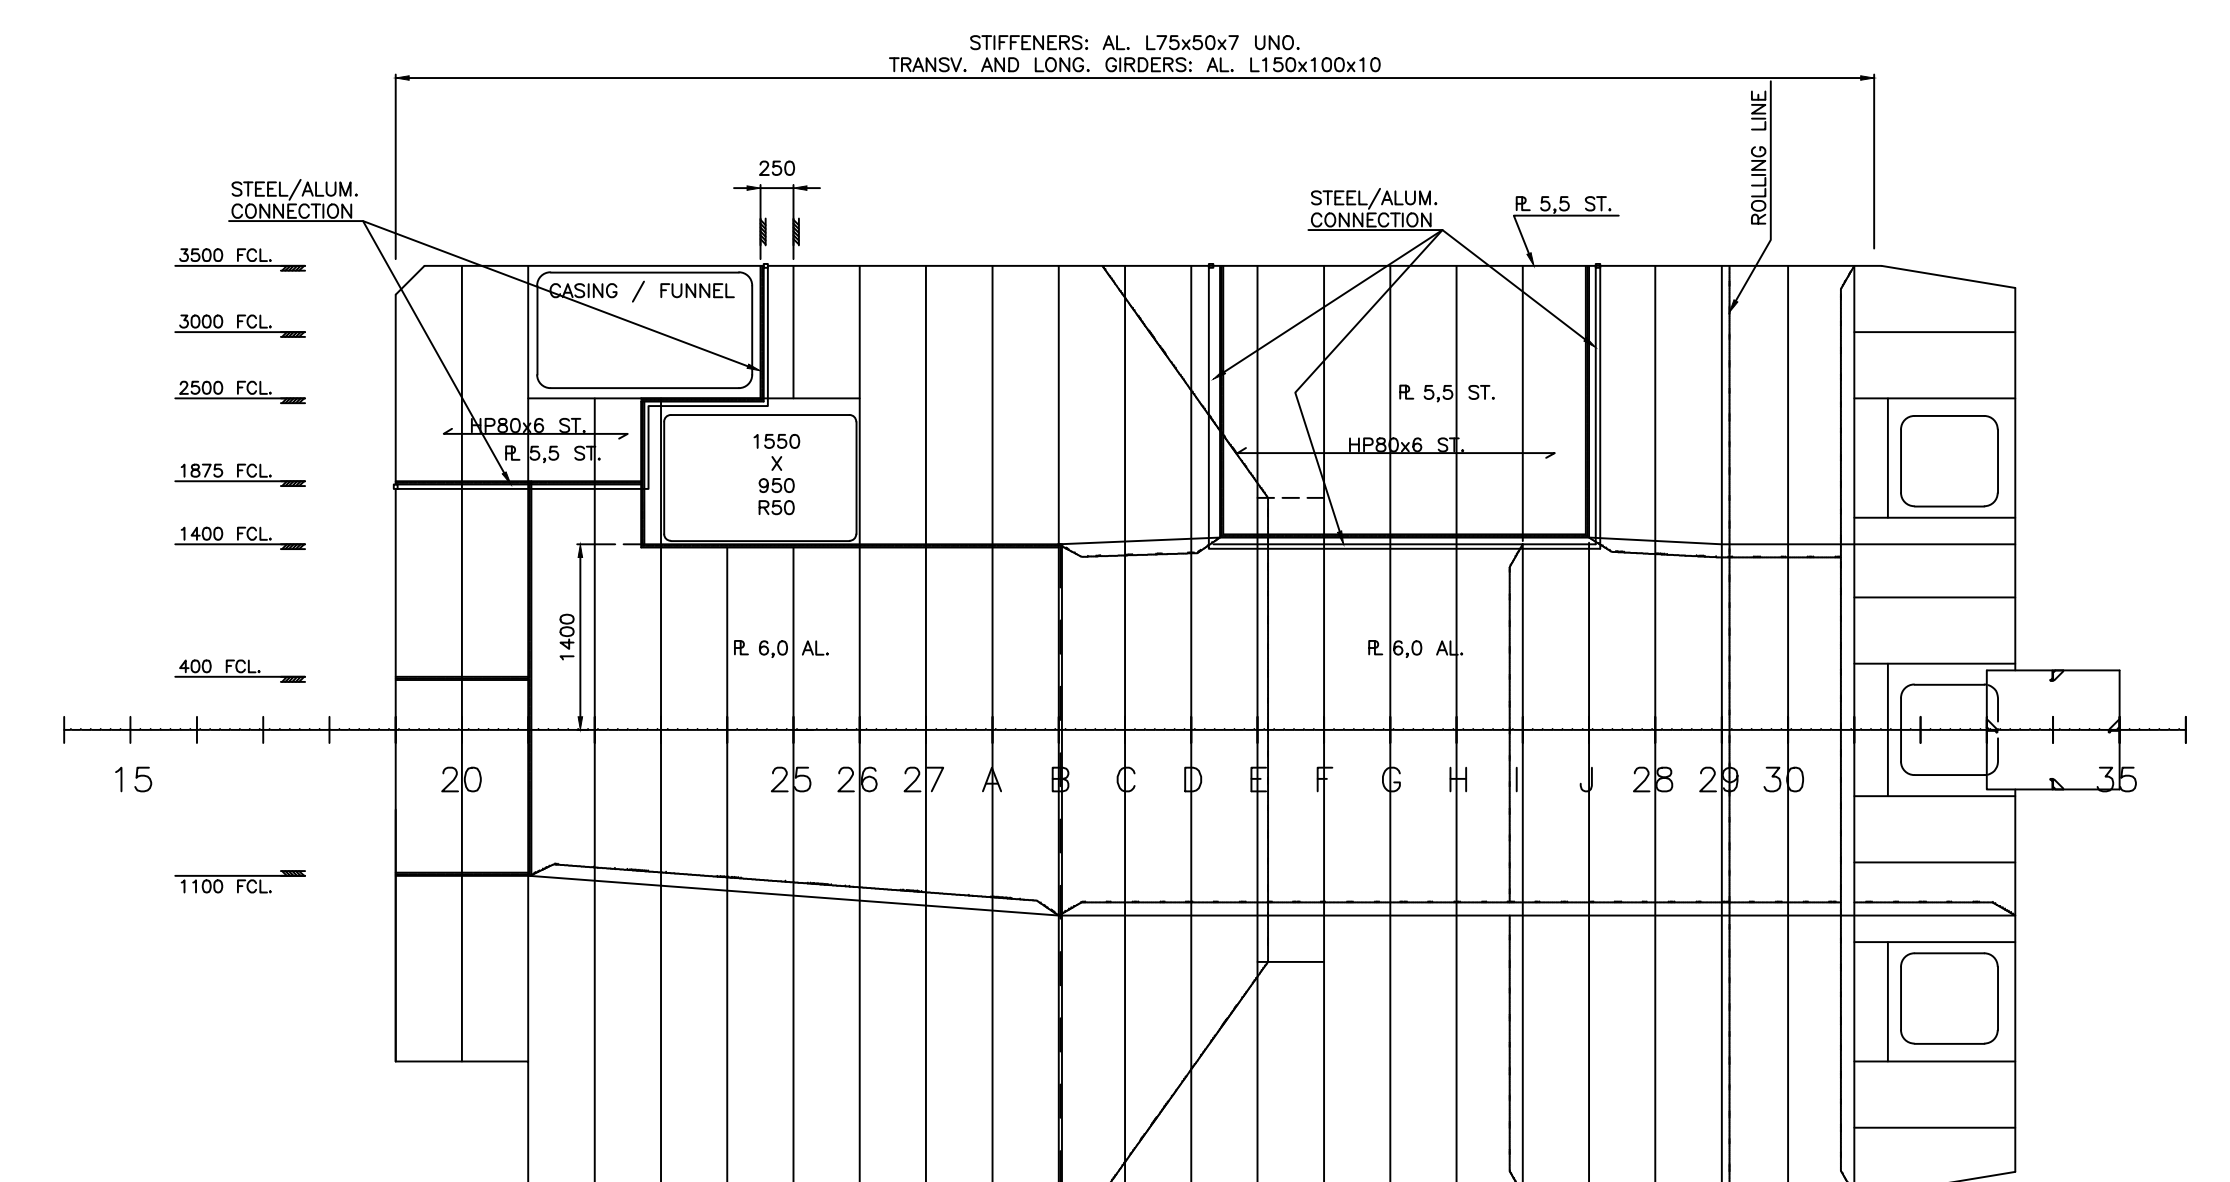

A-DECK 6600 ABOVE BL

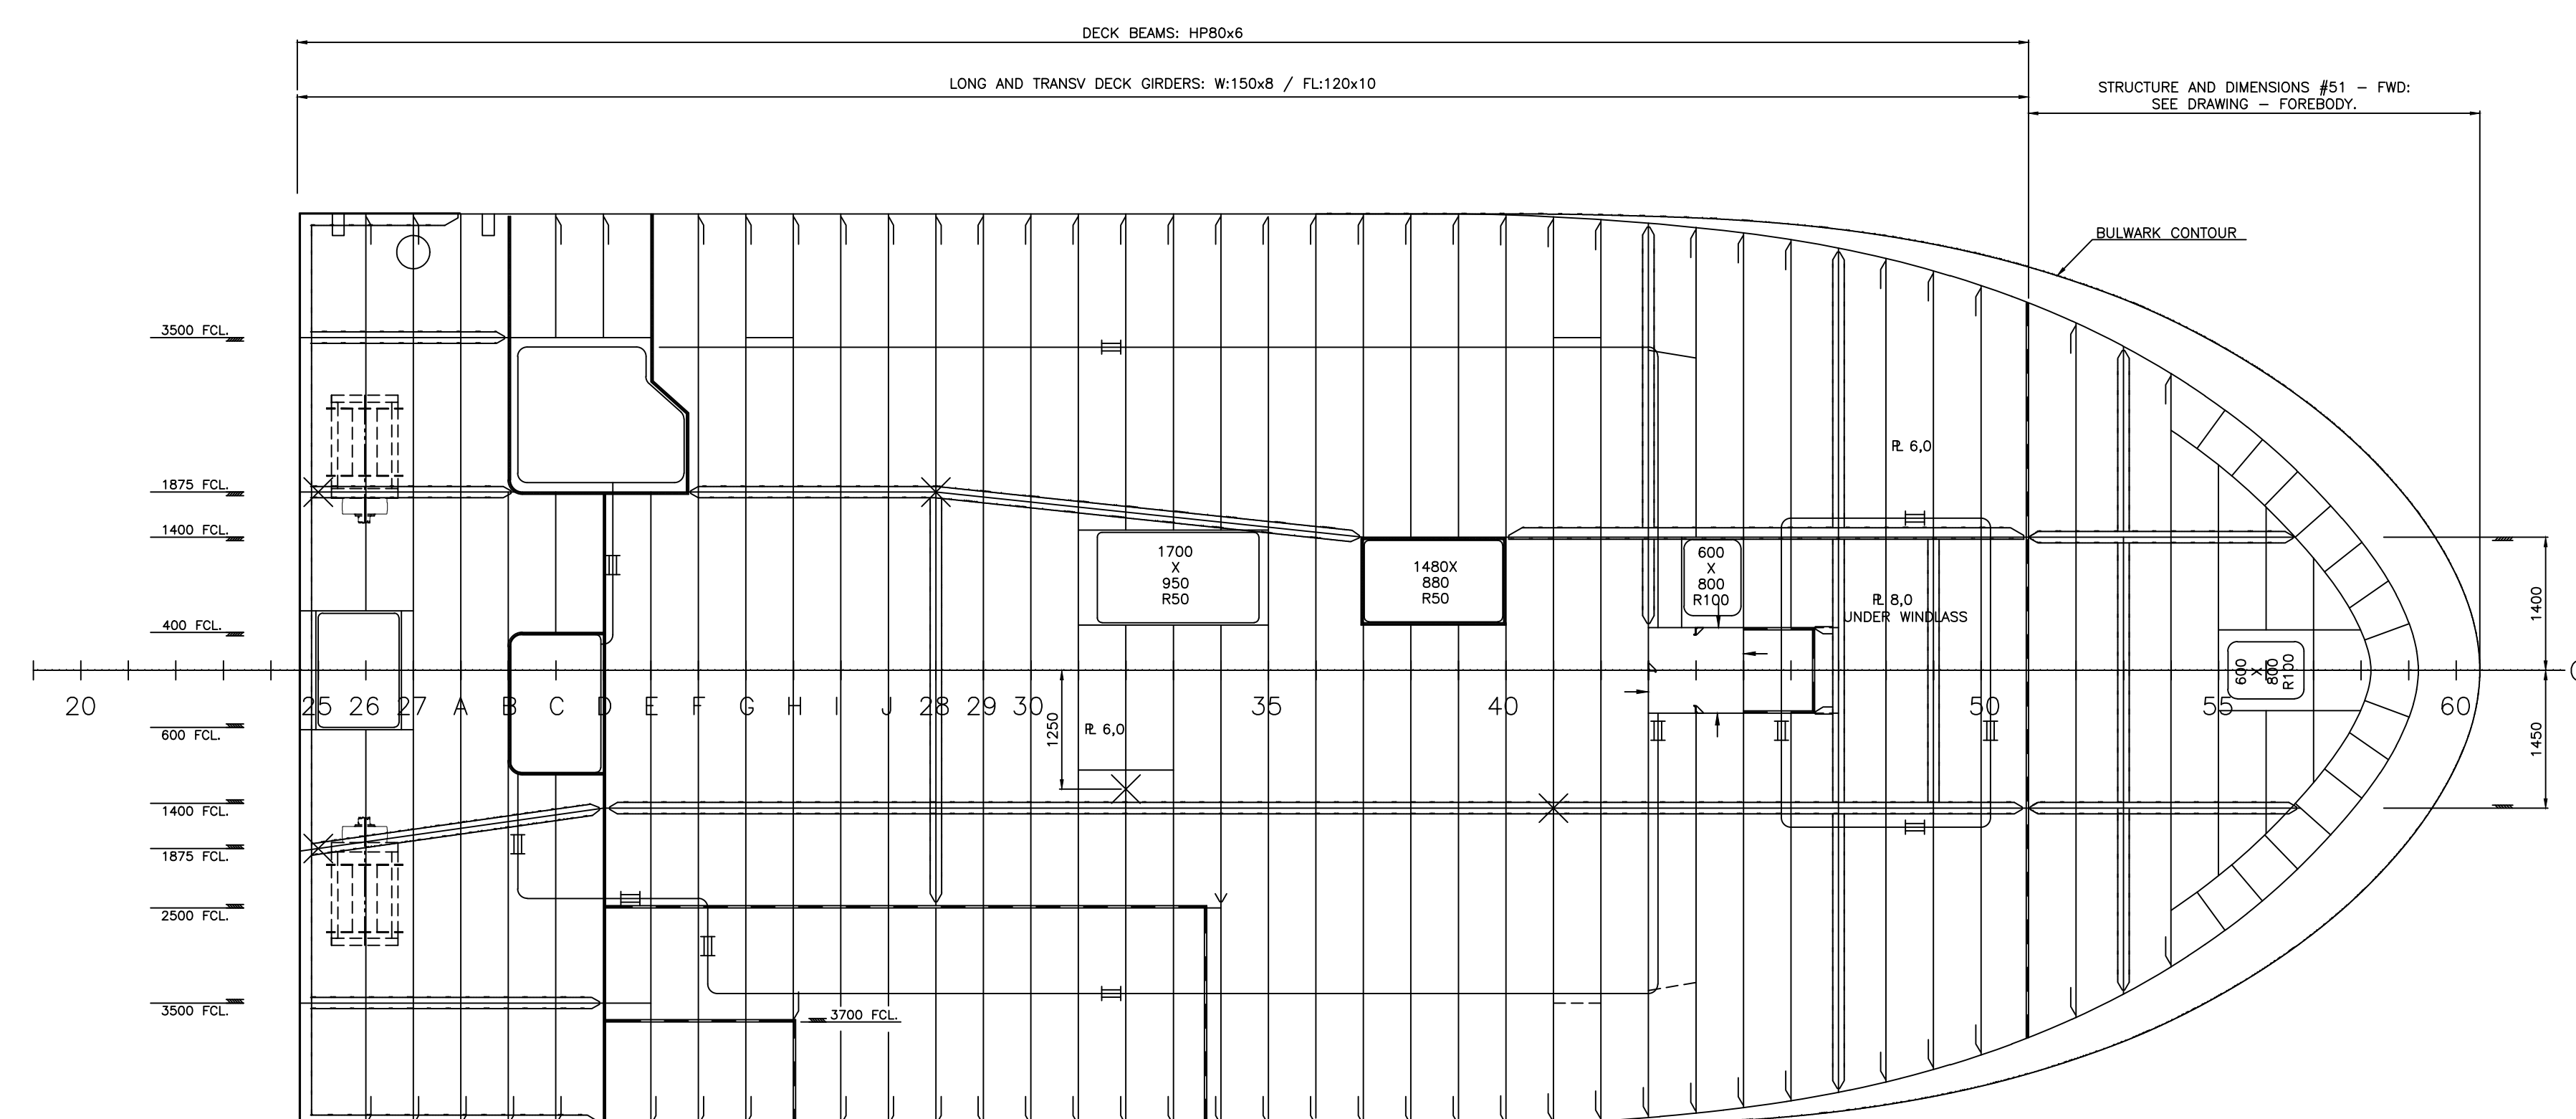

BASED ON DWG. CONSTRUCTION PLAN Rev0		DATE: 11/09/2026	
PROJECT: FF GUNNERUS -LNVZ- CONSTRUCTION PLAN DECK AND DOUBLE BOTTOM		SCALE: 1:50	SHEETS: 1/1

Open use for research/teaching and other non-commercial activities
Commercial use is not permitted without approval (CC BY-NC 4.0)



This drawing is a derivative work made by C-JOB and NTNU, based on the R/V Gunnerus open repository drawings, courtesy of Polarkonsult, published by NTNU. Licensed CC BY-NC 4.0.