

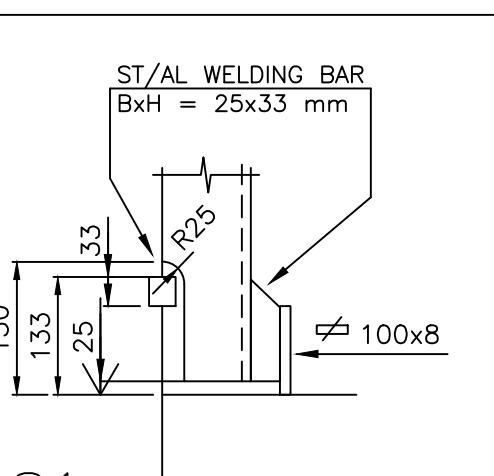



SECTION AT CENTRAL LINE

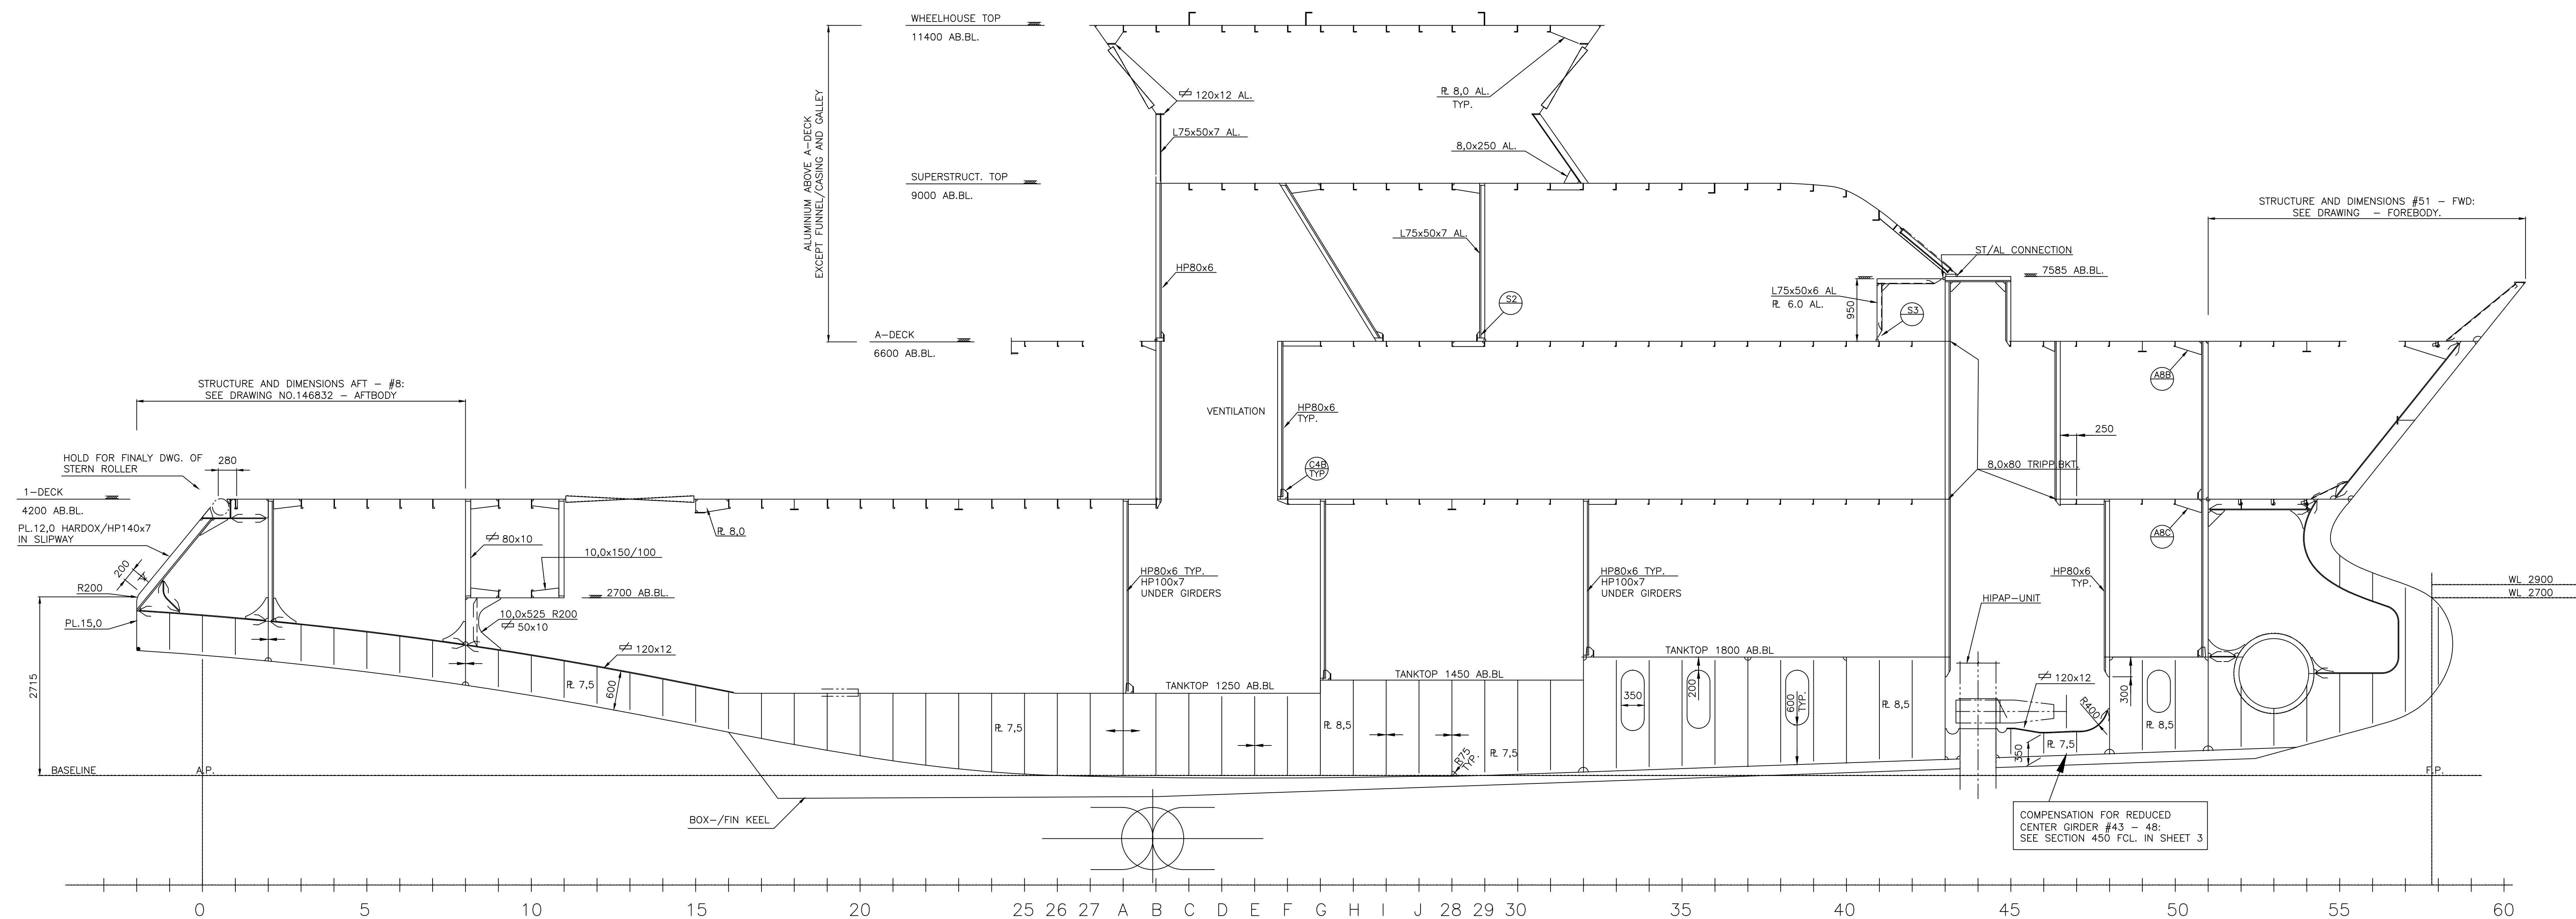


1

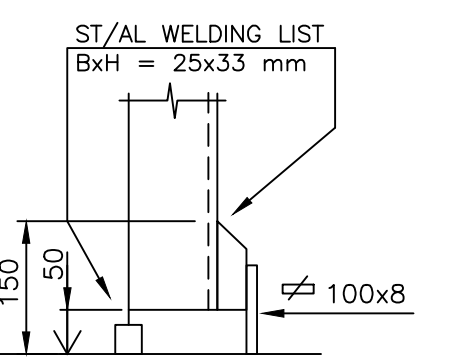

2

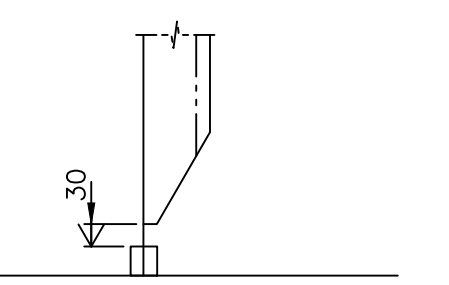


3

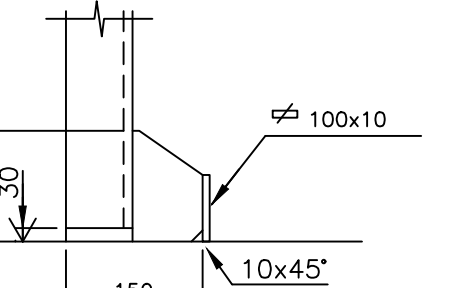

4

10	300
10	250
8	250
8	200
8	150
6	150

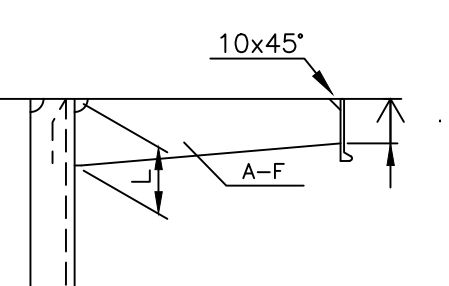

8

10	300
10	250
8	250
8	200
8	150
6	150

PROJECT: FF GUNNERUS - LNVZ - CONSTRUCTION PLAN LONGITUDINAL SECTION		SCALE: 1:50	SHEETS: 1/1
--	--	----------------	----------------

Open use for research/teaching and other non-commercial activities
Commercial use is not permitted without approval (CC BY-NC 4.0)



This drawing is a derivative work made by C-JOB and NTNU, based on the R/V Gunnerus open repository drawings, courtesy of Polarkonsult, published by NTNU. Licensed CC BY-NC 4.0.