


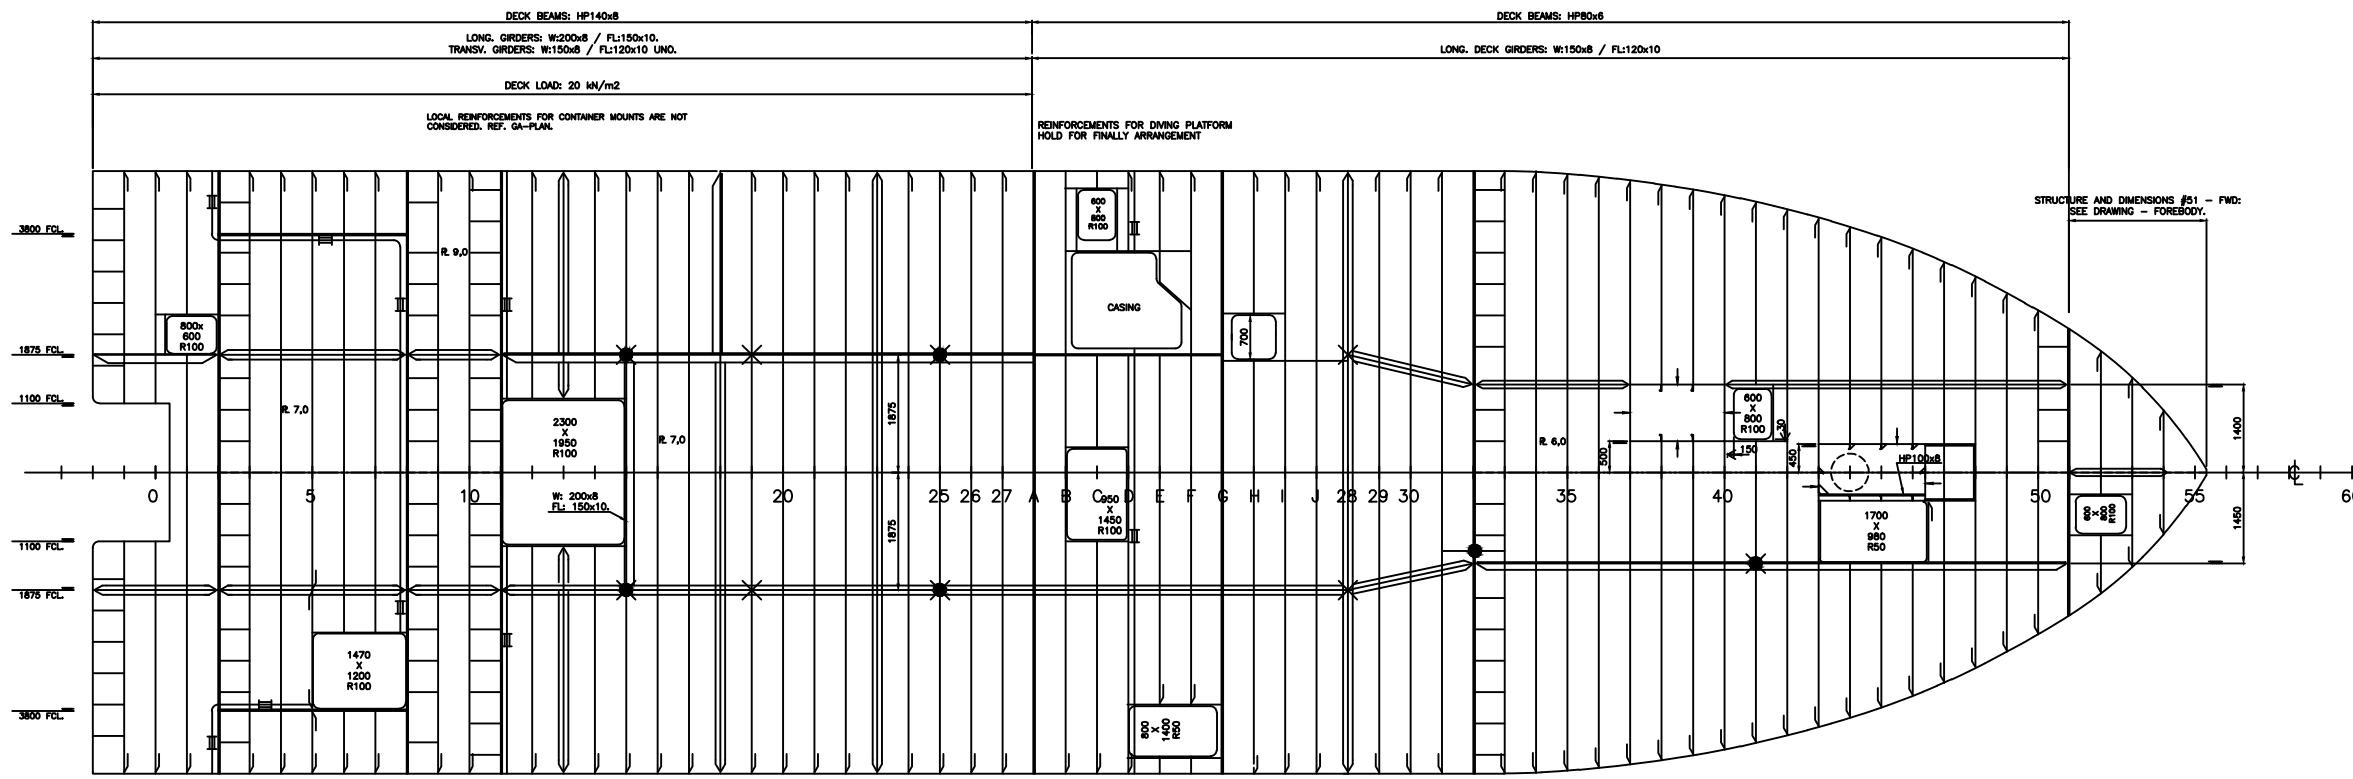
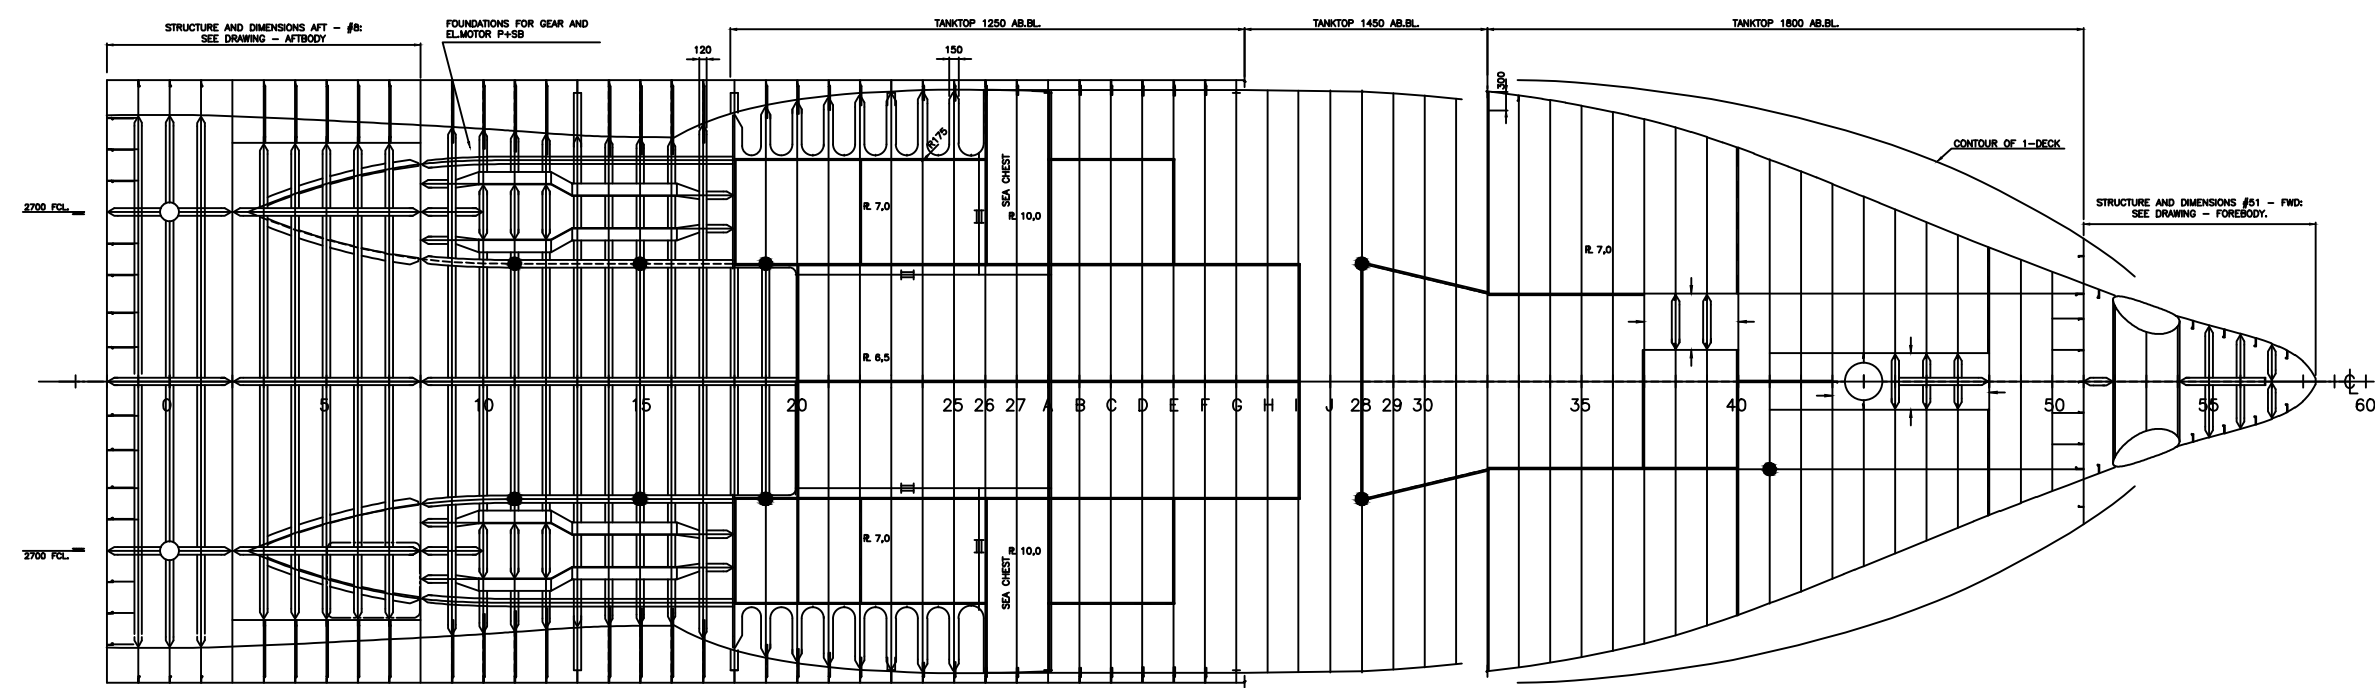
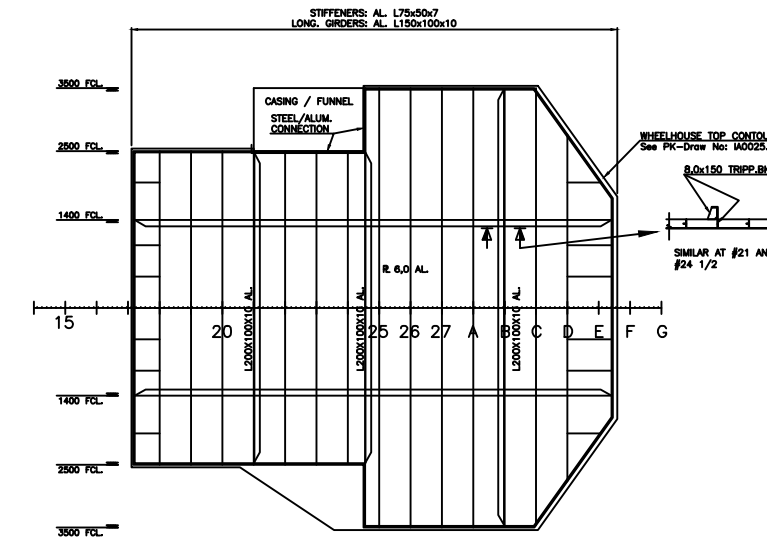


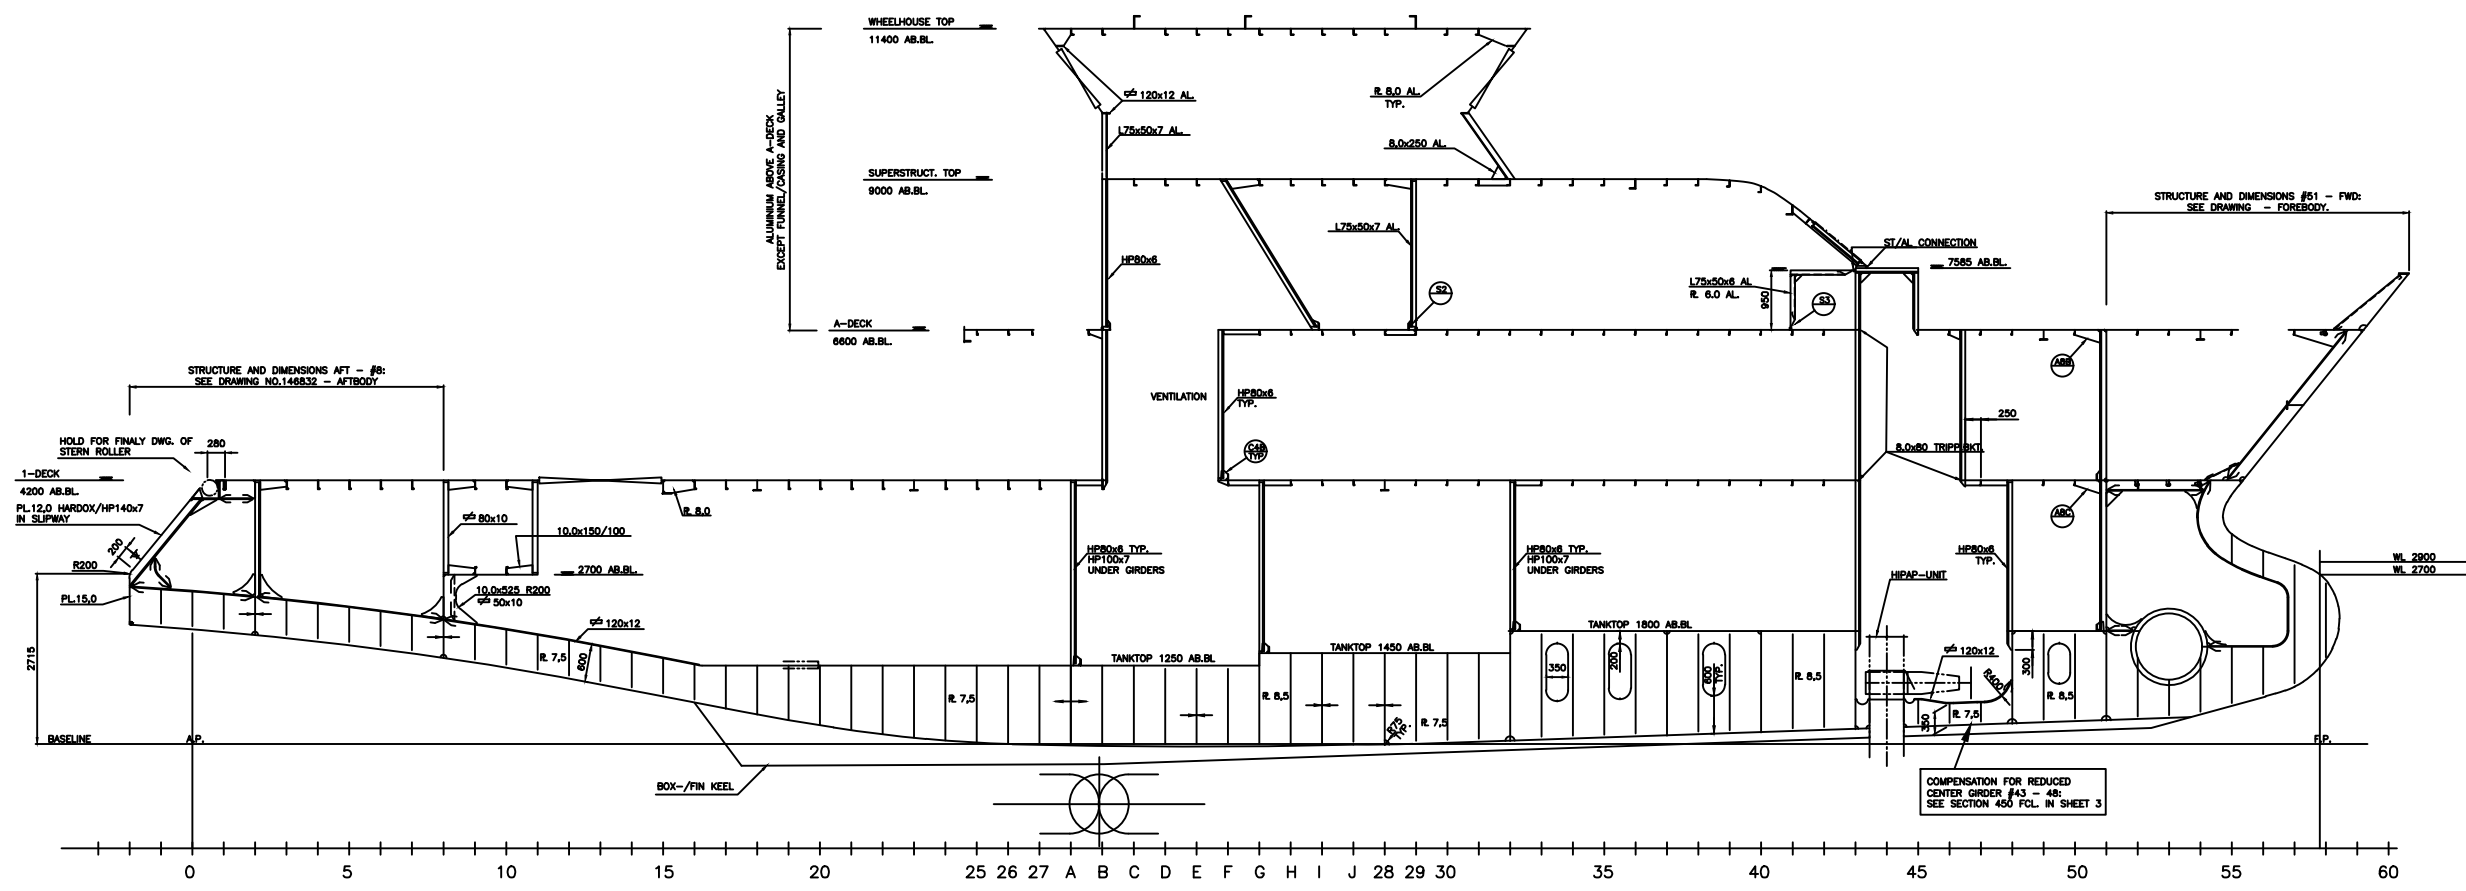



1-DECK 4000 AB.B.

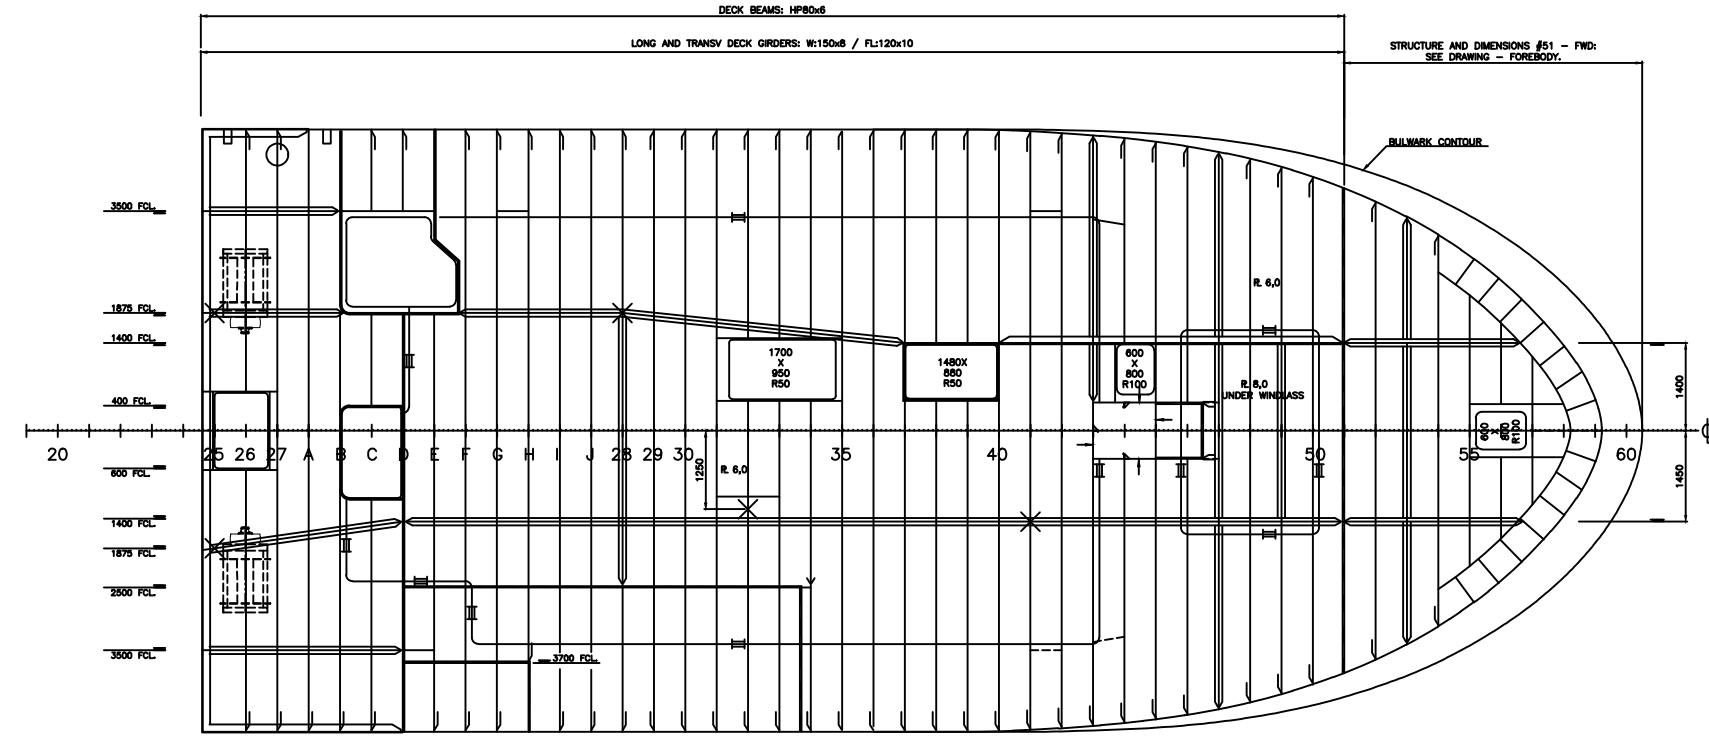



WHEELHOUSE TOP 11400 AB.B.

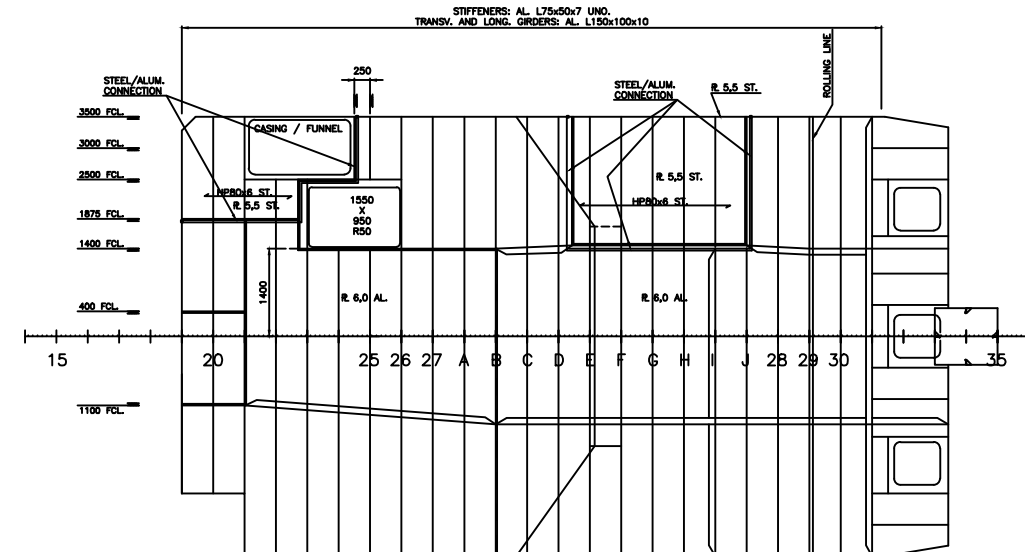


WHEELHOUSE FLOOR / SUPERSTRUCTURE TOP 8000 AB.B.

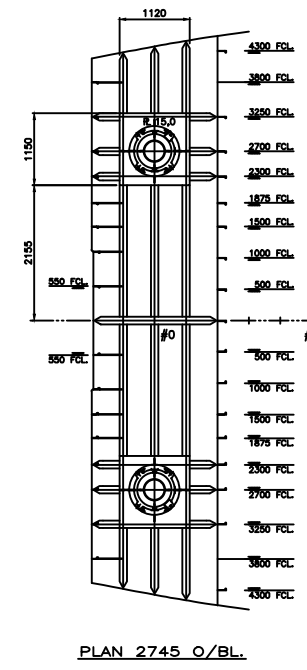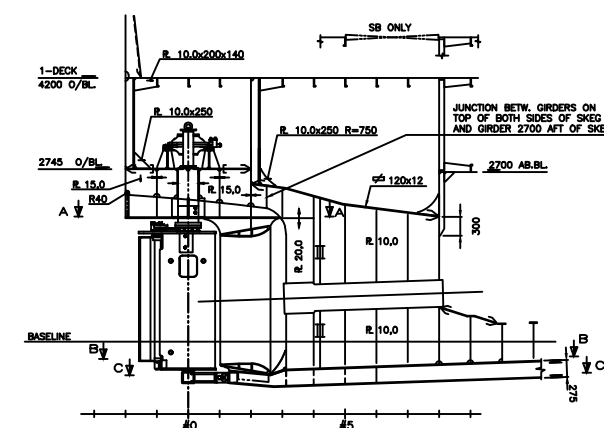

PLAN 2145 OUTLINE

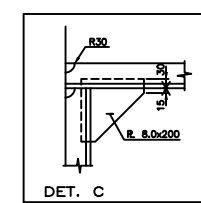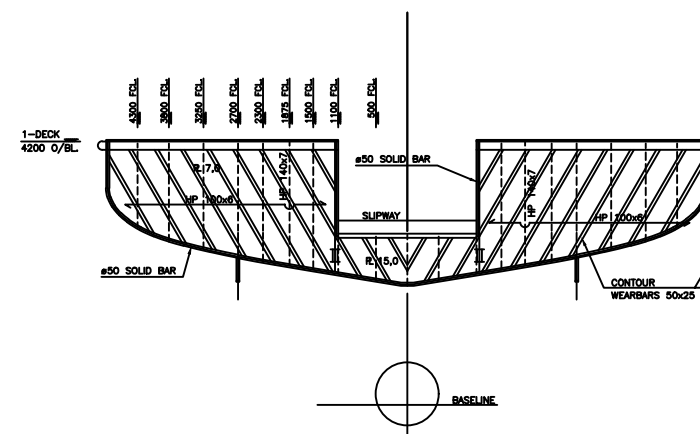

DET. C

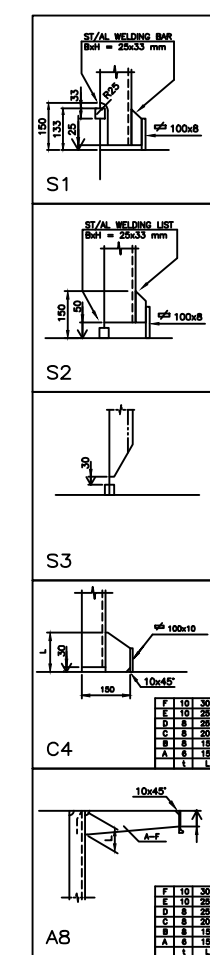



S1

S2



S3

C4



AB

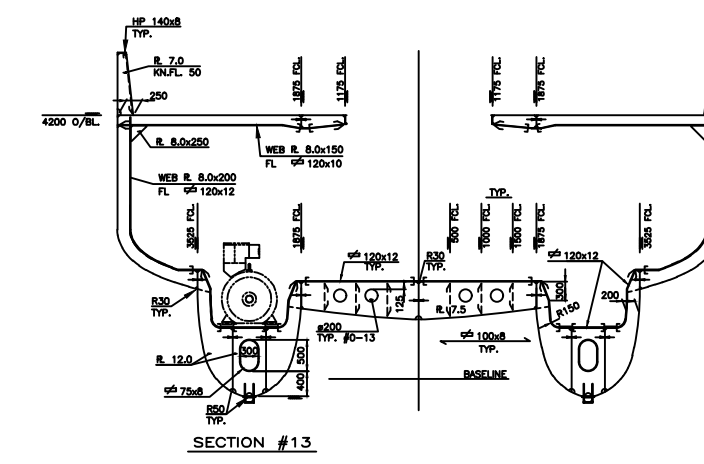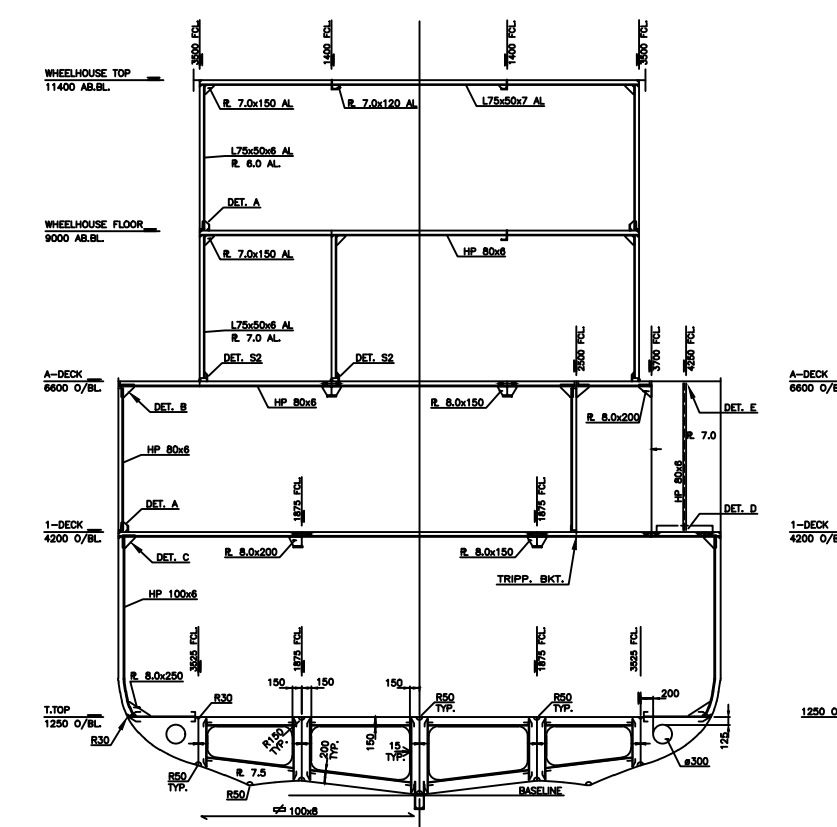

SECTION #13

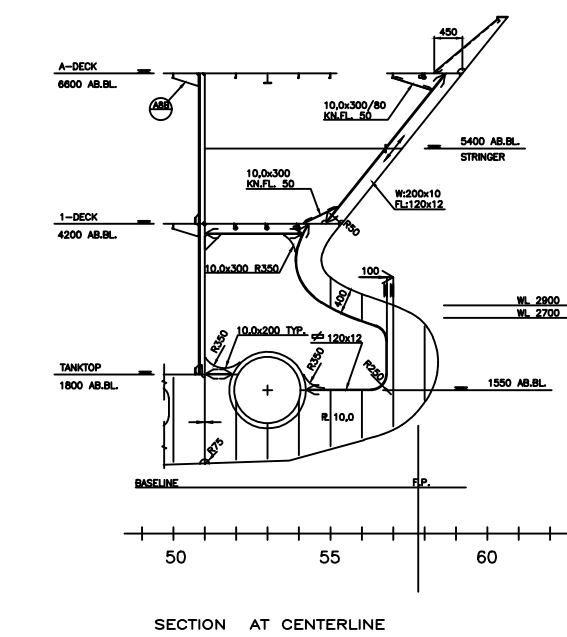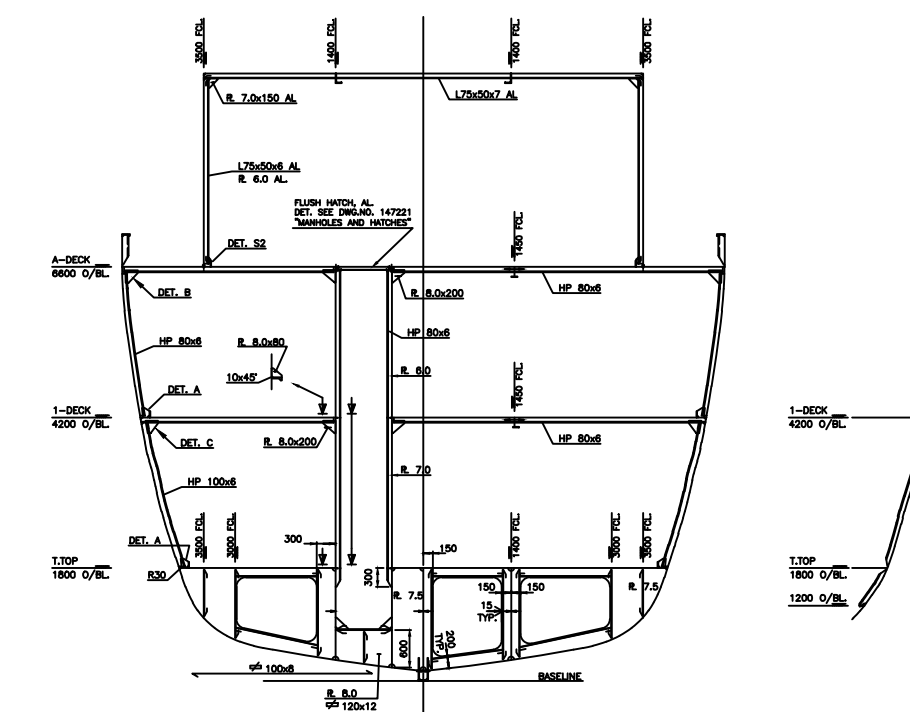

SECTION AT CENTERLINE

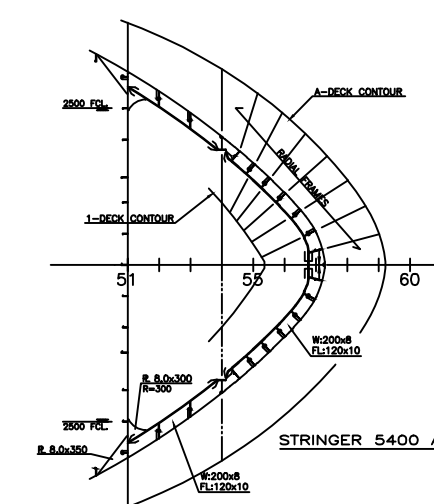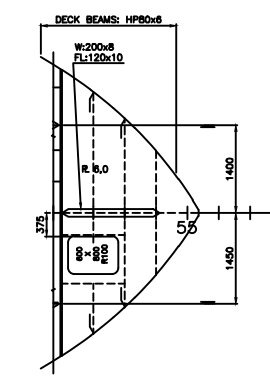

STRONGER 3400 AB.B.

