

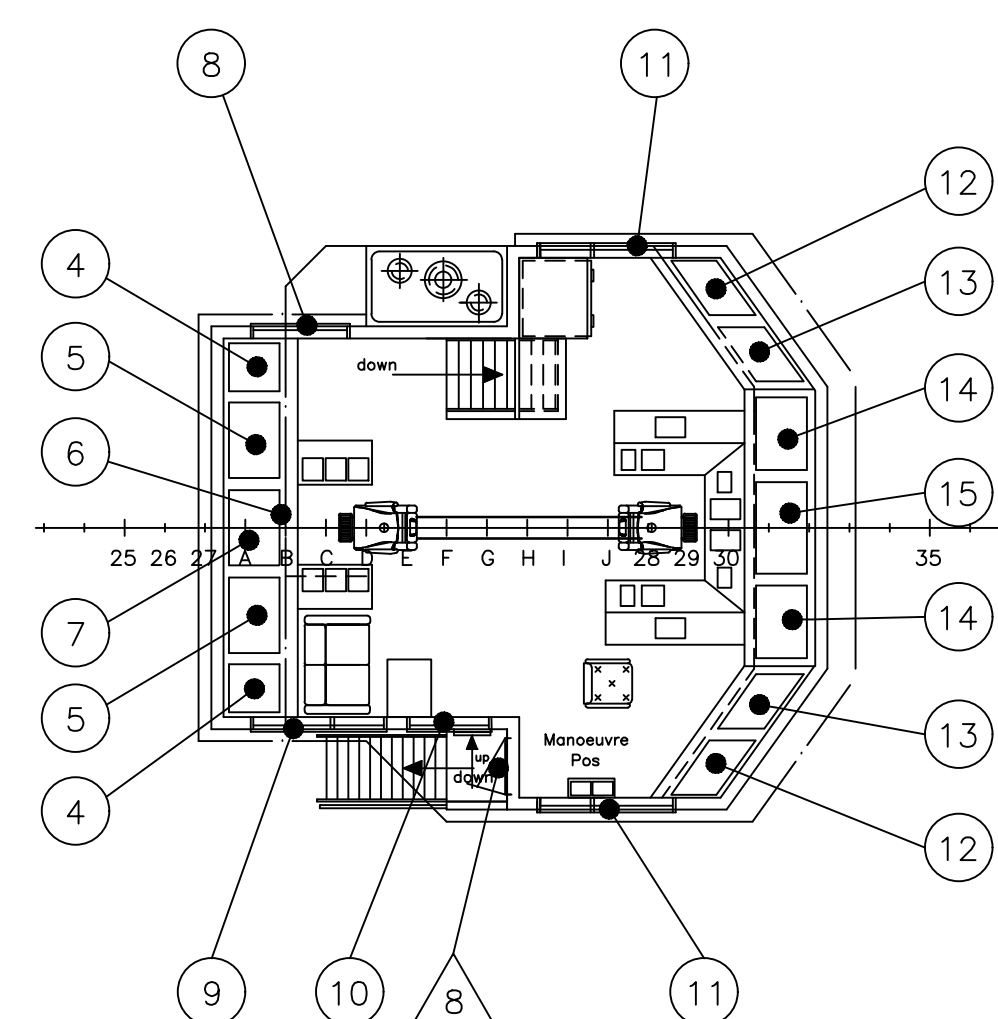



## PROFILE

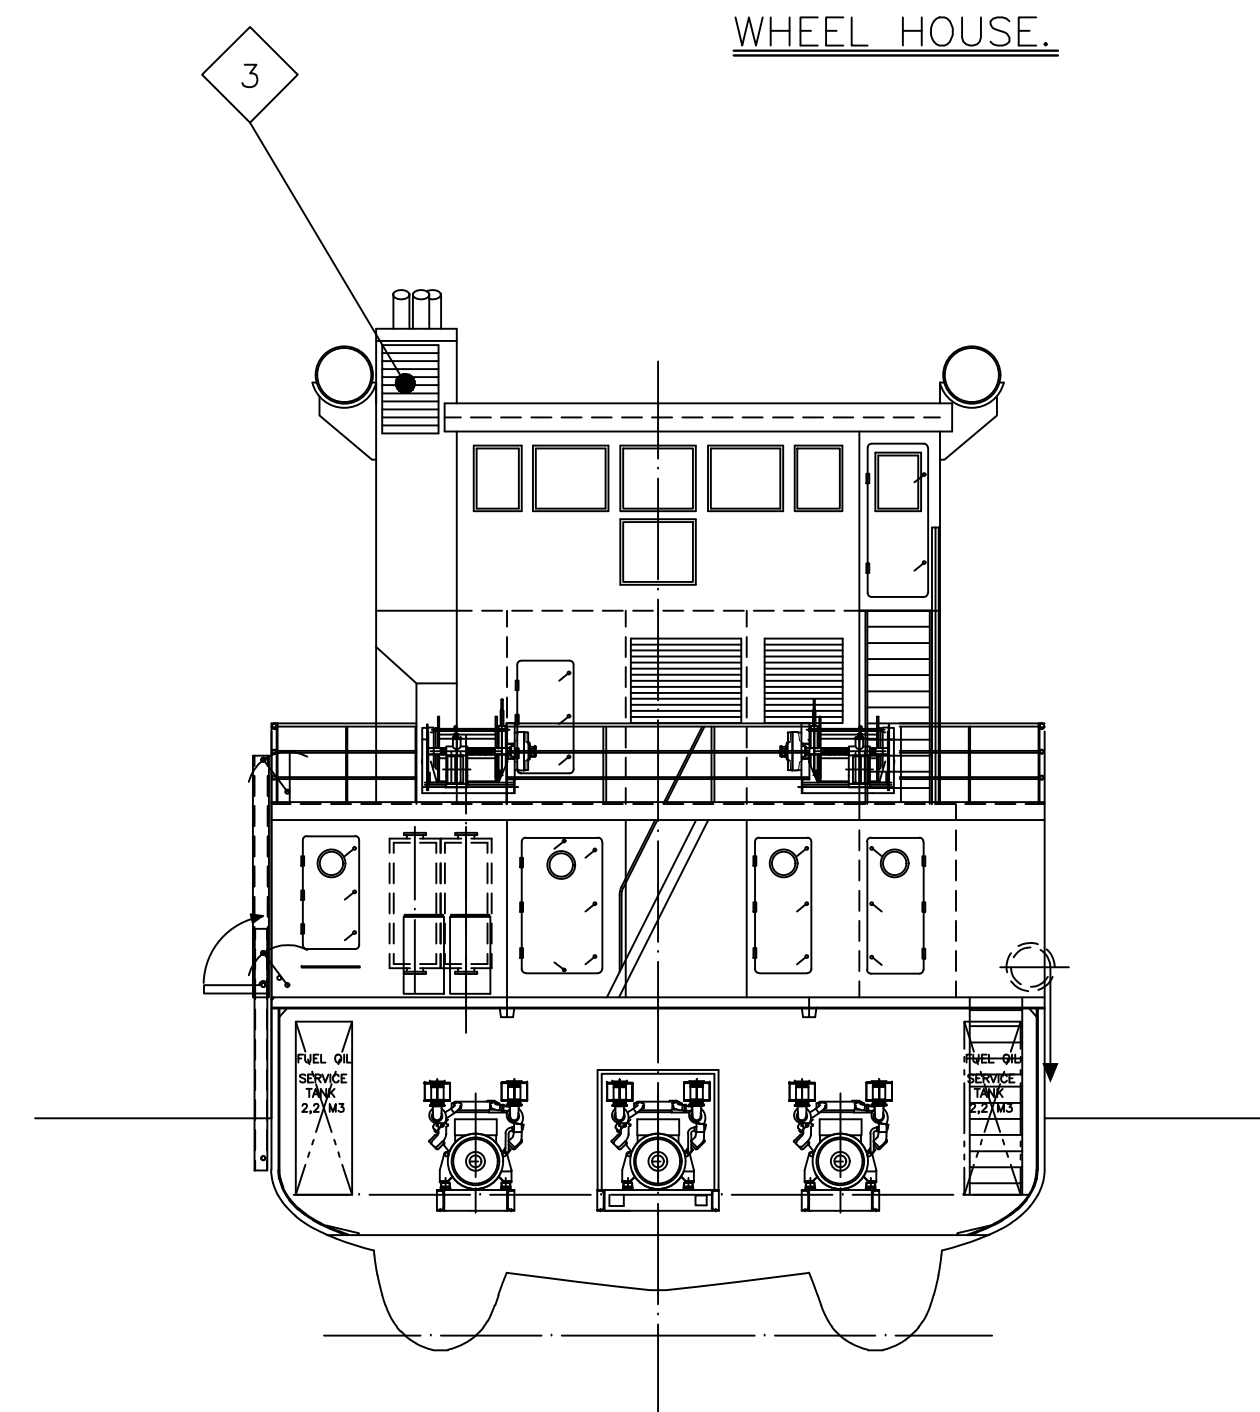


WHEEL HOUSE.

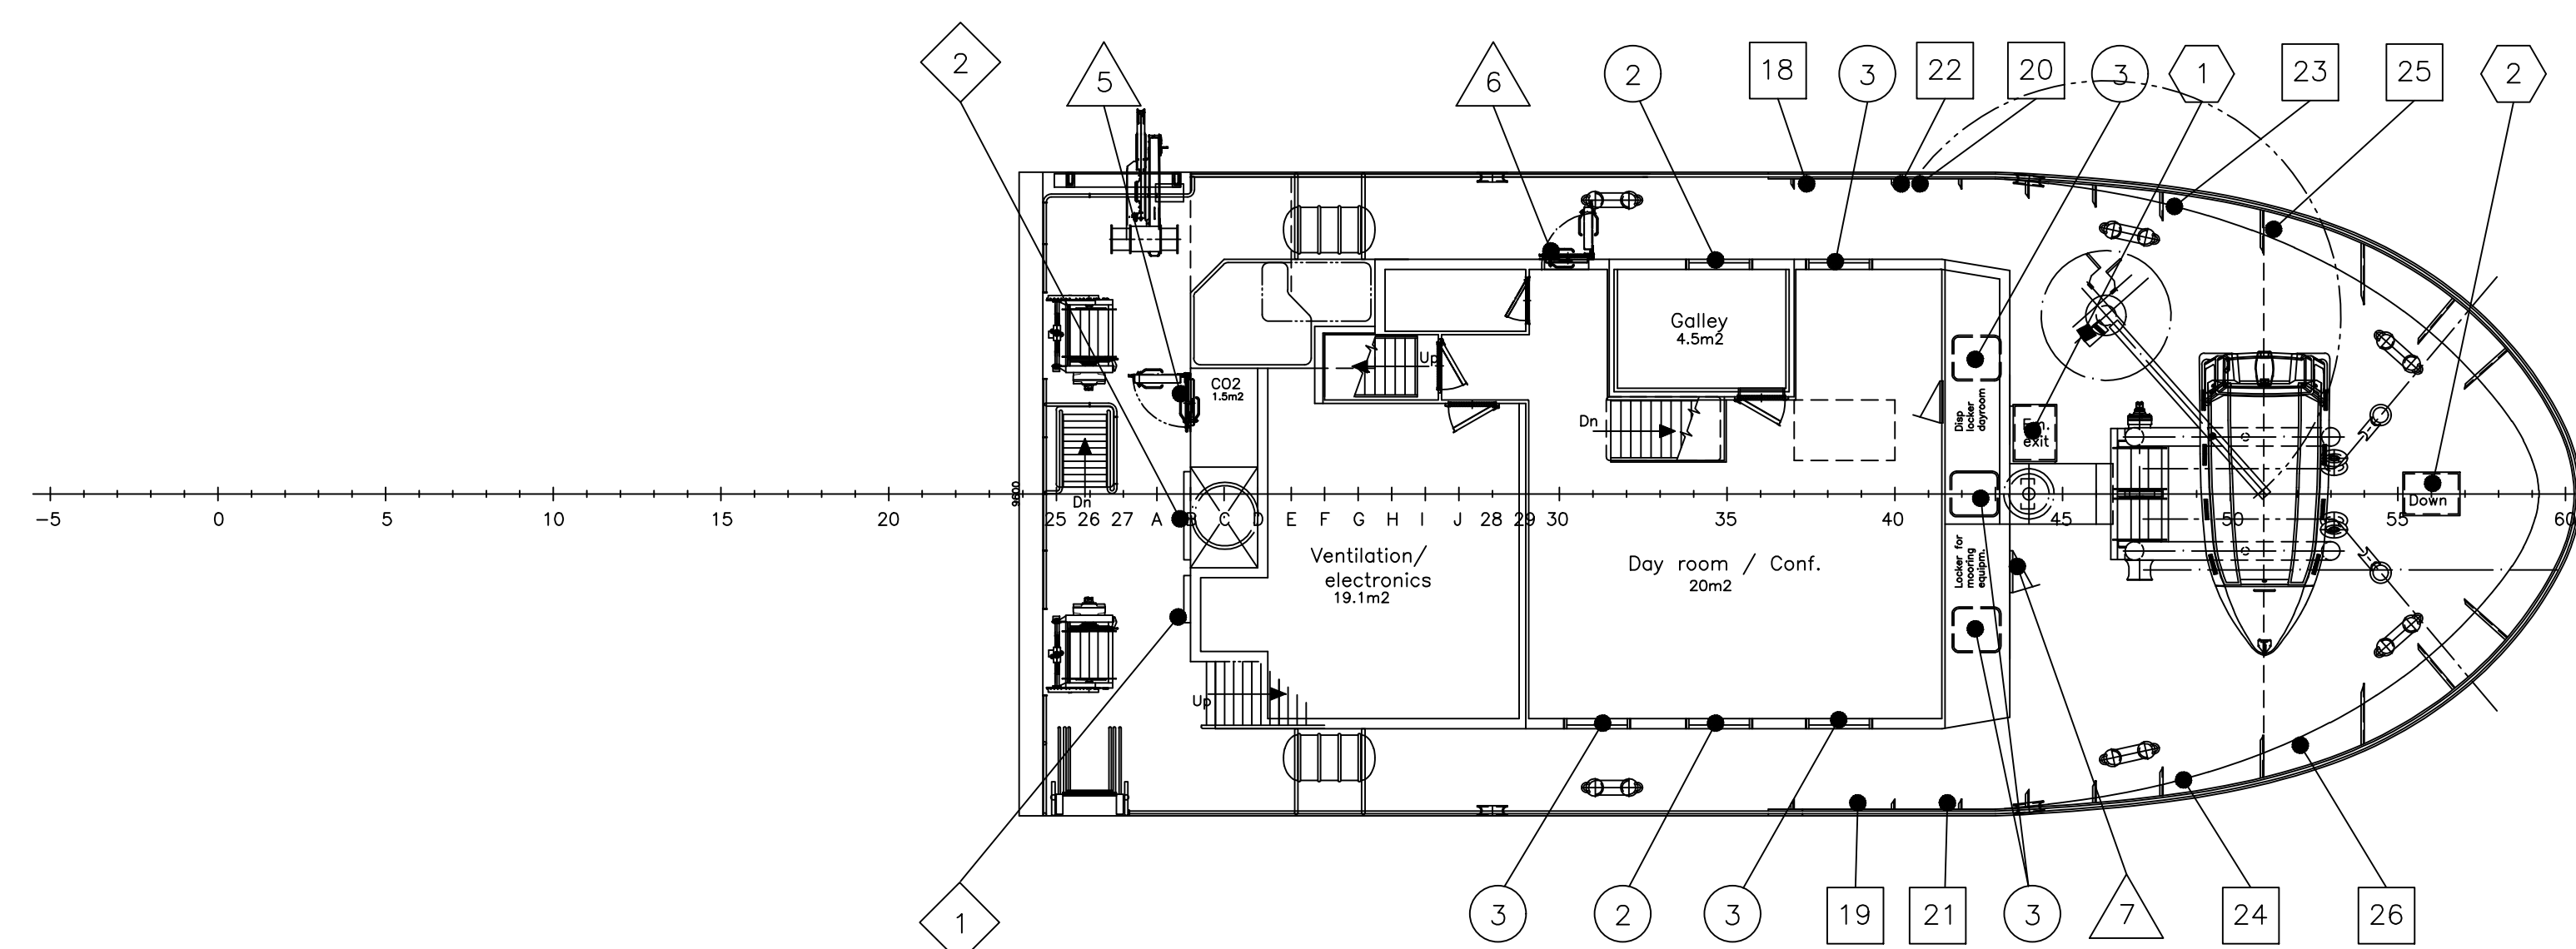


SECTION FR.17

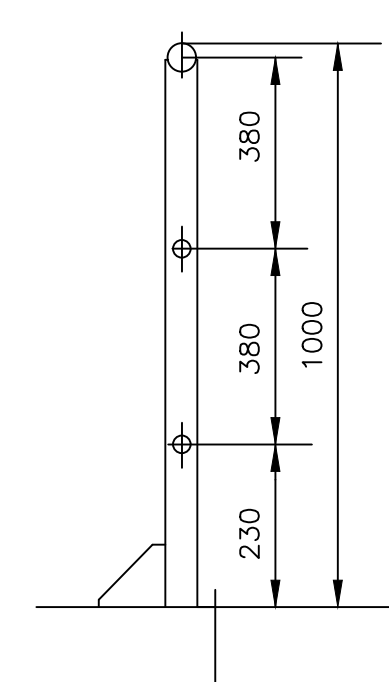

TYPICAL SECTION  
GUARDRAILS ON DECK.

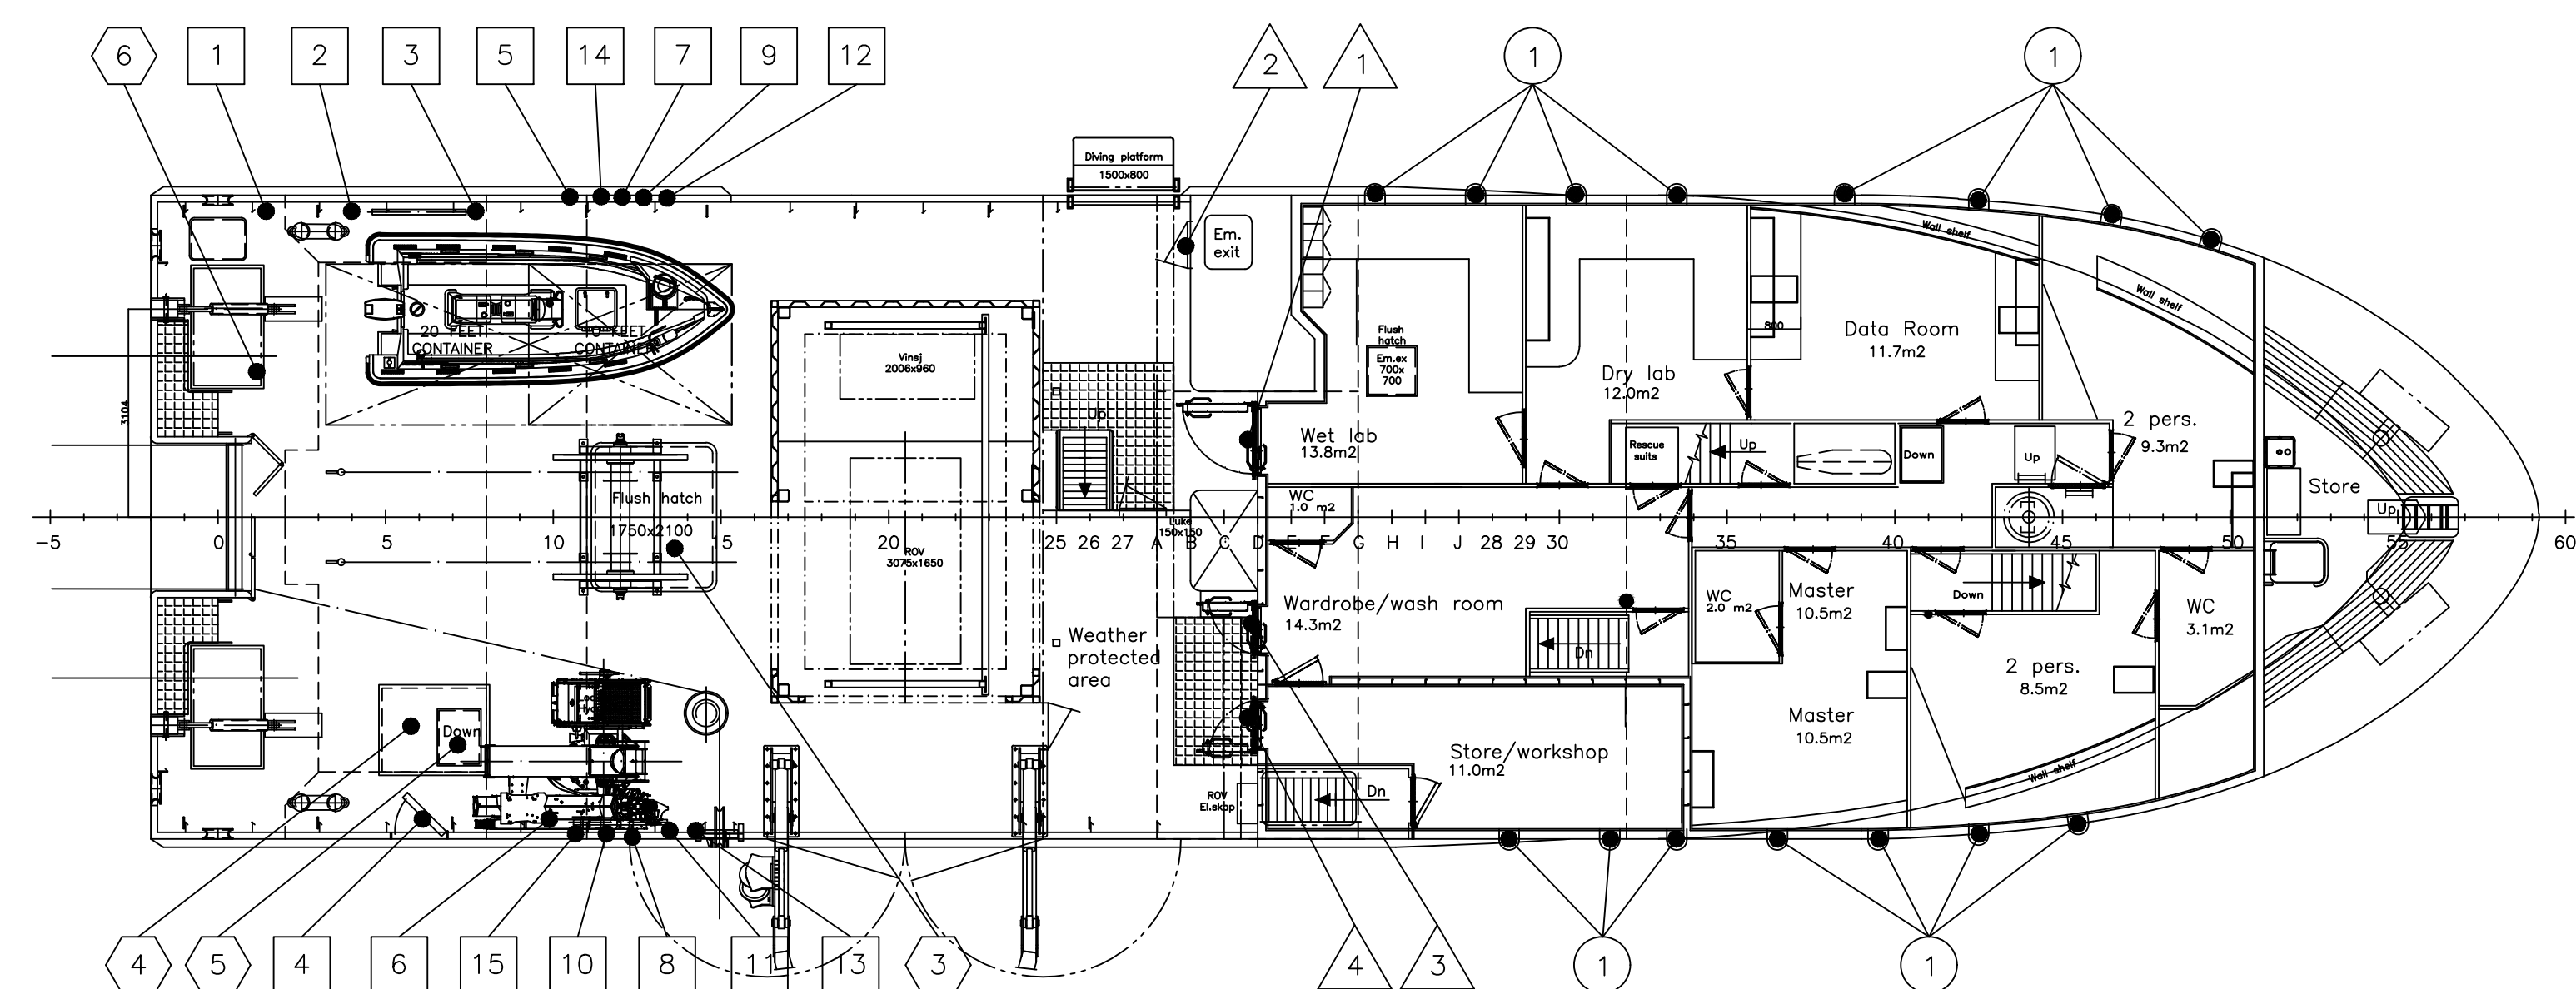

1-DECK

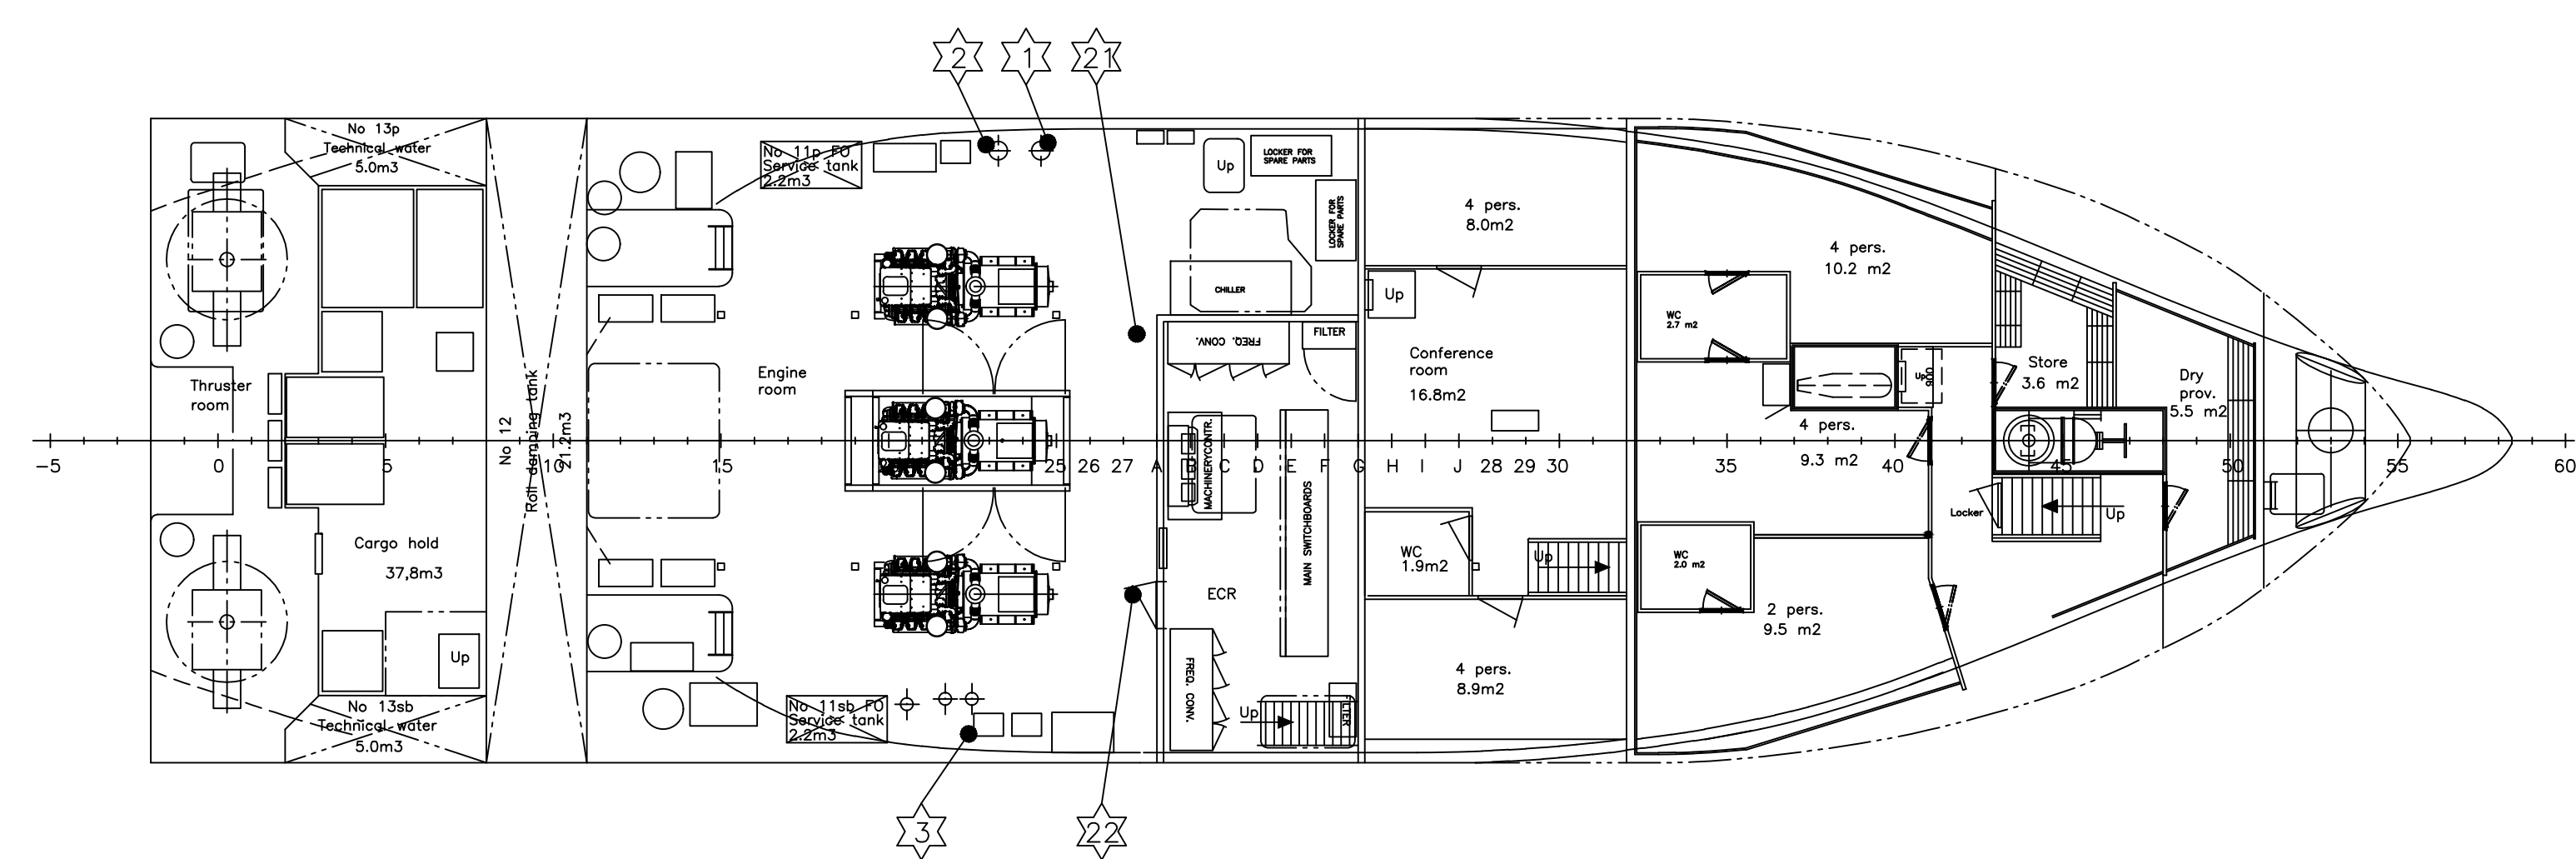


BELOW 1-DECK

| AIR-PIPES  |                |            |                      |       |                         |                       |
|-----------------------------------------------------------------------------------------------|----------------|------------|----------------------|-------|-------------------------|-----------------------|
| POS.                                                                                          | FROM           | TO         | HEIGHT<br>ABOVE DECK | MATR. | DIMENSION<br>ABOVE DECK | TYPE CLOSING          |
| 1                                                                                             | ST. GEAR HOLD  | 1-DECK     | 760                  | ST.   | 88,9x7,1                | TANK VENT CHECK VALVE |
| 2                                                                                             | CARGO HOLD     | 1-DECK     | 760                  | ST.   | 88,9x7,1                | TANK VENT CHECK VALVE |
| 3                                                                                             | TANK NO. 13 p  | 1-DECK     | 760                  | ST.   | 76,1x6,3                | TANK VENT CHECK VALVE |
| 4                                                                                             | TANK NO. 13 sb | 1-DECK     | 760                  | ST.   | 76,1x6,3                | TANK VENT CHECK VALVE |
| 5                                                                                             | TANK NO. 12 p  | 1-DECK     | 760                  | ST.   | 76,1x6,3                | TANK VENT CHECK VALVE |
| 6                                                                                             | TANK NO. 12 sb | 1-DECK     | 760                  | ST.   | 76,1x6,3                | TANK VENT CHECK VALVE |
| 7                                                                                             | SEACHEST PORT  | 1-DECK     | 760                  | ST.   | 88,9x7,1                | SWAN NECK             |
| 8                                                                                             | SEACHEST SB    | 1-DECK     | 760                  | ST.   | 88,9x7,1                | SWAN NECK             |
| 9                                                                                             | TANK NO. 10    | 1-DECK     | 760                  | ST.   | 88,9x7,1                | TANK VENT CHECK VALVE |
| 10                                                                                            | TANK NO. 9     | 1-DECK     | 760                  | ST.   | 60,3x6,3                | TANK VENT CHECK VALVE |
| 11                                                                                            | TANK NO. 8     | 1-DECK     | 760                  | ST.   | 60,3x6,3                | TANK VENT CHECK VALVE |
| 12                                                                                            | TANK NO. 11 p  | 1-DECK     | 760                  | ST.   | 60,3x6,3                | TANK VENT CHECK VALVE |
| 13                                                                                            | TANK NO. 11 sb | 1-DECK     | 760                  | ST.   | 60,3x6,3                | TANK VENT CHECK VALVE |
| 14                                                                                            | TANK NO. 6 p   | 1-DECK     | 760                  | ST.   | 76,1x6,3                | TANK VENT CHECK VALVE |
| 15                                                                                            | TANK NO. 6 sb  | 1-DECK     | 760                  | ST.   | 76,1x6,3                | TANK VENT CHECK VALVE |
| 16                                                                                            | TANK NO. 7 p   | TOP FUNNEL | 5200                 | ST.   | 88,9x7,1                | SWAN NECK             |
| 17                                                                                            | TANK NO. 7 sb  | TOP FUNNEL | 5200                 | ST.   | 88,9x7,1                | SWAN NECK             |
| 18                                                                                            | TANK NO. 5     | A-DECK     | 450                  | ST.   | 76,1x6,3                | TANK VENT CHECK VALVE |
| 19                                                                                            | TANK NO. 4     | A-DECK     | 450                  | ST.   | 76,1x6,3                | TANK VENT CHECK VALVE |
| 20                                                                                            | TANK NO. 3 p   | A-DECK     | 450                  | ST.   | 76,1x6,3                | TANK VENT CHECK VALVE |
| 21                                                                                            | TANK NO. 3 sb  | A-DECK     | 450                  | ST.   | 76,1x6,3                | TANK VENT CHECK VALVE |
| 22                                                                                            | CEN. B. TRUNK  | A-DECK     | 450                  | ST.   | 88,9x7,1                | TANK VENT CHECK VALVE |
| 23                                                                                            | TANK NO. 2 p   | A-DECK     | 450                  | ST.   | 76,1x6,3                | TANK VENT CHECK VALVE |
| 24                                                                                            | TANK NO. 2 sb  | A-DECK     | 450                  | ST.   | 76,1x6,3                | TANK VENT CHECK VALVE |
| 25                                                                                            | TANK NO. 1     | A-DECK     | 450                  | ST.   | 76,1x6,3                | TANK VENT CHECK VALVE |
| 26                                                                                            | FOREPEAK       | A-DECK     | 450                  | ST.   | 88,9x7,1                | TANK VENT CHECK VALVE |

| VENTILATORS  |     |                                     |   |            |                          |           |              |
|-------------------------------------------------------------------------------------------------|-----|-------------------------------------|---|------------|--------------------------|-----------|--------------|
| POS.                                                                                            | OFF | FROM                                | — | TO         | HEIGHT<br>ABOVE<br>DECK. | DIM       | TYPE CLOSING |
| 1                                                                                               | 1   | VENT. ROOM                          | — | A—DECK     | 1000                     | 1000x1000 | WITH HATCH.  |
| 2                                                                                               | 1   | ENG. FRANROOM                       | — | A—DECK     | 1000                     | 1400x1000 | WITH HATCH   |
| 3                                                                                               | 1   | ENG. ROOM                           | — | TOP FUNNEL | 4500                     | 700x1000  | WITH HATCH.  |
| 4                                                                                               |     |                                     |   |            |                          |           |              |
| 5                                                                                               |     | HOLD FOR VENTILATORS FOR VENT PLANT |   |            |                          |           |              |
| 6                                                                                               |     |                                     |   |            |                          |           |              |

| FREEING PORTS |        |        |                  |                     |                   |                      |
|---------------|--------|--------|------------------|---------------------|-------------------|----------------------|
| DECK          | LENGHT | HEIGHT | NUMBER EACH SIDE | POSITION            | AREA EACH OPENING | TOTAL AREA EACH SIDE |
| 1-DECK        | 950 mm | 230 mm | 5                | PORT SIDE ON RAIL   | 0,22 m2           | 1,08 m2              |
| 1-DECK        | 950 mm | 230 mm | 5                | STARB. SIDE ON RAIL | 0,22 m2           | 1,08 m2              |

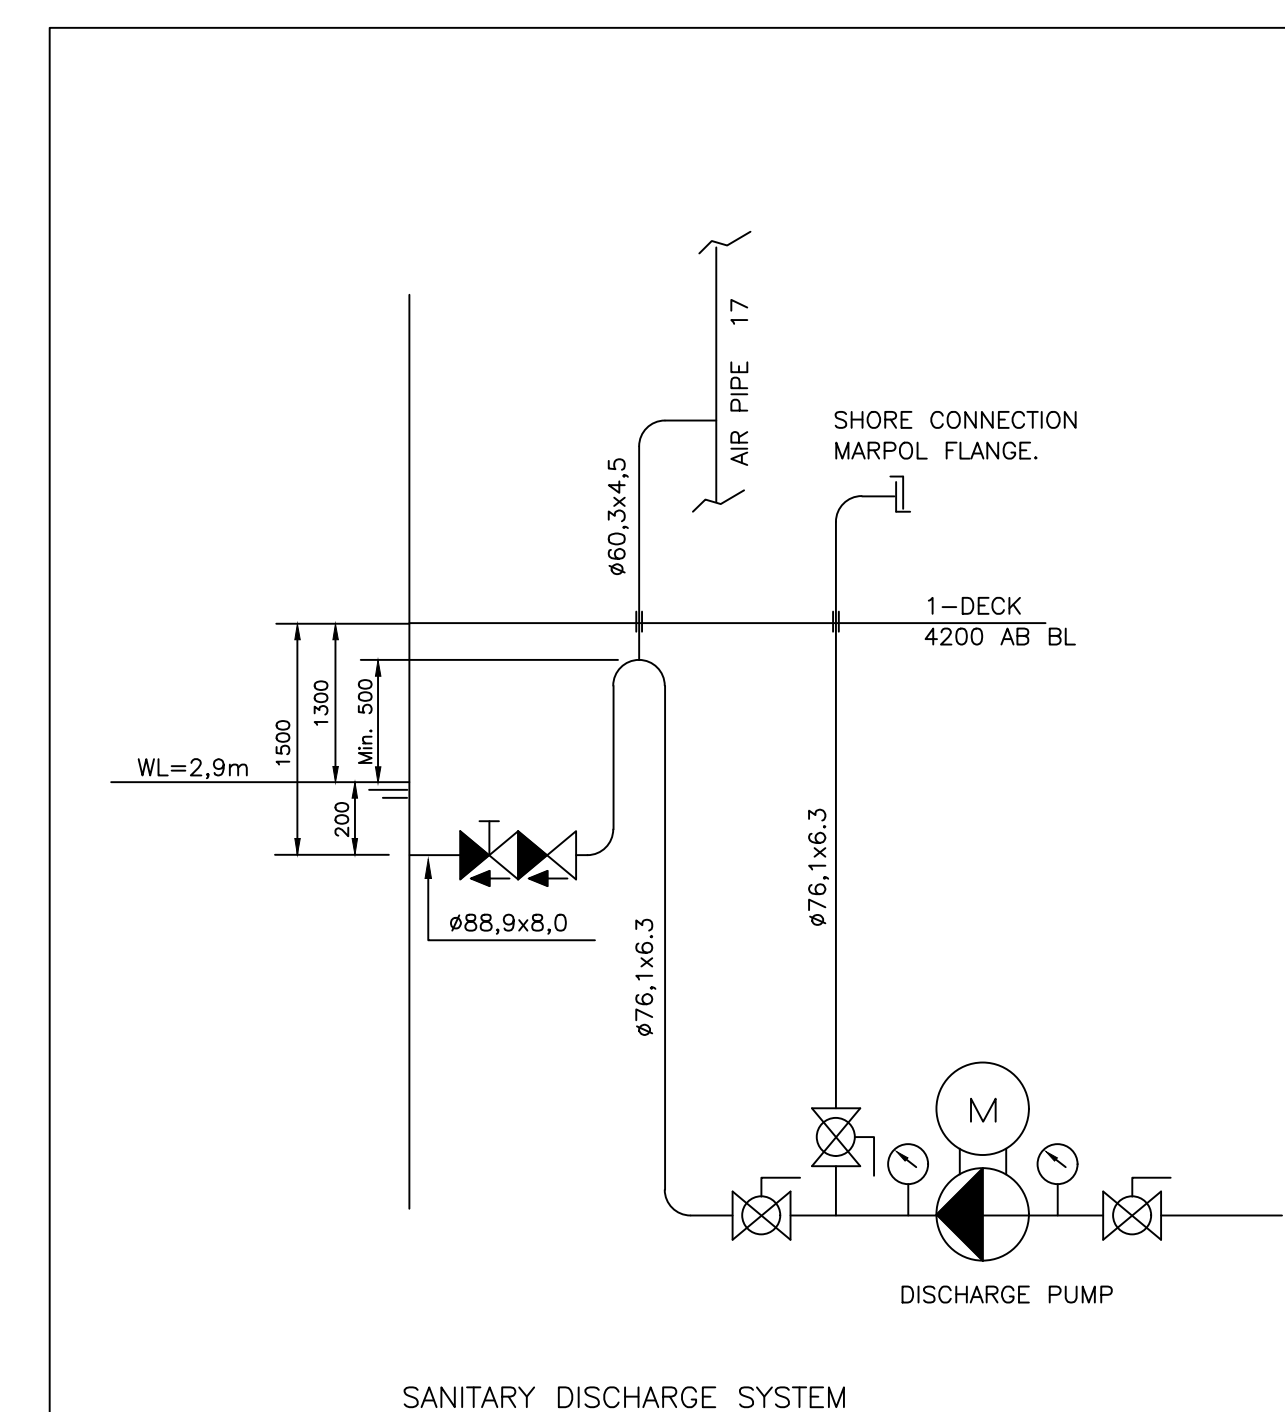

### SANITARY DISCHARGE SYSTEM

| WINDOWS AND SCUTTLES |     |          |           |                |                     |           |       |            |       |        |       |
|----------------------|-----|----------|-----------|----------------|---------------------|-----------|-------|------------|-------|--------|-------|
| POS.                 | OFF | LOCATION | DIMENSION | GLAS THICKNESS | HEIGHT ABOVE A-DECK | DEADLIGHT |       | COAM MATR. | TYPE  | TOGGLE | HING. |
|                      |     |          |           |                |                     | TOGGLE    | HING. |            |       |        |       |
| 1                    | 14  | 1—DECK.  | ø300      | 10             | 1500                |           |       | BR.        | FIXED |        |       |
| 2                    | 2   | A—DECK.  | 900x630   | 12             | 1400                | 2         | 1     | AL.        |       | 2      | 1     |
| 3                    | 6   | A—DECK.  | 900x630   | 12             | 1400                |           |       | AL.        |       |        |       |
| 4                    | 1   | BRIDGE   |           | 15             | 3500                |           |       | AL.        | FIXED |        |       |
| 5                    | 1   | BRIDGE   |           | 15             | 3500                |           |       | AL.        | FIXED |        |       |
| 6                    | 1   | BRIDGE   |           | 15             | 2700                |           |       | AL.        | FIXED |        |       |
| 7                    | 1   | BRIDGE   |           | 15             | 3500                |           |       | AL.        |       | 2      | 1     |
| 8                    | 1   | BRIDGE   |           | 15             | 3500                |           |       | AL.        | FIXED |        |       |
| 9                    | 1   | BRIDGE   |           | 15             | 3500                |           |       | AL.        | FIXED |        |       |
| 10                   | 1   | BRIDGE   |           | 15             | 3500                |           |       | AL.        | FIXED |        |       |
| 11                   | 2   | BRIDGE   |           | 15             | 3500                |           |       | AL.        | SLIDE |        |       |
| 12                   | 2   | BRIDGE   |           | 15             | 3500                |           |       | AL.        | FIXED |        |       |
| 13                   | 1   | BRIDGE   |           | 15             | 3500                |           |       | AL.        | FIXED |        |       |
| 14                   | 2   | BRIDGE   |           | 15             | 3500                |           |       | AL.        | FIXED |        |       |
| 15                   | 1   | BRIDGE   |           | 15             | 3500                |           |       | AL.        | FIXED |        |       |

| DOORS  |             |             |           |              |             |                    |       |
|-------------------------------------------------------------------------------------------|-------------|-------------|-----------|--------------|-------------|--------------------|-------|
| POS.                                                                                      | DECK        | SILL HEIGHT | NOM. DIM. | TYPE         | REMARKS     | TIGHTENING HANDLES | HINGE |
| 1                                                                                         | 1. DECK     | 380         | 980X1680  | WEATHERTIGHT | WITH WINDOW | 6                  | 2     |
| 2                                                                                         | 1. DECK     | 600         | 680X1480  | WEATHERTIGHT |             | 6                  | 2     |
| 3                                                                                         | 1. DECK     | 380         | 680X1680  | WEATHERTIGHT | WITH WINDOW | 6                  | 2     |
| 4                                                                                         | 1. DECK     | 380         | 680X1680  | WEATHERTIGHT | WITH WINDOW | 6                  | 2     |
| 5                                                                                         | A-DECK      | 380         | 680X1680  | WEATHERTIGHT |             | 6                  | 2     |
| 6                                                                                         | A-DECK      | 380         | 680X1680  | WEATHERTIGHT |             | 6                  | 2     |
| 7                                                                                         | A-DECK      | 75          | 800x800   | SPRAYTIGHT.  |             | 2                  | 2     |
| 8                                                                                         | BRIDGE-DECK | 150         | 680X1880  | SPRAYTIGHT.  | WITH WINDOW | 2                  | 2     |

| HATCHES ○ |      |                 |                 |                          |                  |         |              |       |       |         |
|-----------|------|-----------------|-----------------|--------------------------|------------------|---------|--------------|-------|-------|---------|
| POS.      | OFF. | HATCH COAMING   |                 |                          |                  | CLOSING |              |       |       | REMARKS |
|           |      | DIM.<br>OPENING | COAM<br>THICKN. | HEIGHT<br>ABOVE<br>DECK. | HATCH<br>THICKN. | PACKING | TYPE CLOSING |       |       |         |
|           |      |                 |                 |                          |                  |         | TOGGLE       | BOLTS | HINGE |         |
| 1         | 1    | 600x800         | 11              | 600                      | 8                | 40x25   | 3            |       | 2     |         |
| 2         | 1    | 800x600         | 11              | 600                      | 8                | 40x25   | 3            |       | 2     |         |
| 3         | 1    | 1950x2300       | 11              | FLUSH                    | 8                | 40x25   |              | 18    | 2     |         |
| 4         | 1    | 1470x1200       | 11              | 200                      | 8                | 40x25   |              | 12    | 2     |         |
| 5         | 1    | 600x800         | 11              | 600                      | 8                | 40x25   | 3            |       | 2     |         |
| 6         | 1    | 600x800         | 11              | 600                      | 8                | 40x25   | 3            |       | 2     |         |

| SEA OUTLET |              |                                                                                       |                        |         |                   |     |
|------------|--------------|---------------------------------------------------------------------------------------|------------------------|---------|-------------------|-----|
| POS.       | OUTLETS FROM | POSITION OF VALVE OPERATING                                                           | PIPES OUTLET DIMENSION | MATR OF | REMARKS           |     |
| 1          | BALLAST PUMP |  | ø88,9x8,0              | ST.     | OUTLET 3500 ABOVE | BL. |
| 2          | BILGE PUMP   |  | ø88,9x8,0              | ST.     | OUTLET 3500 ABOVE | BL. |
| 3          | SEWAGE PUMP  |  | ø88,9x8,0              | ST.     | OUTLET 3500 ABOVE | BL. |

| SEA INLET |             |                             |                       | ☆       |                      |
|-----------|-------------|-----------------------------|-----------------------|---------|----------------------|
| POS.      | INLETS FROM | POSITION OF VALVE OPERATING | PIPES INLET DIMENSION | MATR OF | REMARKS              |
| 21        | CROSSOVER   | ☒☒                          | ø168,3x10,0           | ST.     | INLET IN ENGINE ROOM |
| 22        | CROSSOVER   | ☒☒                          | ø168,3x10,0           | ST.     | INLET IN ENGINE ROOM |

| MAIN PARTICULARS        |                             |
|-------------------------|-----------------------------|
| LENGTH OVER ALL         | 36.25 [m]                   |
| LENGTH BETV. PERP.      | 33.90 [m]                   |
| BREADTH MOULDED         | 9.60 [m]                    |
| DEPTH TO 1-LOCK         | 4.287 [m]                   |
| DEPTH TO A-DECK         | 6.687 [m]                   |
| DRAUGHT NORM. OPERATIVE | 2.50 [m]                    |
| DRAUGHT MAX. LOADED     | 2.789 [m]                   |
| SCANTLING DRAUGHT       | 2.90 [m]                    |
| GROSS TONNAGE           | 430 [GT]                    |
| FRAME DISTANCE          | 500 [mm]                    |
| CLASS                   | Sigefartsdirektoratet (NM0) |
| ACCORDING TO            | DNV +A1 Ice C E0 RD         |
| DEADWEIGHT AT d=2786    | 169 [t]                     |
| TRADING UNIT            | SMALL COASTAL TRADE         |
| BUILT YEAR              | 2005                        |

|   |  |                  |                |
|---|--|------------------|----------------|
| PROJECT: <b>FF</b>   |  | DATE: 31/08/2026 |                |
| <b>GUNNERUS -LNVZ-<br/>FREEBOARD PLAN</b>   |  | SCALE:<br>1:100  | SHEETS:<br>1/1 |
| <p>Open use for research/teaching and other non-commercial activities<br/>         Commercial use is not permitted without approval (CC BY-NC 4.0)</p>                                   |  |                  |                |
|  <b>NTNU</b>                                                                                        |  |                  |                |
| <p>This drawing is a derivative work made by C-JOB and NTNU, based on the R/V Gunnerus open repository drawings, courtesy of Polarkonsult, published by NTNU. Licensed CC BY-NC 4.0.</p> |  |                  |                |