




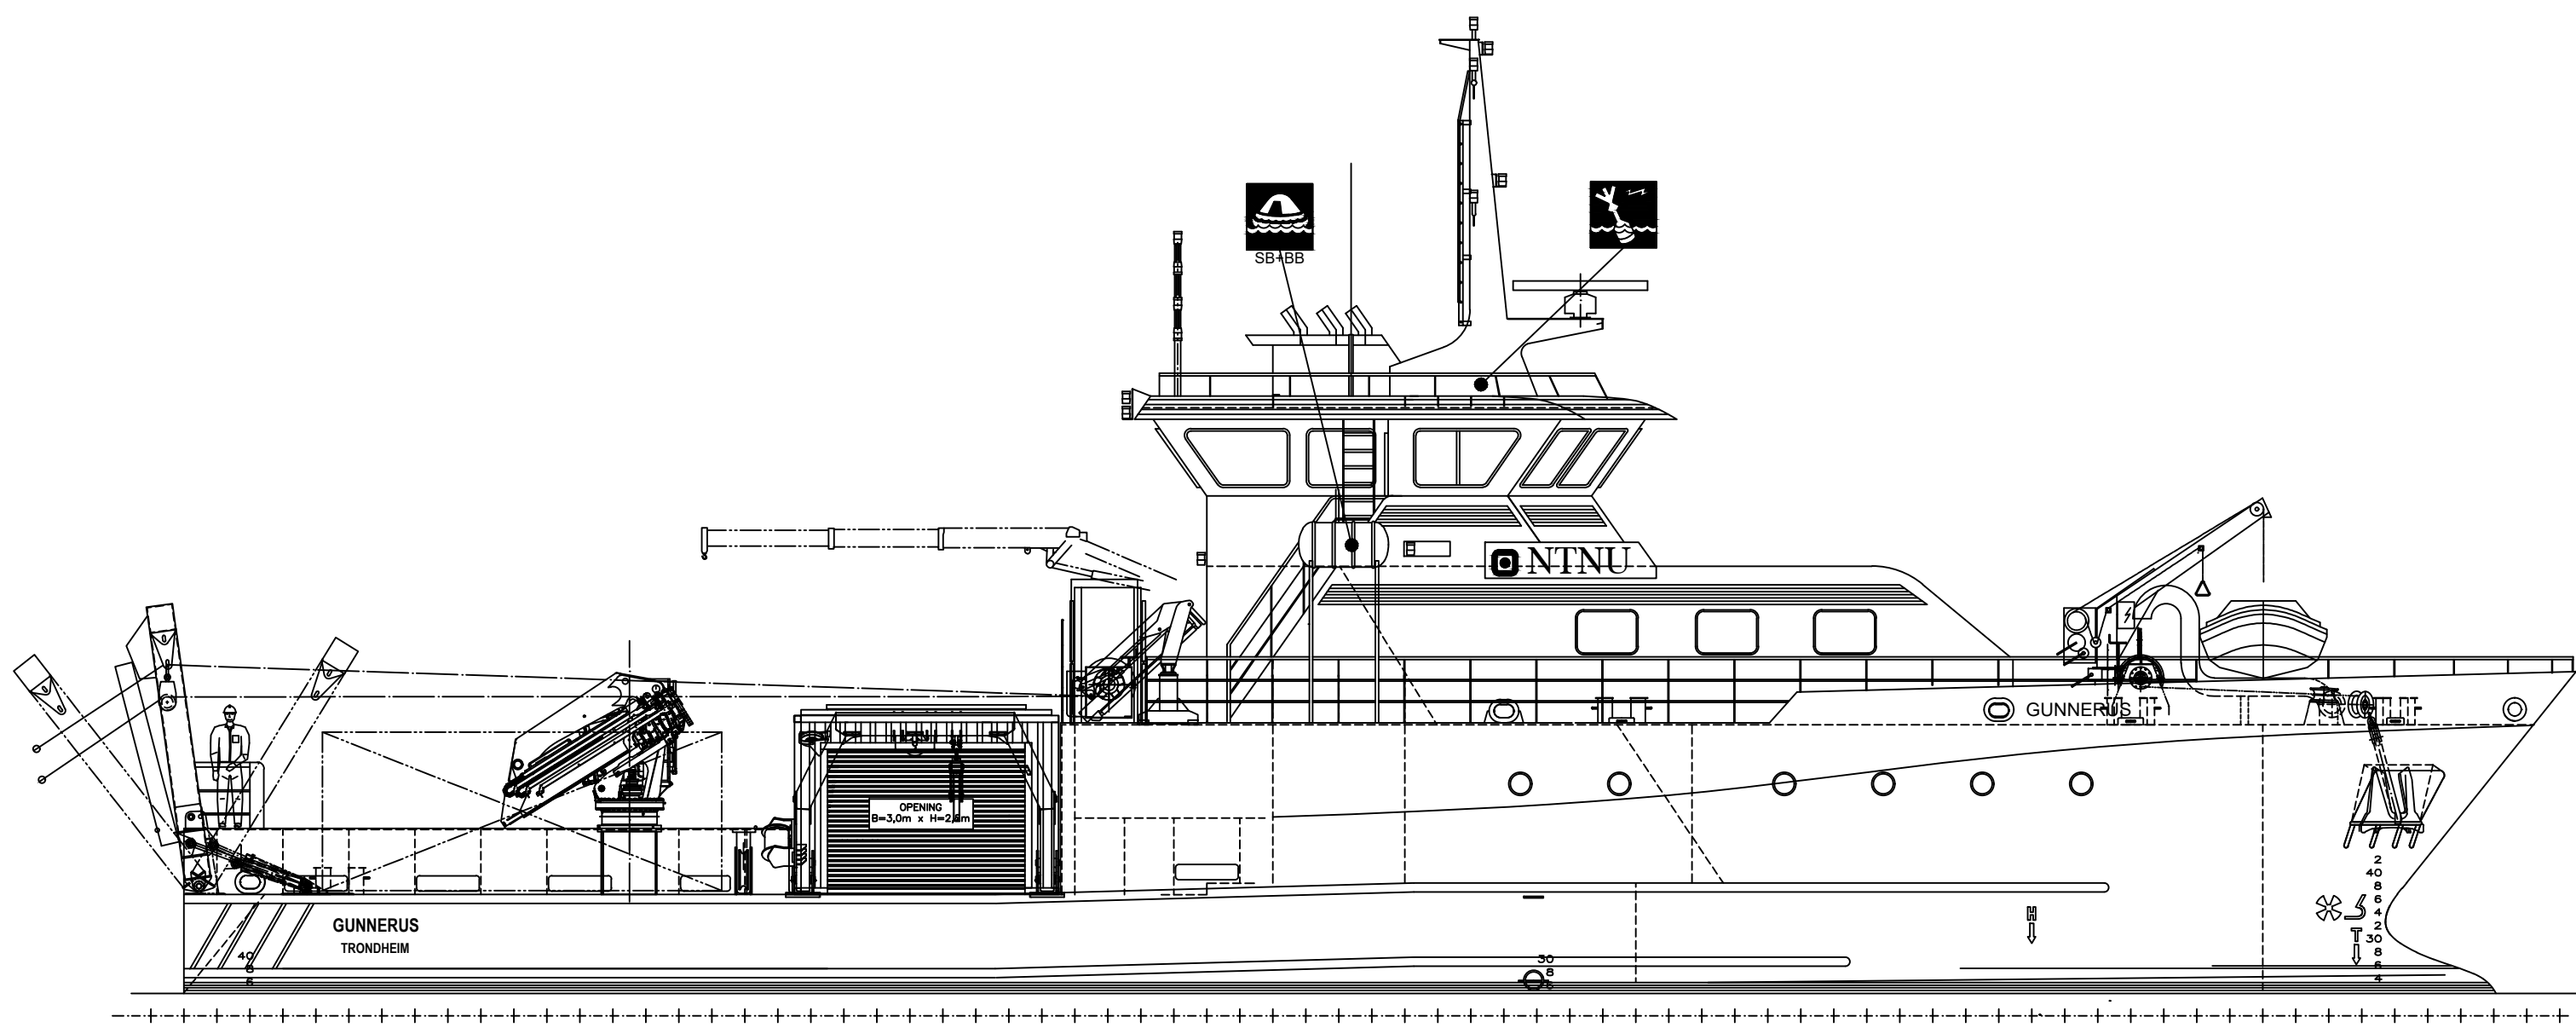


PROFILE

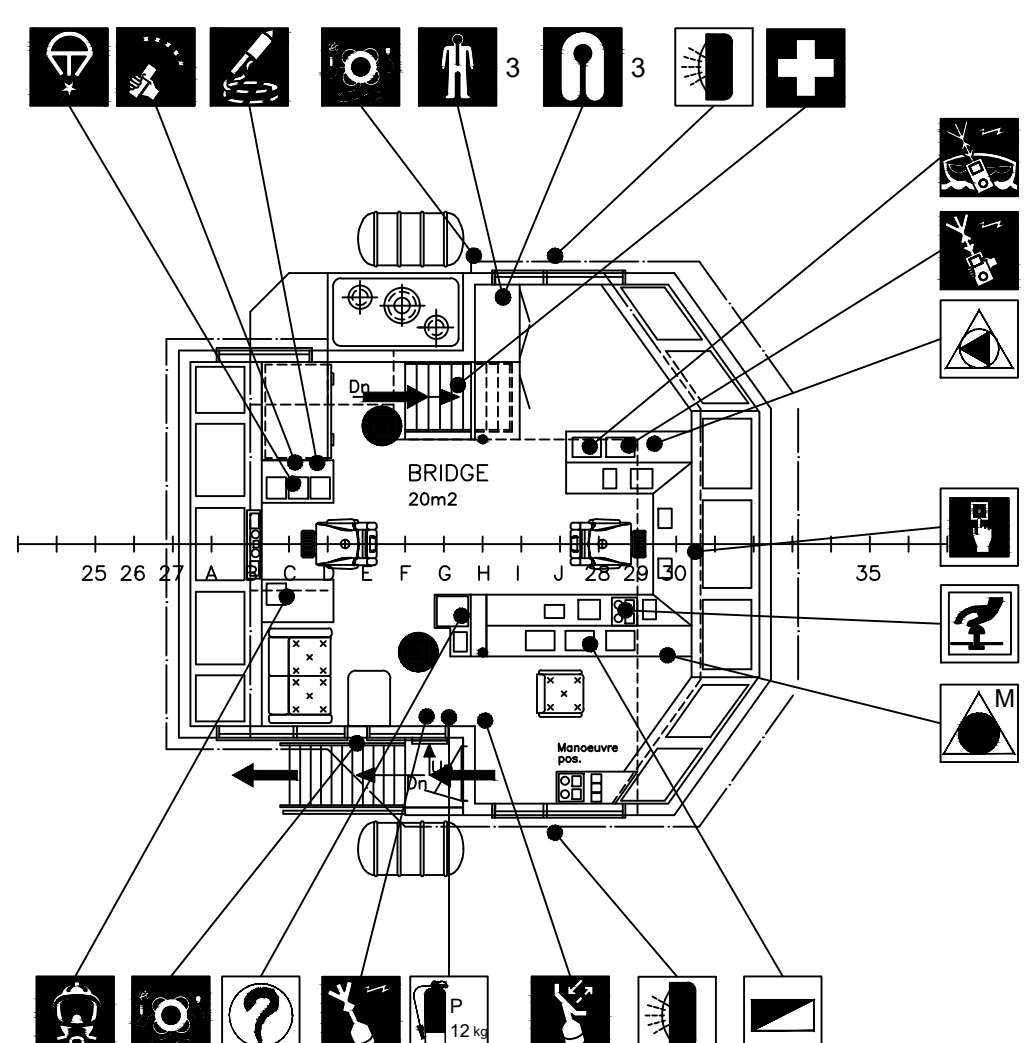


WHEEL HOUSE

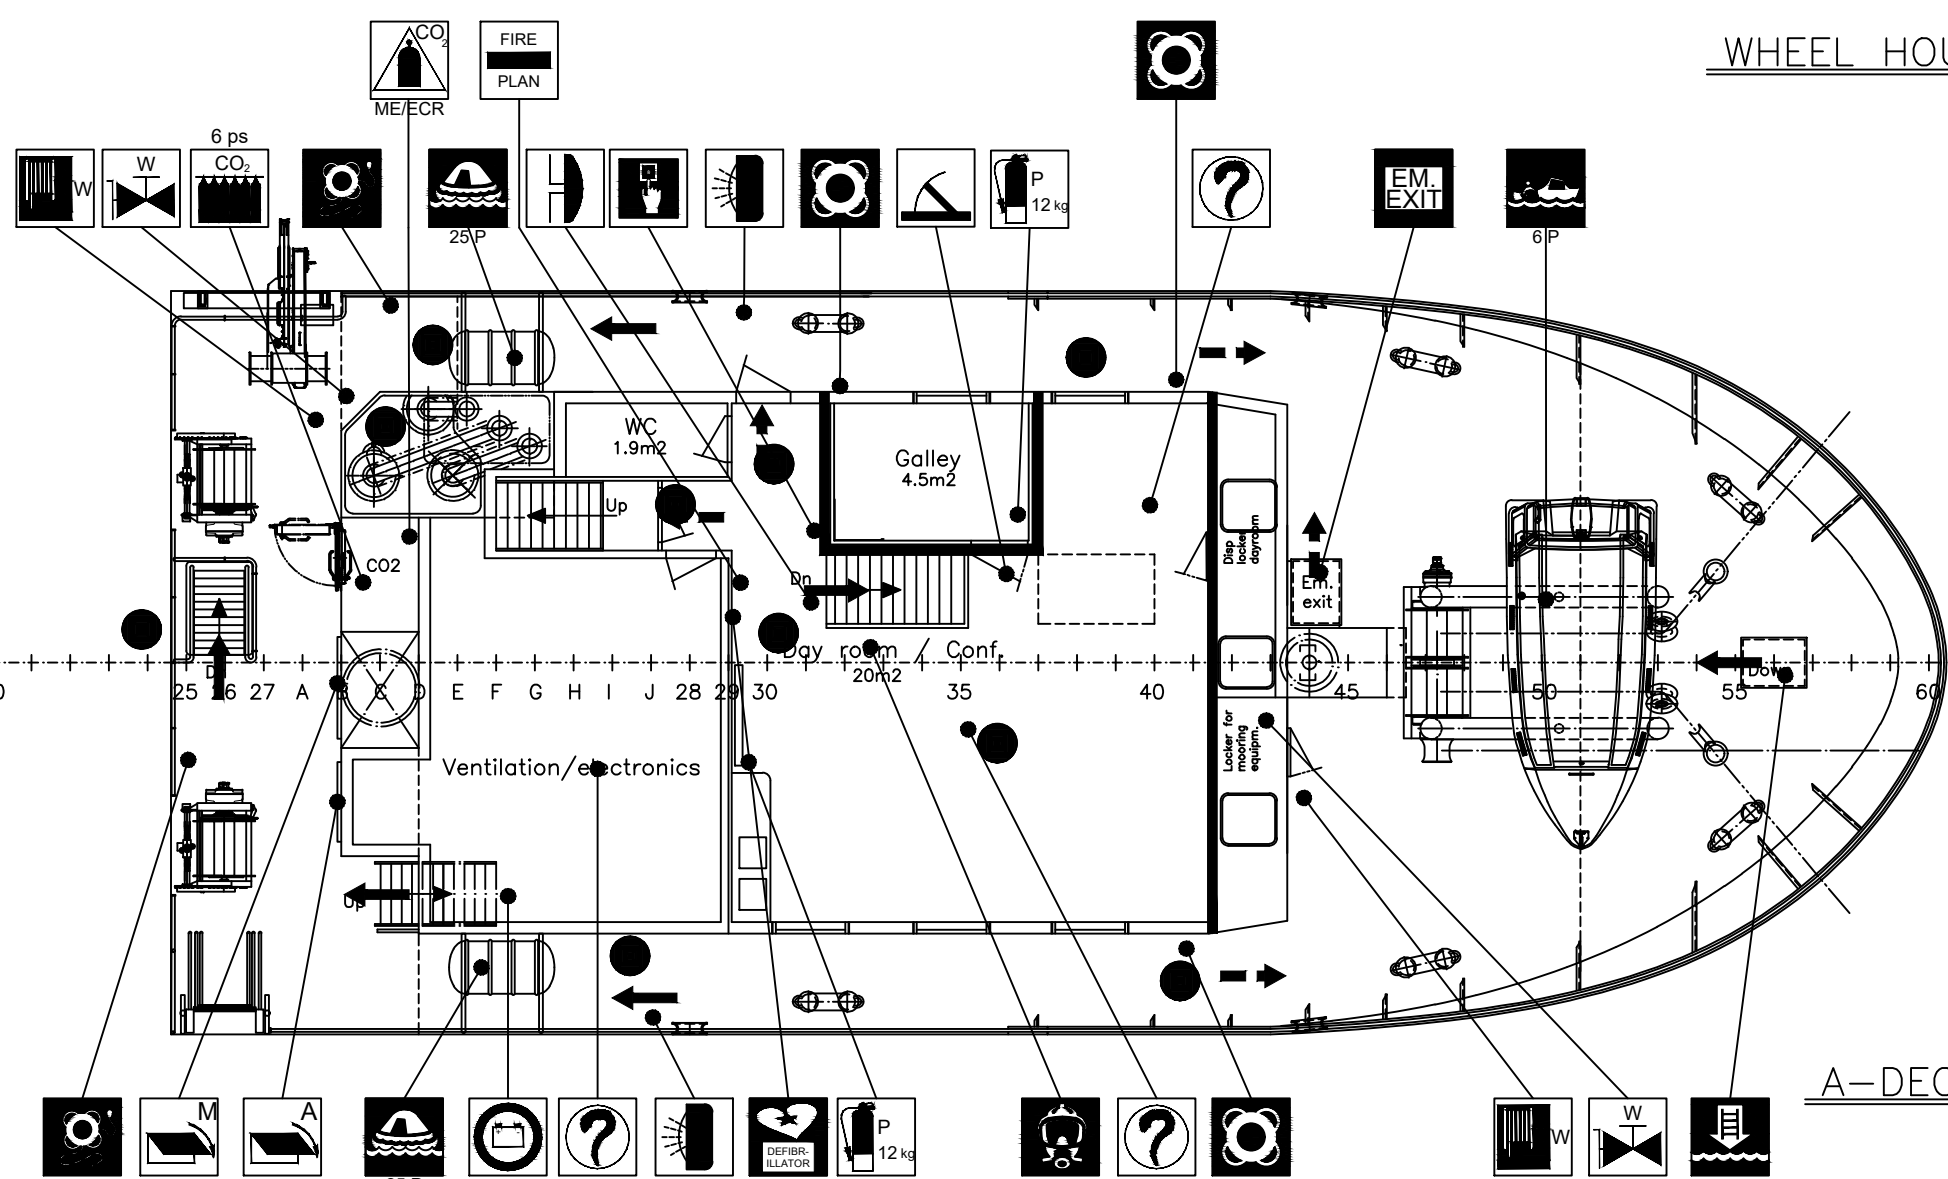

A-DECK

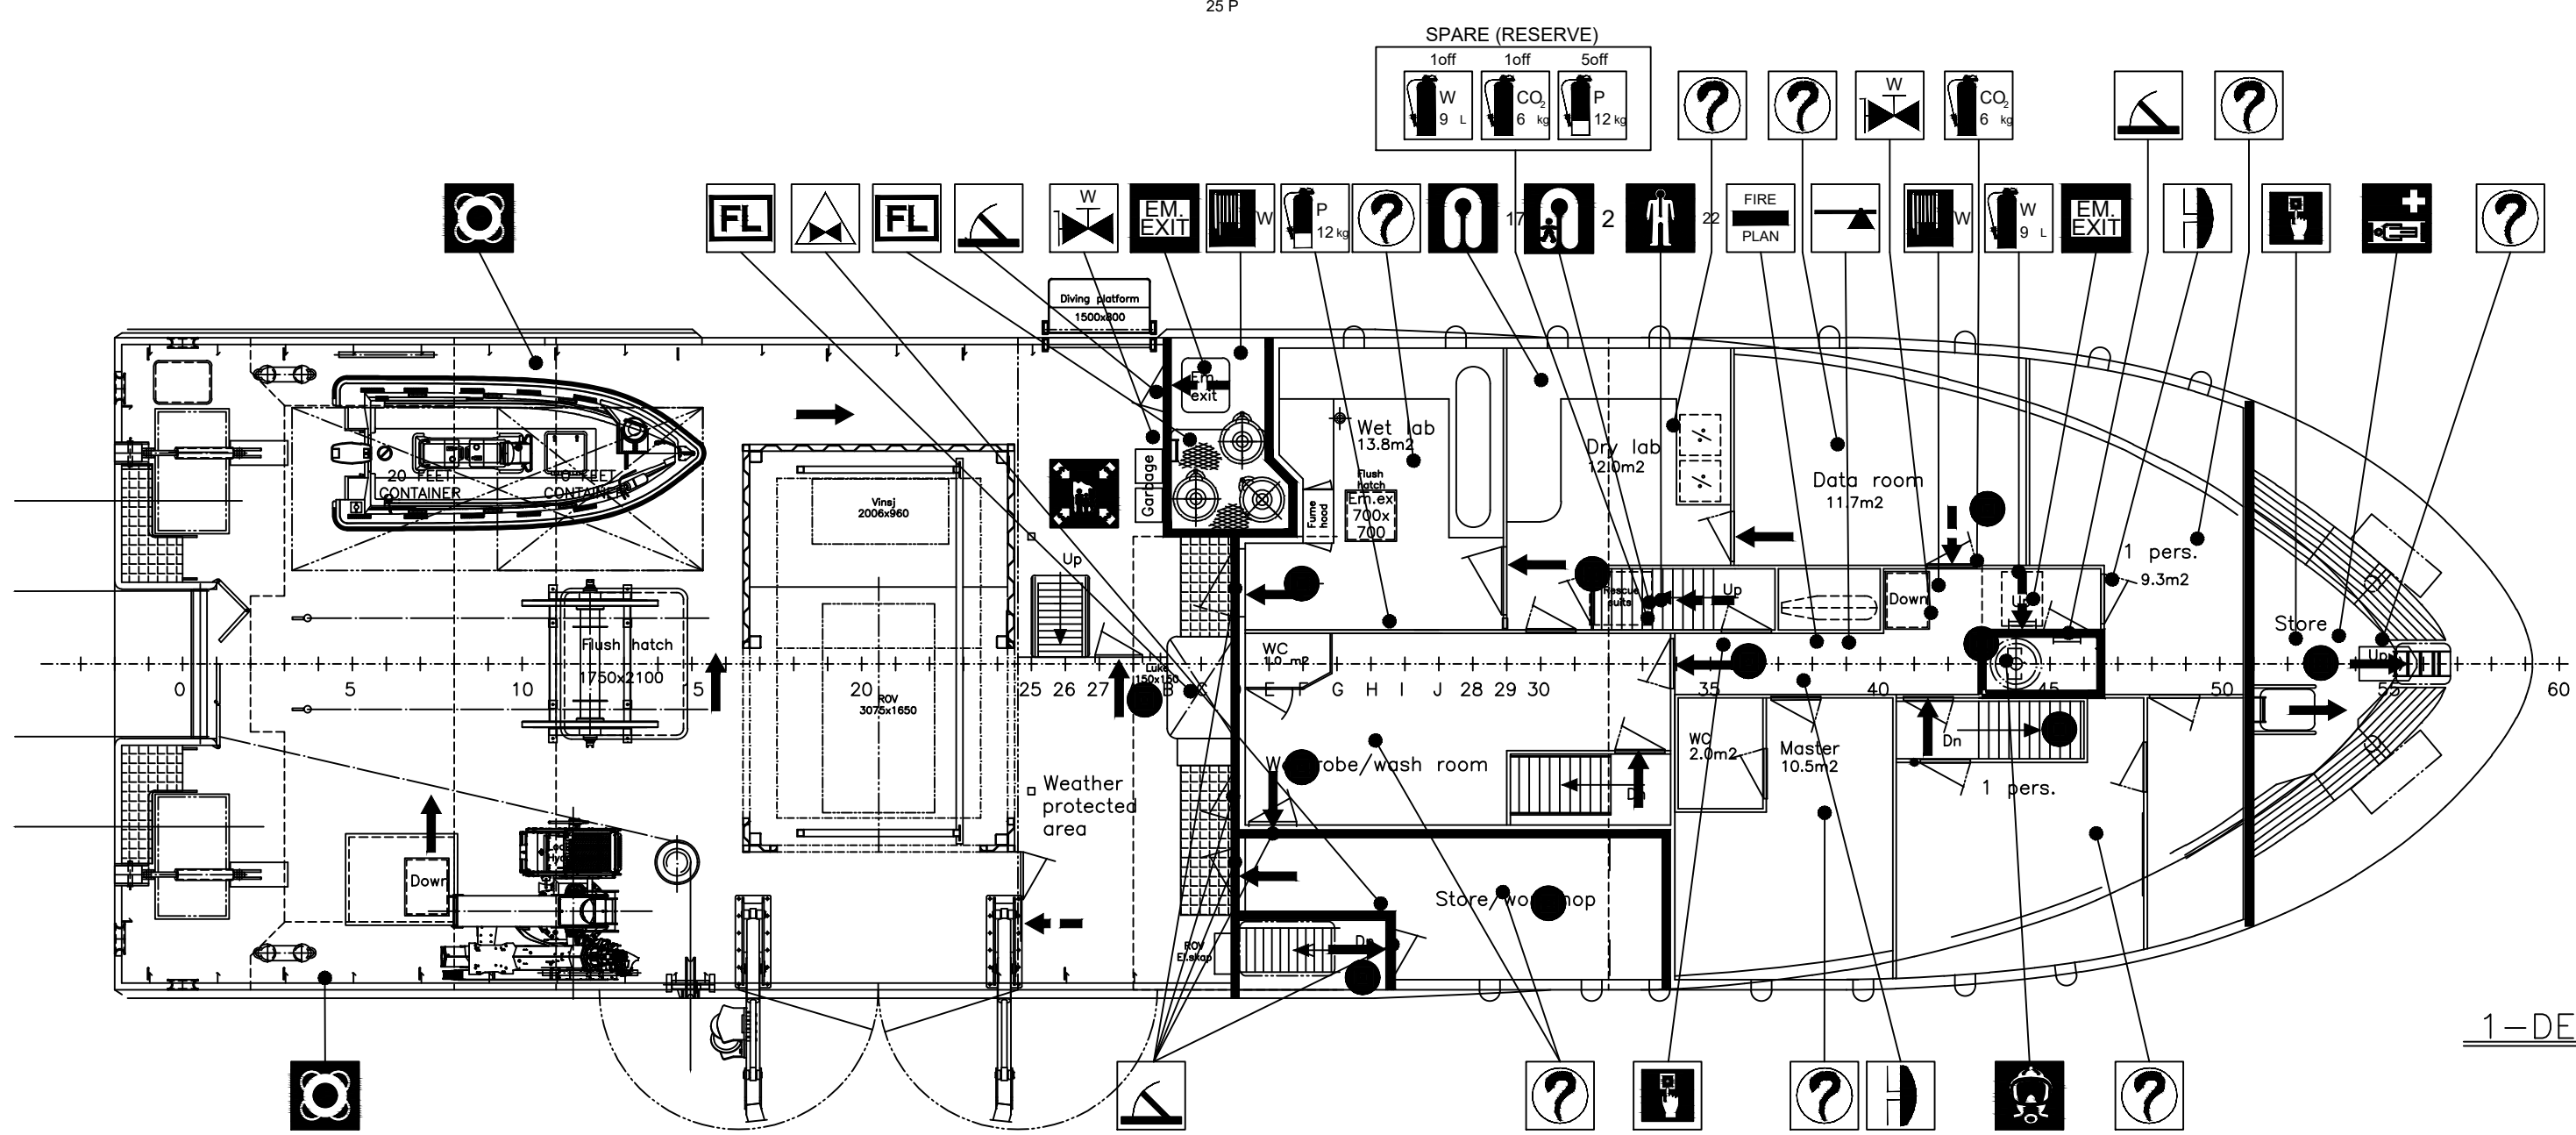

1-DECK

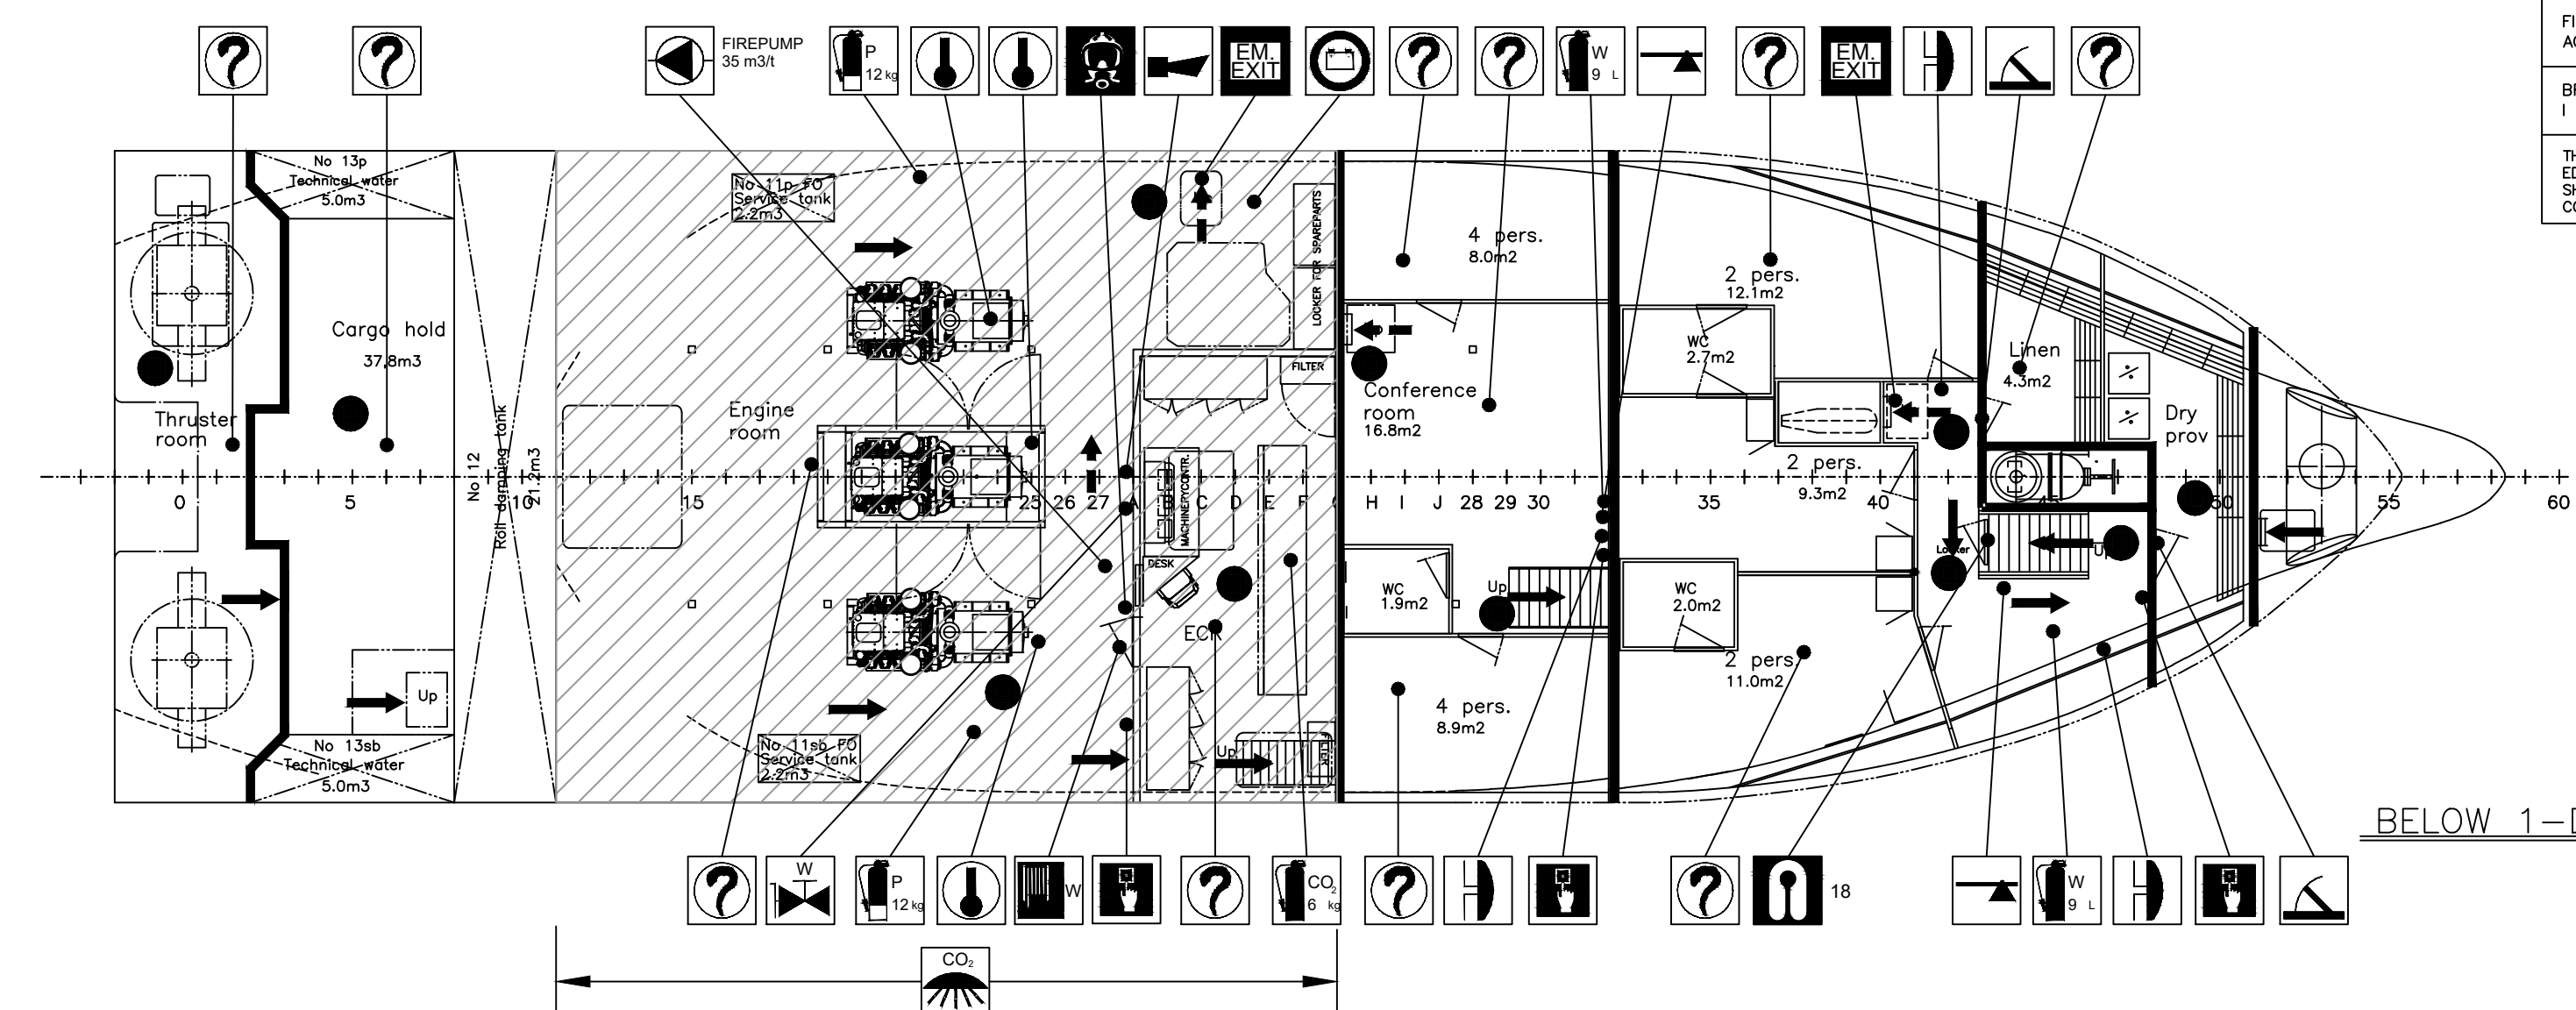

BELOW 1-DECK

FIREPROTECTION METHOD IC
ACCORDING TO SOLAS II-2 §7.5.5
BRANNBESKYTTELSEMETODE IC
IF HET SOLAS II-2 §7.5.5
THIS DOCUMENT IS INTENDED FOR
EDUCATIONAL PURPOSES ONLY AND
SHALL NOT BE USED FOR
CONSTRUCTION OR CONTRACTUAL

SYMBOL	NO. ANT.	DESCRIPTION UTSTYR	COMMENT ANMERKNING
	2	FIRE CONTROL PLAN BRANNKONTROLLPLAN	
	1	FIRE PUMP BRANNPUMPE	35 M ³ /HOUR - 6 BAR
	1	REMOTE CONTROL FOR FIRE PUMP FJERNKONTROLL FOR BRANNPUMPE	35 M ³ /TIME - 6 BAR
	5	FIRE HYDRANT FOR WATER BRANN HYDRANT FOR VANN	
	5	FIREHOSE AND NOZZLE FOR WATER BRANNSLANGE OG STRÅLERØR FOR VANN	
	1	FIXED FIRE-EXTINGUISHING BATTERY WITH CO ₂ FAST SLUKKESYSTEMBATTERI MED CO ₂	6 STK. BOTTLES
	1	REMOTE RELEASE STATION FOR CO ₂ FJERNUTSLÅNING FOR CO ₂	6 STK. FLÅSKER
	3	SPACES OR GROUP OF SPACES PROTECTED BY CO ₂ ROM ELLER OMRÅDER BESKYTTET MED CO ₂	
	3	FIRE EXTINGUISHER, POWDER, 12KG BRANNSLUKKEAPPARAT, PULVER, 12KG	INCLUDE 4 SPARES INKLUDERER 4 I RESERVE
	11	FIRE EXTINGUISHER, WATER, 5L BRANNSLUKKEAPPARAT, VANN, 5L	INCLUDE 1 SPARE INKLUDERER 1 I RESERVE
	4	FIRE EXTINGUISHER, CO ₂ , 6KG BRANNSLUKKEAPPARAT, CO ₂ , 6KG	INCLUDE 1 SPARE INKLUDERER 1 I RESERVE
	2	FIRE LOCKER SKAP MED BRANNMANNSUTSTYR	
	9	A-CLASS DIVISION A-KLASSE BRANNSKILLE	
	9	A-CLASS HINGED FIRE DOOR A-KLASSE HINGSELT BRANNØR	

SYMBOL	NO. ANT.	DESCRIPTION UTSTYR	COMMENT ANMERKNING
	1	RESCUE BOAT MANN-OVER-BOARD BÅT	CAPACITY: 6 PERSONS KAPASITET: 6 PERSONER
	1	EMERGENCY LADDER EMERGENSISSTIGE	
	2	LIFEBUOY REDDINGSFLÅTE	CAPACITY: 25 PERSONS KAPASITET: 25 PERSONER
	38	LIFEBUOY REDDINGSØST	
	2	LIFEBUOY FOR CHILDREN REDDINGSØST FOR BARN	
	25	IMMERSION SUITE REDDINGSØRØR	3 SUITS TO BE KEPT ON BRIDGE 3 ØRØRER OPPEBEVARES PÅ BRO
	4	EMERGENCY ESCAPE BREATHING DEVICE (EEBD) FLUKTMASKE	... SPARE ... RESERVE
	5	LIFEBUOY LVBØYE	
	2	LIFEBUOY WITH LIGHT, LINE AND SMOKE LVBØYE MED LYS, LINJE OG RØK	
	2	LIFEBUOY WITH LIGHT AND LINE LVBØYE MED LYS OG LINJE	
	2	LINE THROWING APPLIANCE LINEKASTERAPPARAT	
	3	EMERGENCY EXIT NØDUTGANG	
	1	MEDICAL LOCKER SKAP MED MEDISK UTSTYR	
	1	STRETCHER STYKEMÅR	
	1	DEFIBRILLATOR HJERTESTARTER	
	1	ASSEMBLY STATION MINSTRINGSSTASJON	
	1	PRIMARY ESCAPE ROUTE PRIMÆR REKKINGSGANG	
	1	ALTERNATIVE ESCAPE ROUTE ALTERNATIV REKKINGSGANG	
	33	EMERGENCY LIGHT NØDLYS	
	4	FLOODLIGHT FOR LIFESAVING OPERATIONS LYS FOR UTSETTING AV REDDINGSUTSTYR	

SYMBOL	NO. ANT.	DESCRIPTION UTSTYR	COMMENT ANMERKNING
	1	CONTROL PANEL FOR FIRE DETECTION AND ALARM BRANNPANEL FOR DETEKSJON OG ALARM	
	7	MANUALLY OPERATED CALL POINT MANUELL BRANNKJØLER	
	6	BELL ALARM FIRE ALARMKLOKKE BRANN	
	1	HORN FOR FIRE VARSSELHORN FOR BRANN	CO ₂ CO ₂
	NO. ANT.	EMERGENCY RADIO EQUIPMENT AND DISTRESS SIGNALS NØDRADIOUTSTYR OG NØDSIGNALER	COMMENT ANMERKNING
	1	ROCKET PARACHUTE FLARES FALLSKJERMARKETTER	6 PCS 6 STK
	1	HANDFLARE HÅNDFLÅRE	6 PCS 6 STK
	1	EMERGENCY POSITION INDICATING RADIO BEACON NØDPELSENDER	TO BE KEPT ON BRIDGE OPPEBEVARES PÅ BRO
	1	TWO-WAY VHF RADIO APPARATUS TVOVEIS VHF RADIOAPPARAT	TO BE KEPT ON BRIDGE OPPEBEVARES PÅ BRO
	2	SEARCH AND RESCUE DEVICE LETTESØKESIGNAL	TO BE KEPT ON BRIDGE OPPEBEVARES PÅ BRO
	1	FREEFALL EMERGENCY POSITION INDICATING RADIO BEACON FRIEFALL NØDPELSENDER	EFPIB
	1	RESCUE CRAFT TRANSCIVER RADIO TIL REDDINGSFARTØY	TO BE KEPT ON BRIDGE OPPEBEVARES PÅ BRO
	5	EMERGENCY SOURCE OF ELECTRICAL POWER NØDSTRØMKILDE (BATTERI)	

SYMBOL	NO. ANT.	DESCRIPTION UTSTYR	COMMENT ANMERKNING
	1	VENTILATION SHUT-OFF STENING AV VENTILASJON	
	1	CLOSING DEVICE FOR VENTILATION INLET OR OUTLET FOR ACCOMMODATION & SERVICE SPACES LUKKEENHET FOR VENTILASJON TIL ELLER FRA BO-OMRÅDE	
	1	CLOSING DEVICE FOR VENTILATION INLET OR OUTLET FOR MACHINERY SPACES LUKKEENHET FOR VENTILASJON TIL ELLER FRA MASKINROM	
	1	EMERGENCY STOP MAINTHRUSTER NØDSTOP: HOVED THRUSTER	

SYMBOL	NO. ANT.	DESCRIPTION UTSTYR	COMMENT ANMERKNING
	1	DETECTORS FOR AUTOMATIC FIRE ALARM DETEKTORE FOR AUTOMATISK BRANNALARM	
	1	SPACE OR GROUP OF SPACES MONITORED BY HEAT DETECTOR ROM ELLER OMRÅDE OVERVAKET MED VARMEDETECTOR	
	23	SPACE OR GROUP OF SPACES MONITORED BY SMOKE DETECTOR ROM ELLER OMRÅDE OVERVAKET MED RØKDETEKTORE	

SYMBOL	NO. ANT.	DESCRIPTION UTSTYR	CONTENT FOR EACH SET OF FIREMAN'S OUTFIT INNHOLD I HVERT SETT BRANNMANNSUTSTYR
	1	COMPRESSED AIR BREATHING APPARATUS FRISKLUFTMASKE	1 FIRE RESISTANT PROTECTIVE CLOTHING BRANNRESISTENT BESKYTTELSESDRÅKT
	1	VOLUME OF AIR-CYLINDERS: 1200 LTR VOLUM AV LUFT-CYLINDER: 1200 LTR	1 FIRE RESISTANT BOOTS BRANNRESISTENT SKO
	1	VOLUME SPARE BOTTLES: 2400 LTR VOLUM RESERVE FLÅSKER: 2400 LTR	1 FIRE RESISTANT GLOVES BRANNRESISTENT HANSKER
	1	FIRE RESISTANT SAFETY LINE (45m) BRANNRESISTENT SIKKERHETSLINJE (45m)	1 SAFETY HELMET SIKKERHETSHJELM
	1	FIRE RESISTANT SAFETY BELT BRANNRESISTENT SIKKERHETSELSE	1 FIRE AXE BRANNØR
	1	SAFETY LAMP W/BATTERY (RSD) SIKKERHETSLAMPE M/BATTERI (RSD)	

MAIN PARTICULARS

LENGTH OVER ALL	36.25	[m]
LENGTH BETW. PERP.	33.90	[m]
BREADTH MOULDED	9.60	[m]
DEPTH TO 1-DECK	4.293	[m]
DEPTH TO A-DECK	6.687	[m]
DRAUGHT NORM. OPERATIVE	2.50	[m]
DRAUGHT MAX. LOADED	2.787	[m]
SCANTLING DRAUGHT	2.96	[m]
GROSS TONNAGE	430	[GT]
CLASS	Sjøfartsdirektoratet (NMN)	
ACCORDING TO	DNV x1st ice E E9 R2	
DEADWEIGHT AT d=2.786	169	[t]
FARTSOMRÅDE	LITEN KYSTFART	
BUILT YEAR	2006	

BASED ON DNO. SAFETY FIRE ZONE PLAN RevG		DATE: 11/09/2026	
PROJECT:	GUNNERUS - LNVZ - SAFETY FIRE ZONE PLAN	SCALE:	1:100
		SHEETS:	1/1
Open use for research/teaching and other non-commercial activities Commercial use is not permitted without approval (CC BY-NC 4.0)			
This drawing is a derivative work made by C-JOB and NTNU. Based on the R/V Gunnerus open repository drawings, courtesy of Polarconsult, published by NTNU. Licensed CC BY-NC 4.0.			